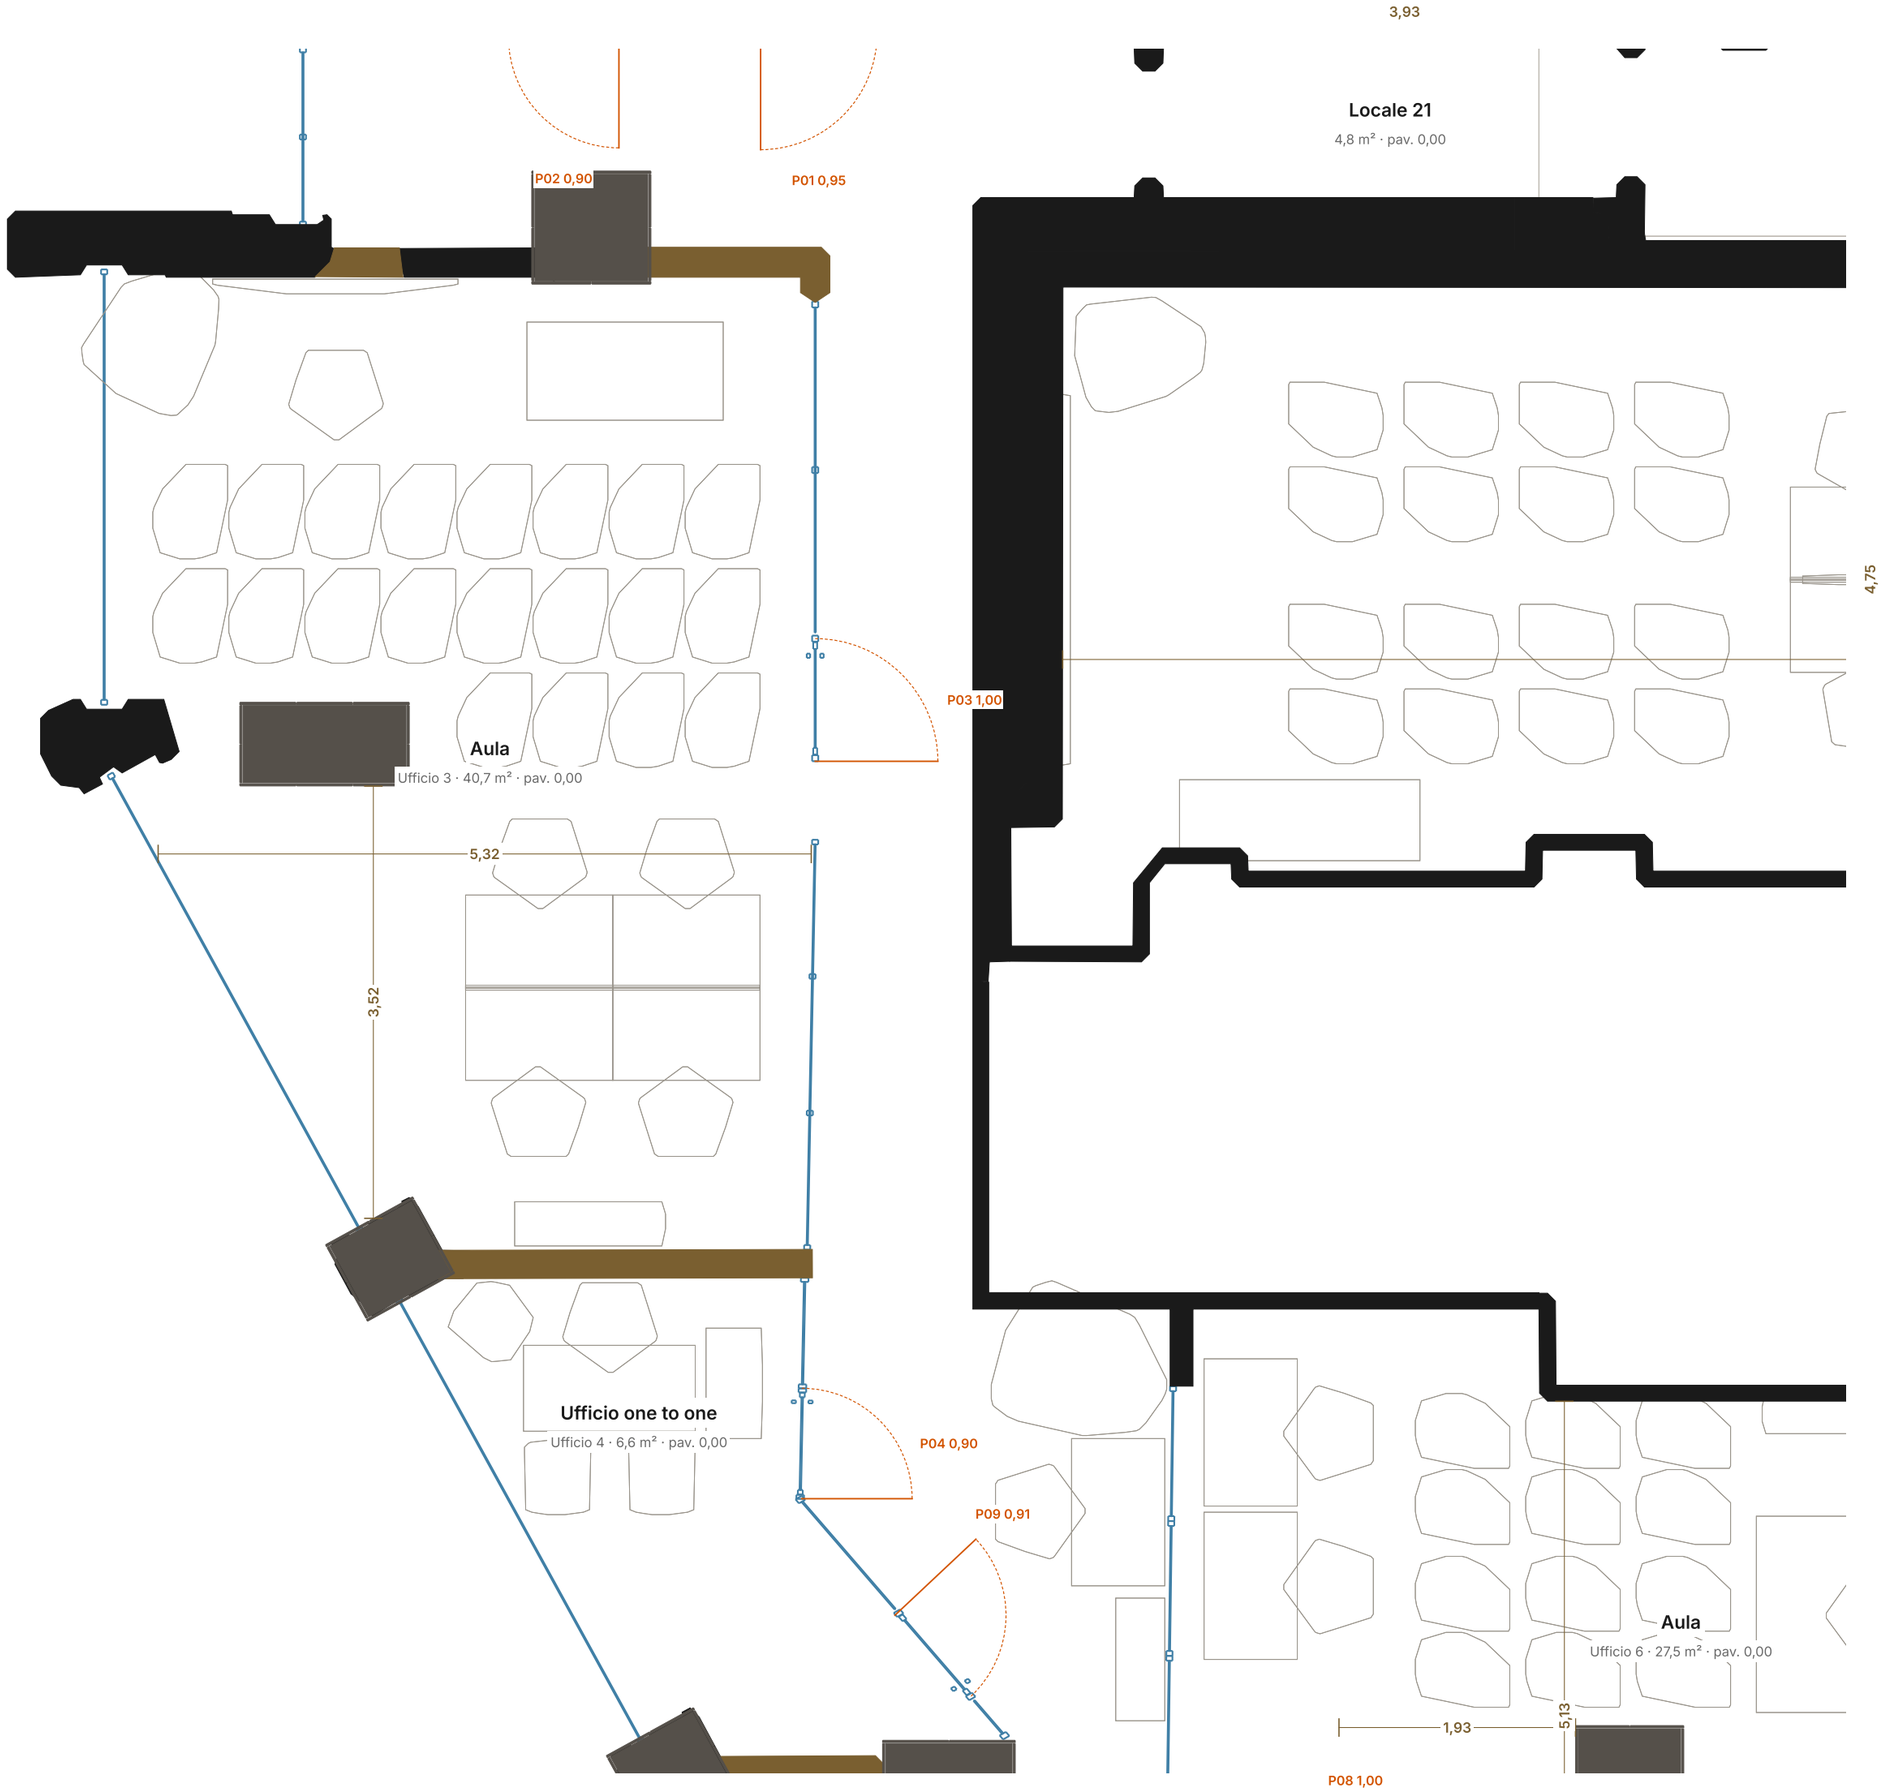


FUTURA
FORMAZIONE • LAVORO

TAVOLA D05

Aula 3
e one to one

Uffici 3 e 4

LEGENDA

- Murature esistenti
- Murature nuove
- Pilastri
- Vetrate e vetrine
- Scale
- Arredi e sanitari
- Misure nette (m)

SCALA 1:50 SU FOGLIO A3

0 — 2 m

VISIO Studio · Michelessi Corporation Srl
Bozza del 9 novembre 2026