
FUTURA
FORMAZIONE • LAVORO

TAVOLA D02

Aule 9, 10 e 11

Lato sud

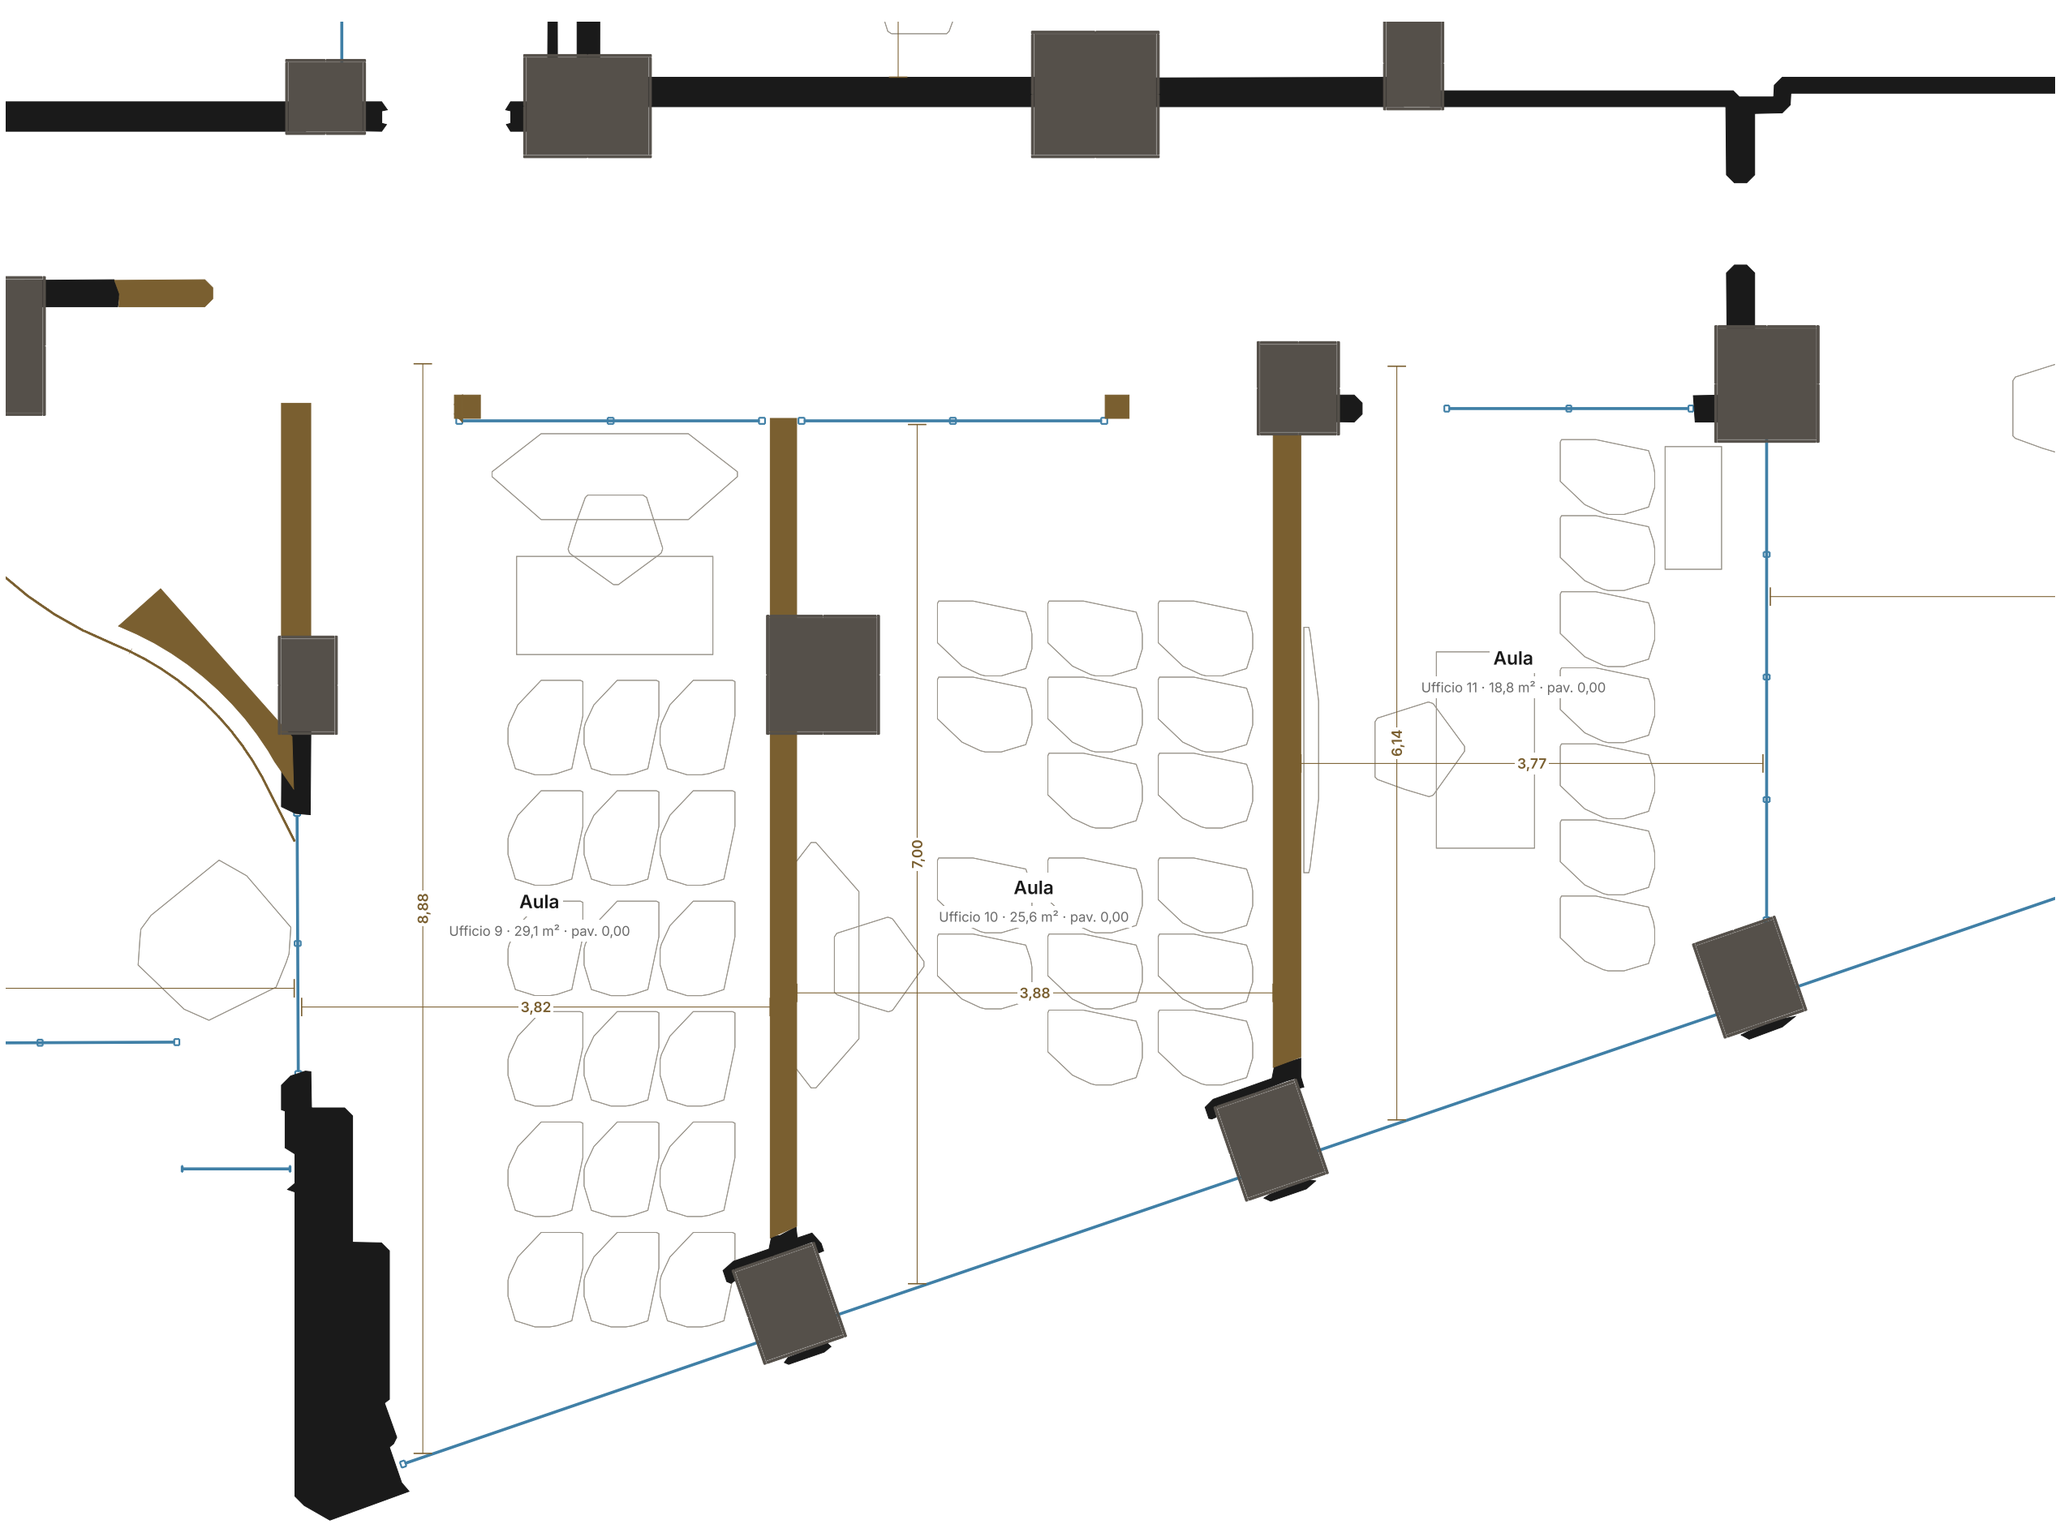

LEGENDA

- Murature esistenti
- Murature nuove
- Pilastri
- Vetrate e vetrine
- Scale
- Arredi e sanitari
- Misure nette (m)

SCALA 1:50 SU FOGLIO A3

0 2 m

VISIO

VISIO Studio · Michelessi Corporation Srl
Bozza del 7 novembre 2026