

Sezione B–B

Aula 6, laboratorio, corridoio, soppalco e bagni · 1:50

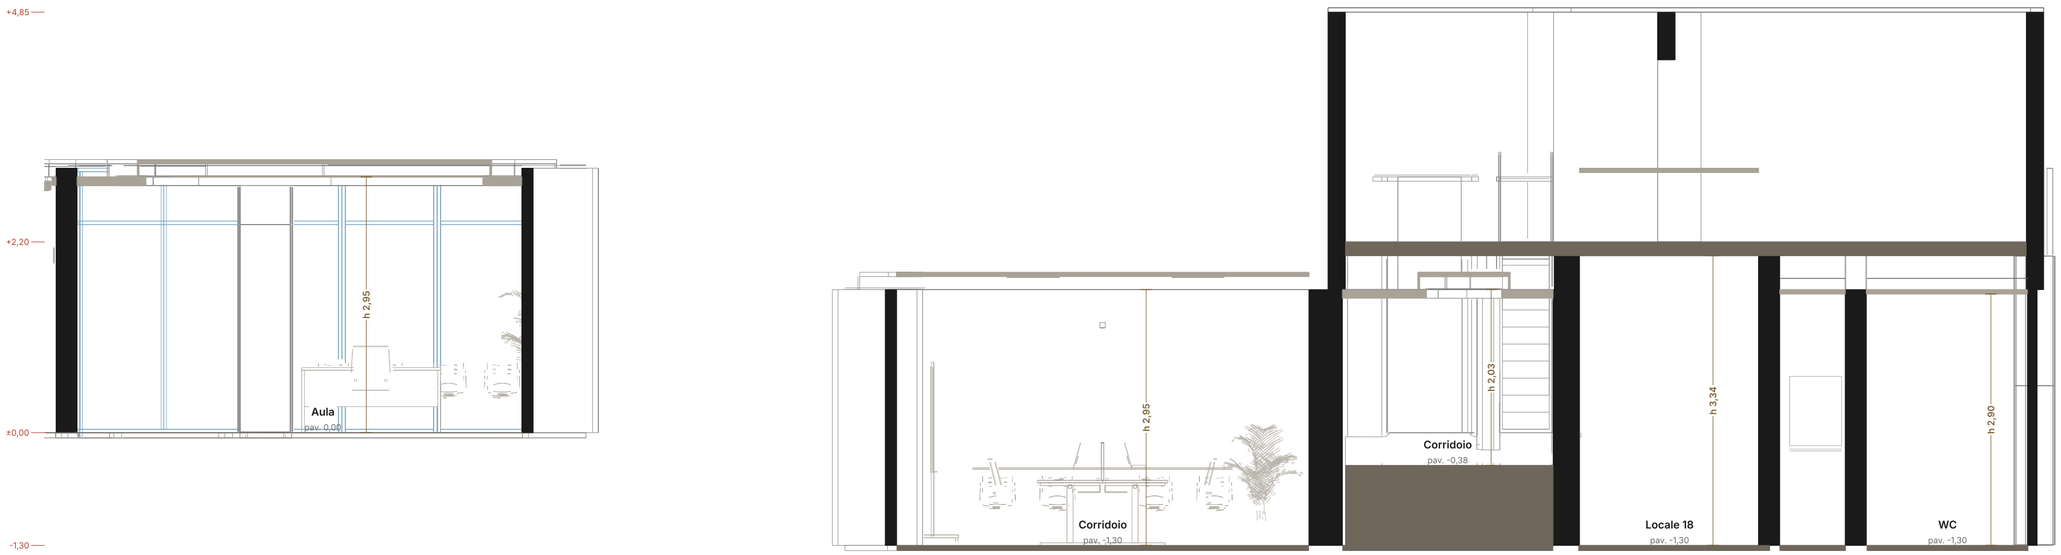

Sezione D–D

Vetrina, Aula 10, reception e Ufficio 7 · 1:50

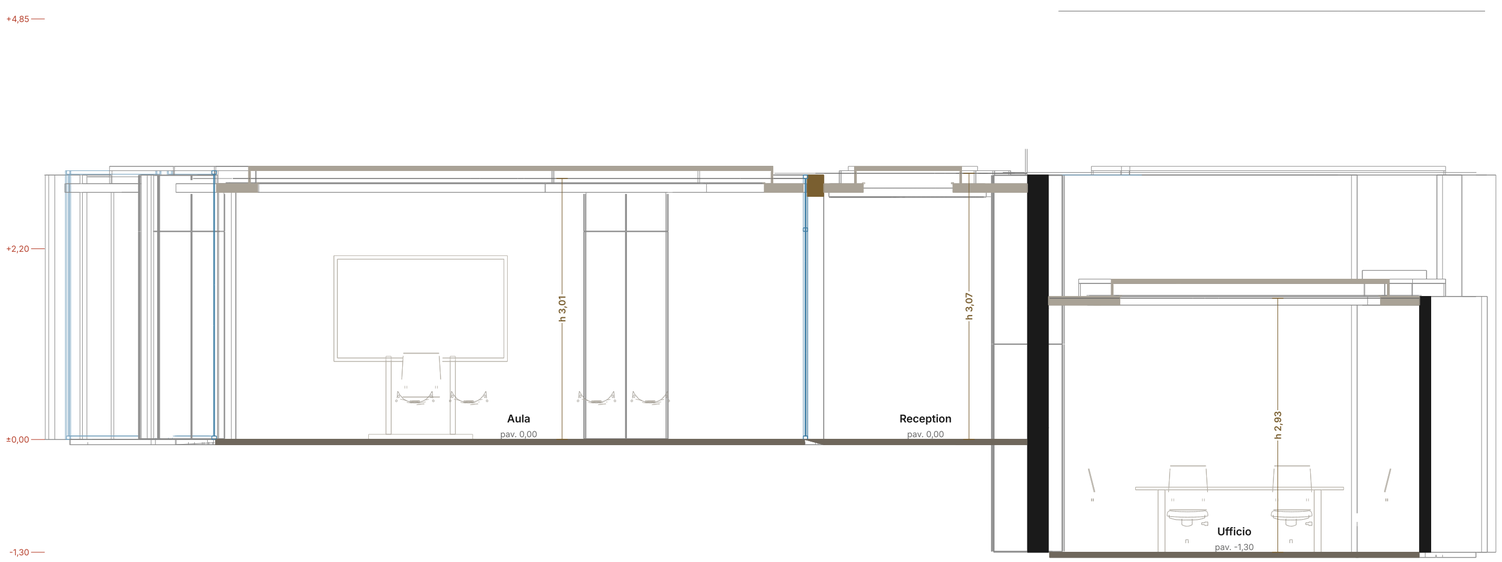

FUTURA
FORMAZIONE • LAVORO

TAVOLA S02

Sezioni B e D

Dal modello 3D aggiornato
Viste oltre il taglio
senza linee nascoste

LEGENDA

- Murature tagliate
- Murature nuove
- Pilastri
- Pavimenti e solaio
- Controsoffitti
- Vetro tagliato
- Vista oltre il taglio
- Arredi in vista
- Altezze nette (m)
- Quote di riferimento

SCALA 1:50 SU FOGLIO A2

0 — 2 m

VISIO Studio · Michelessi Corporation Srl
Bozza del 7 novembre 2026