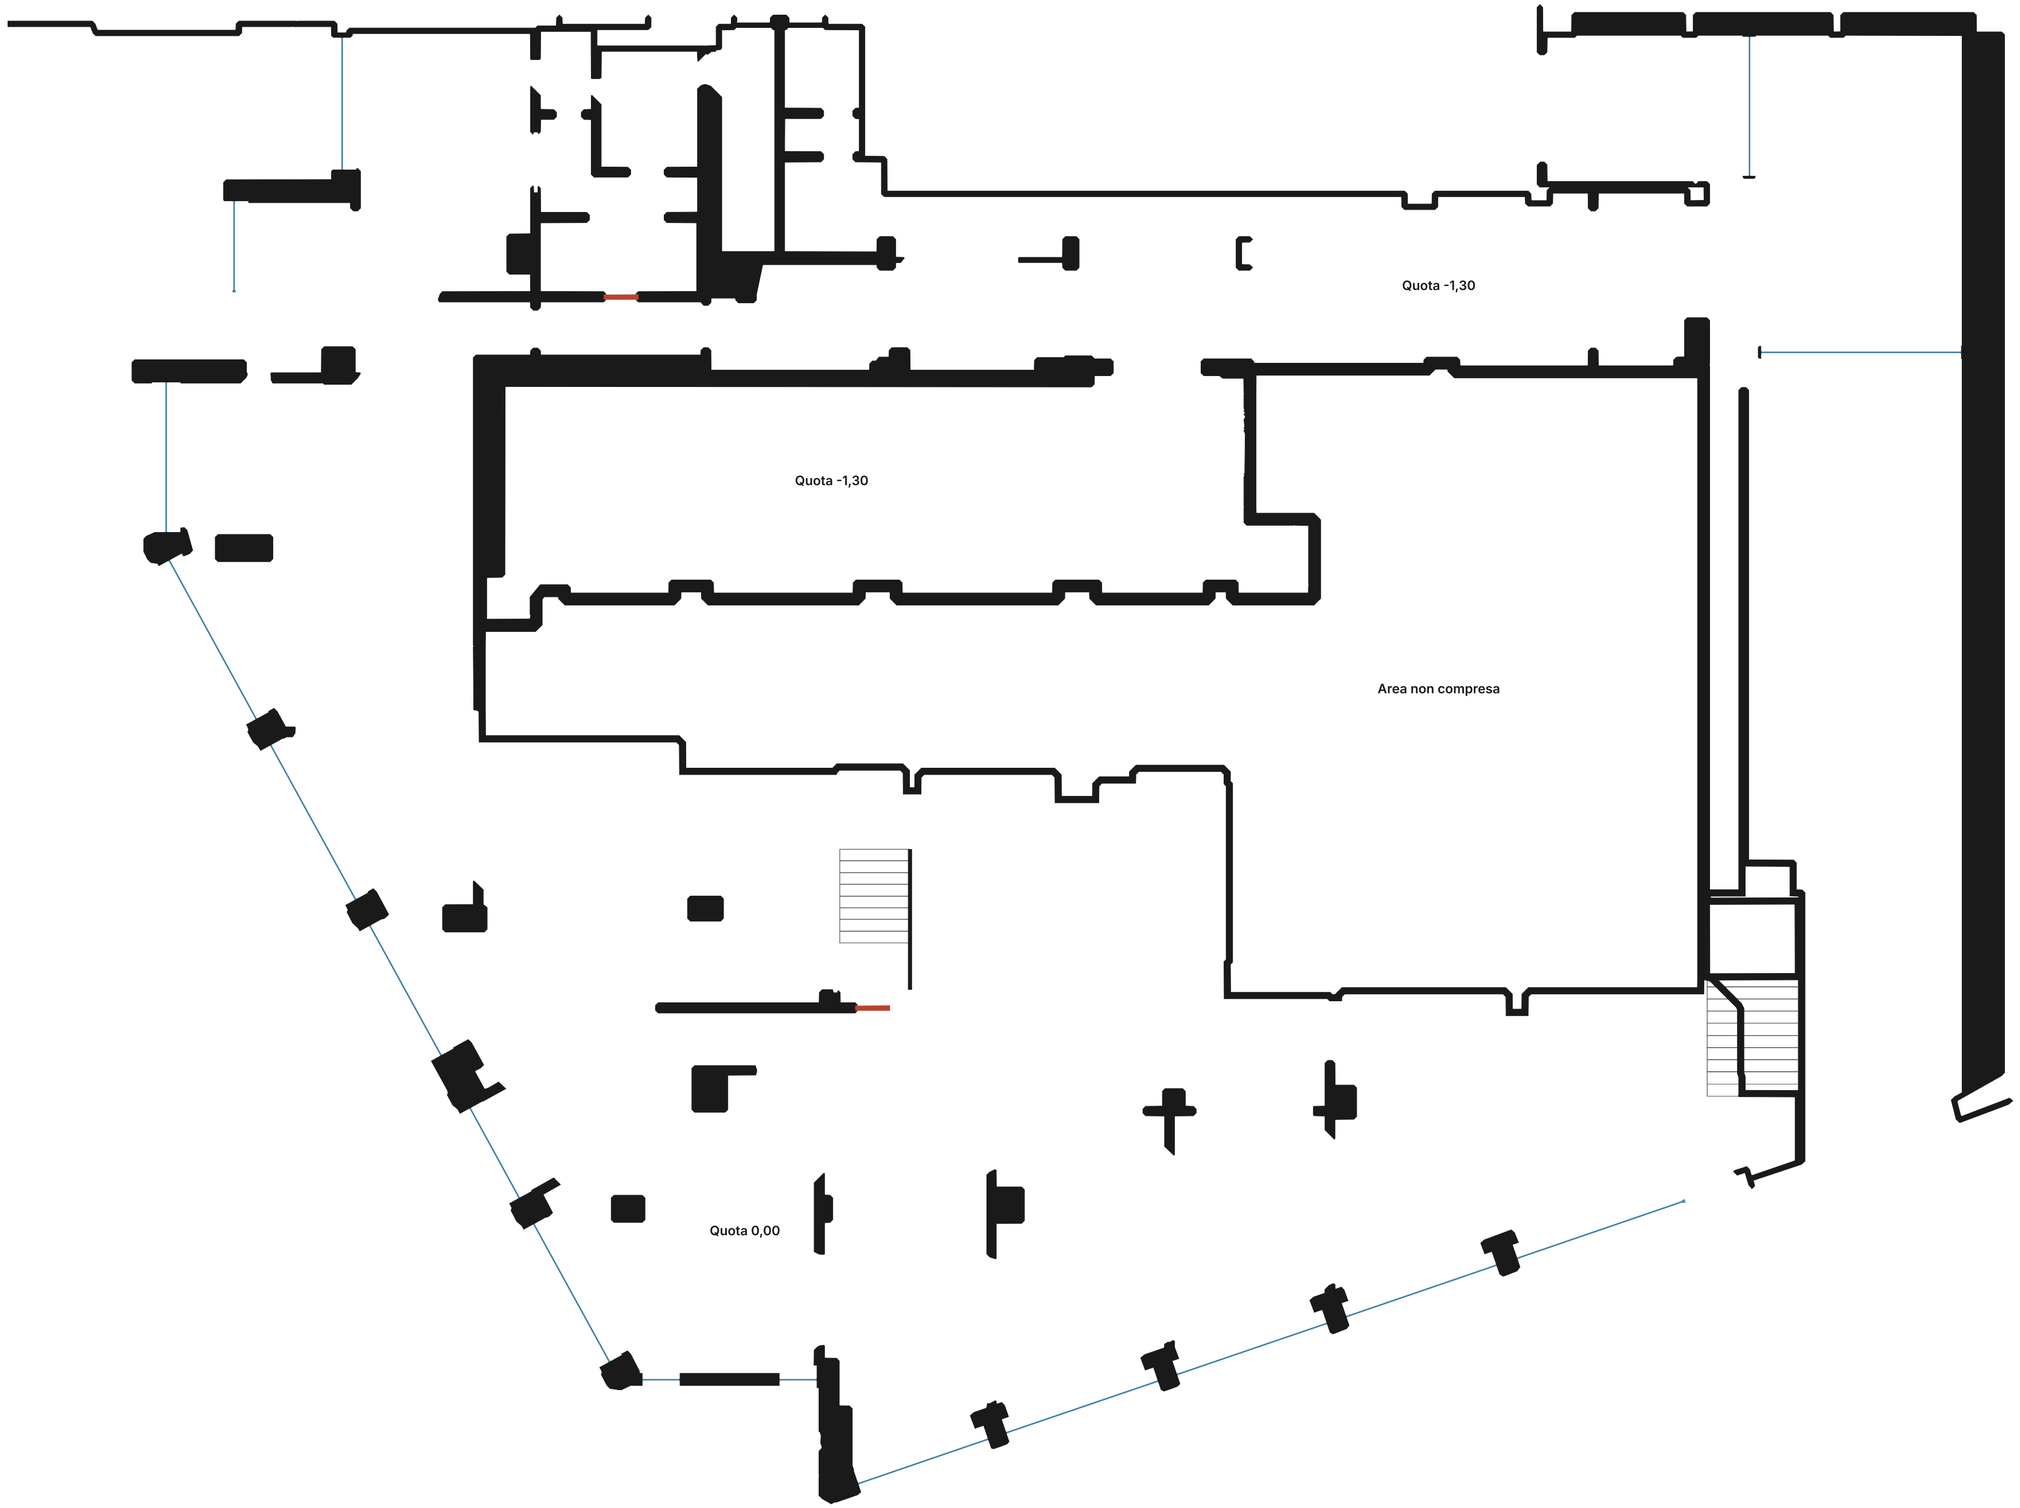


FUTURA
FORMAZIONE • LAVORO

Ante operam

Stato di fatto
dal rilievo 3D e dalla
planimetria EPT Rev01
Taglio a +1,00

LEGENDA

- Murature esistenti
- Da demolire
- Vetrine esistenti
- Scale

SCALA 1:100 SU FOGLIO A2

0 — 5 m

VISIO

VISIO Studio · Michelessi Corporation Srl
Bozza del 9 novembre 2026



FUTURA
FORMAZIONE • LAVORO

Post operam

Progetto dal modello 3D aggiornato
Taglio a +1,00


LEGENDA

- Murature esistenti
- Murature nuove e bancone
- Pilastri rivestiti
- Pareti vetrate e vetrine
- Scale
- Arredi e sanitari
- Soppalco sopra il taglio
- Tracce delle sezioni

SCALA 1:100 SU FOGLIO A2

0 — 5 m

VISIO Studio · Michelessi Corporation Srl
Bozza del 9 novembre 2026

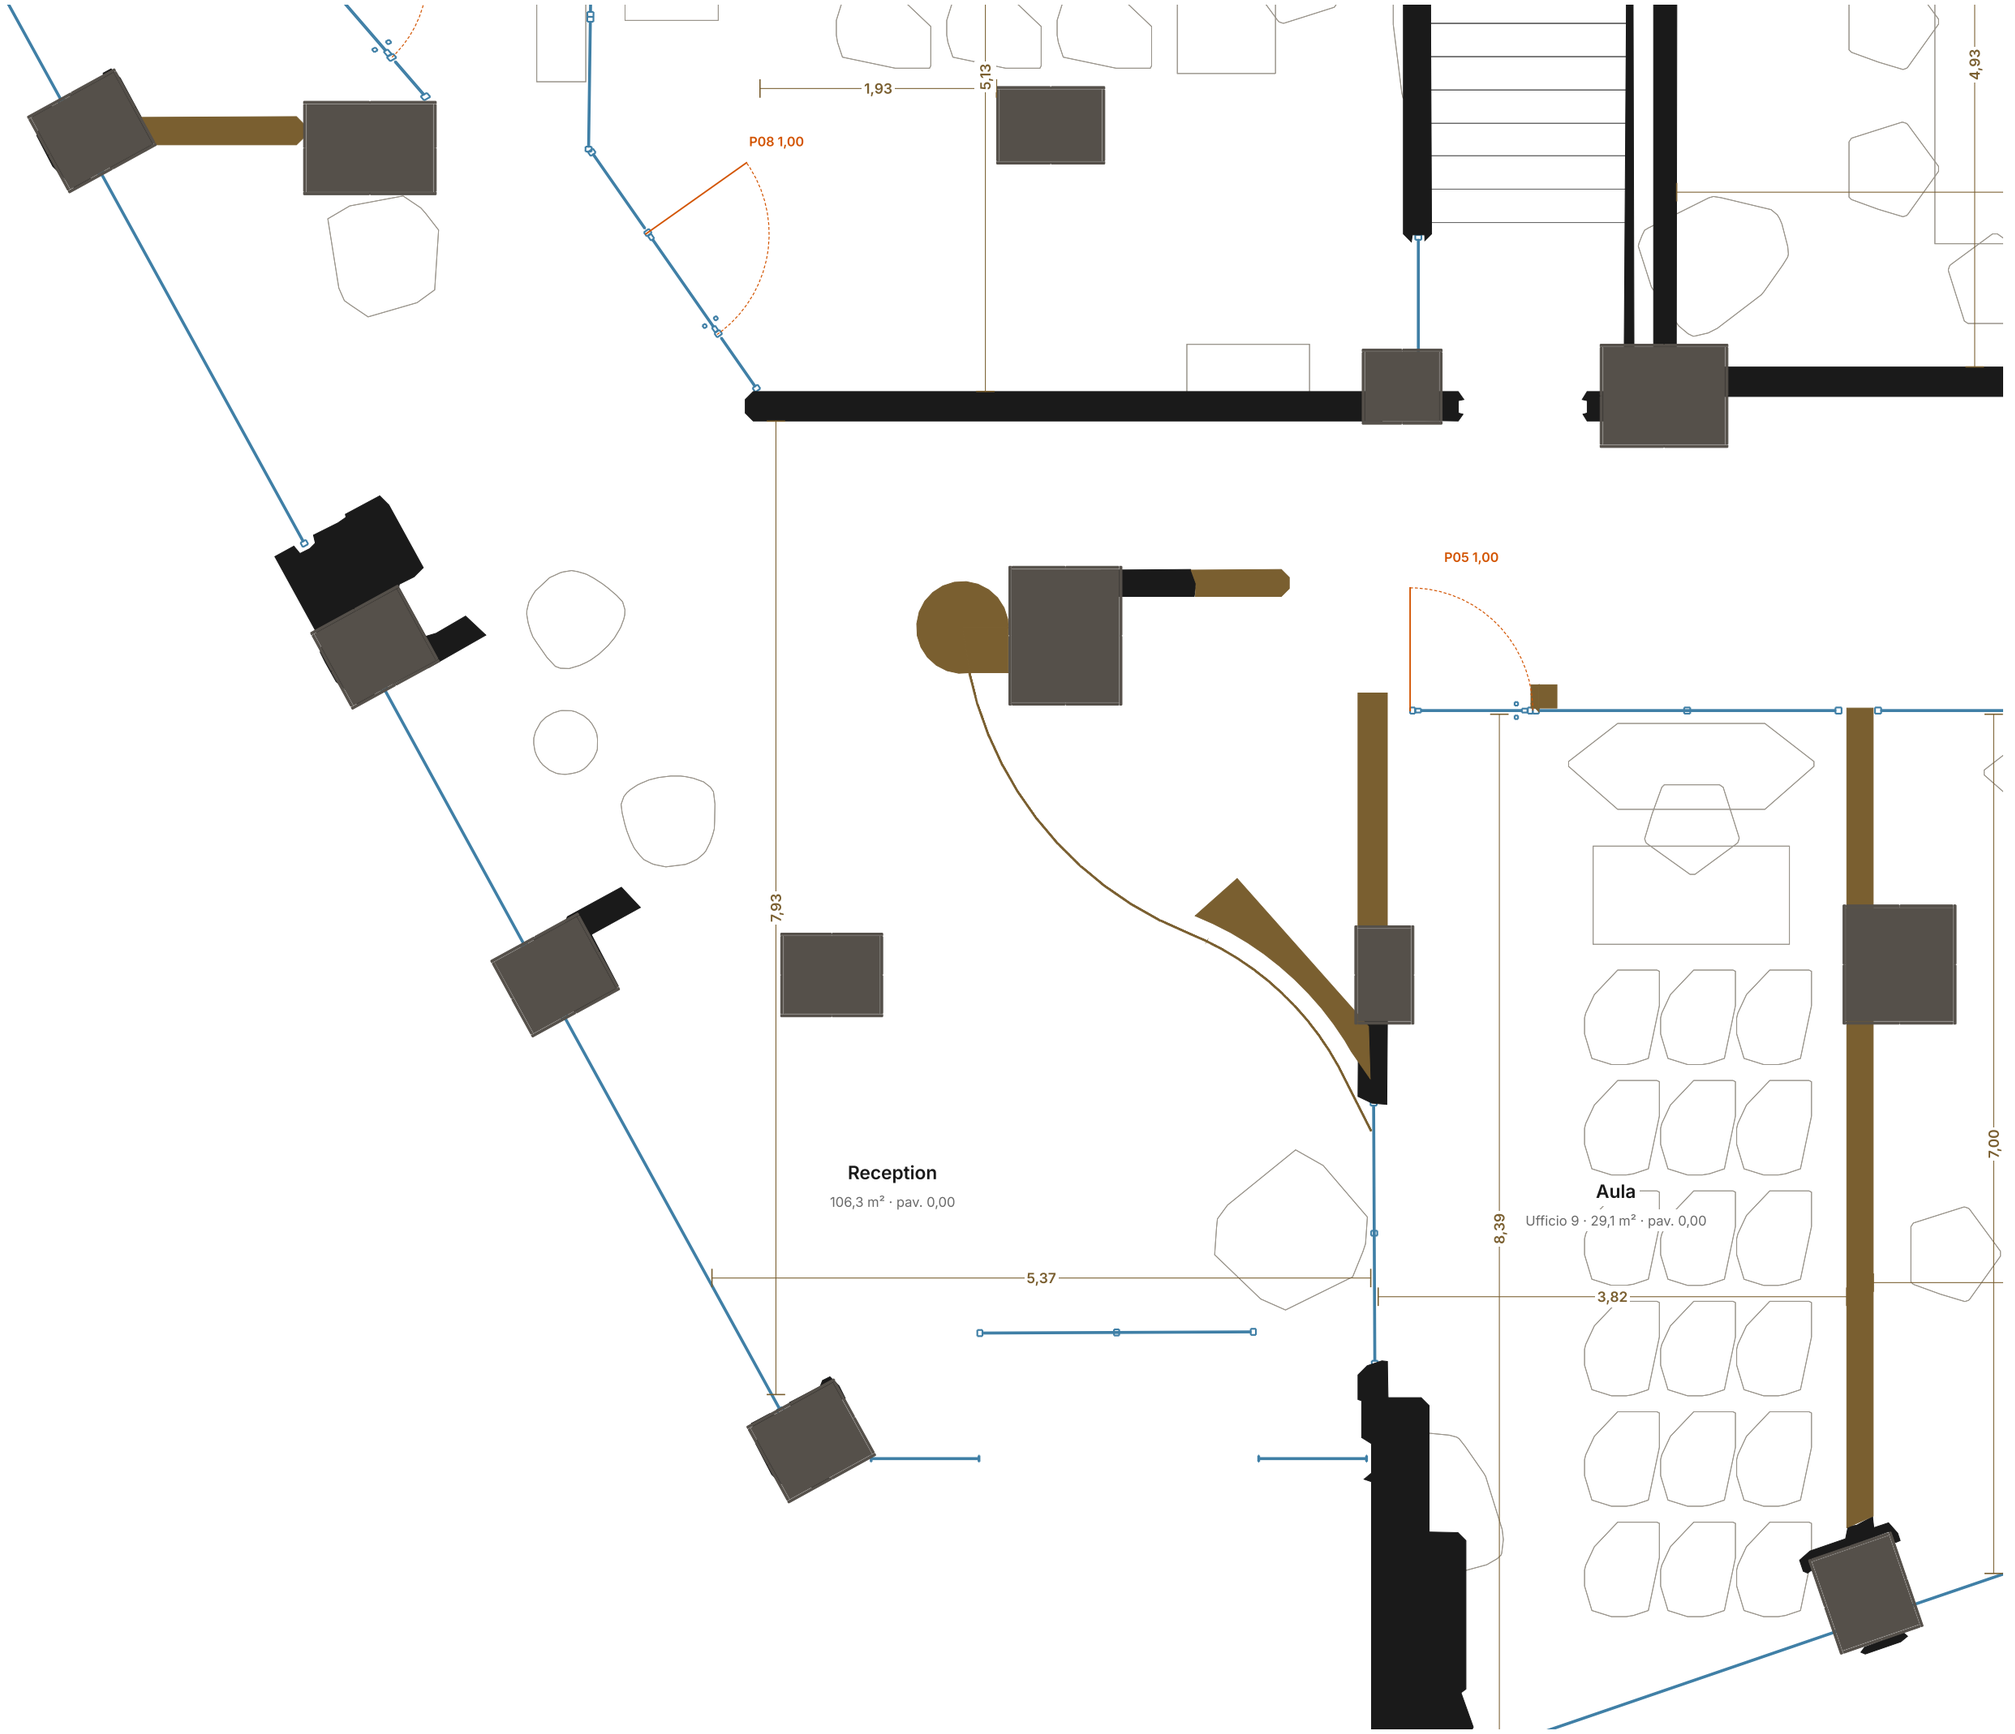

FUTURA
FORMAZIONE • LAVORO

TAVOLA D01

Reception

Ingresso e bancone

LEGENDA

- Murature esistenti
- Murature nuove
- Pilastri
- Vetrate e vetrine
- Scale
- Arredi e sanitari
- Misure nette (m)

SCALA 1:50 SU FOGLIO A3

0 — 2 m


VISIO Studio · Michelessi Corporation Srl
Bozza del 9 novembre 2026

FUTURA
FORMAZIONE • LAVORO

TAVOLA D02

Aule 9, 10 e 11

Lato sud

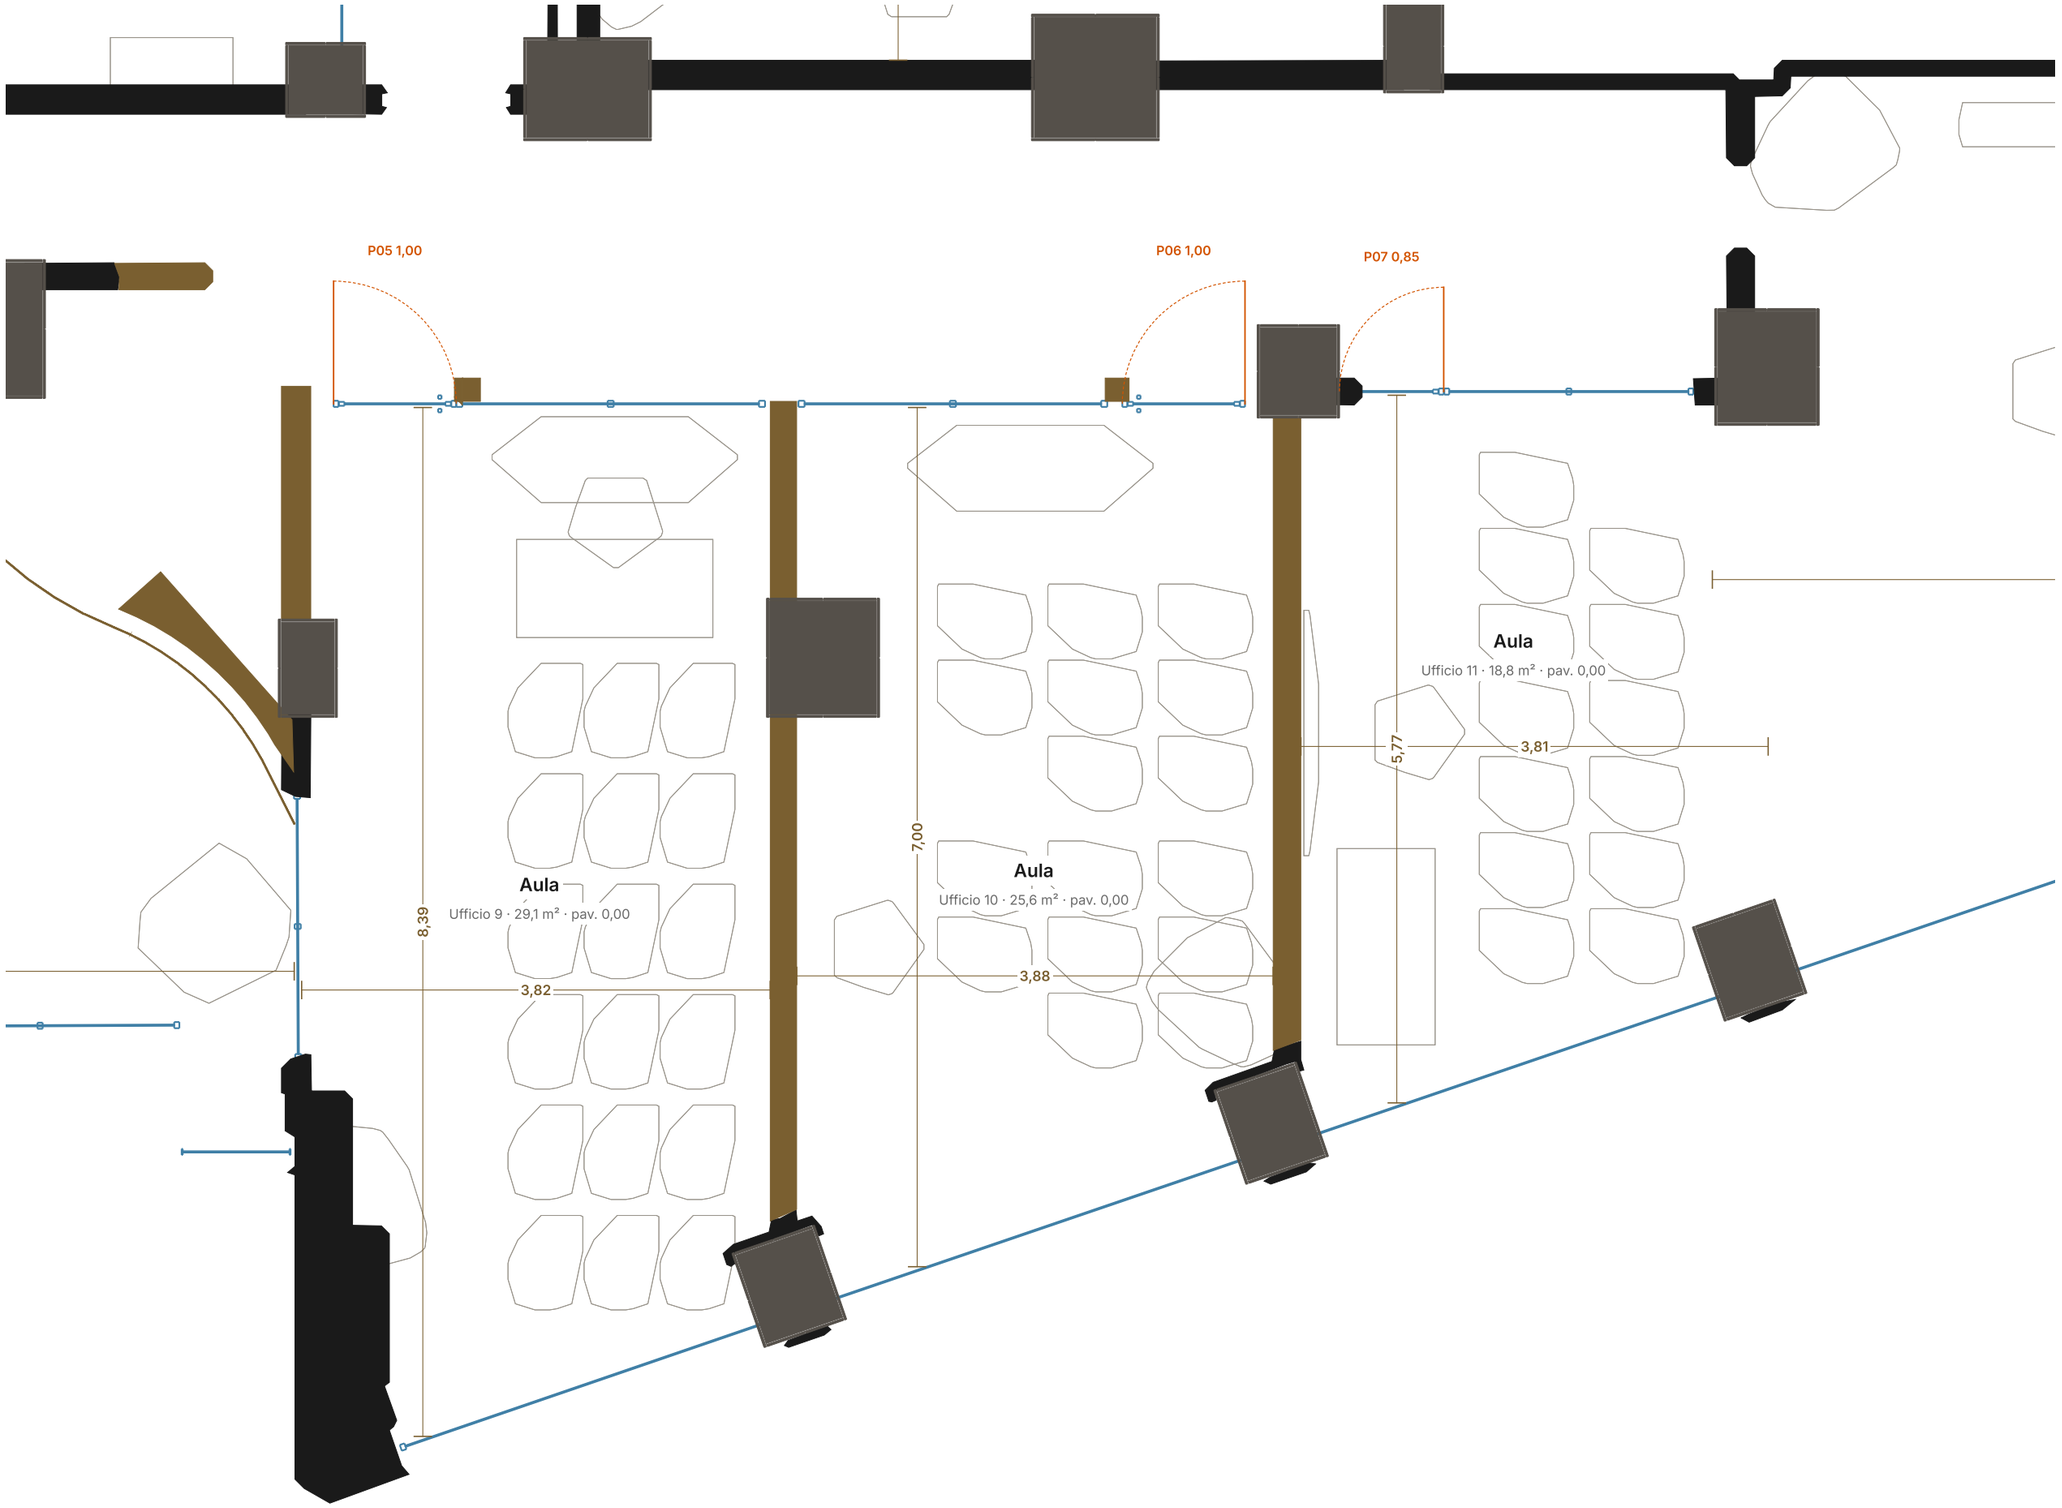


LEGENDA

- Murature esistenti
- Murature nuove
- Pilastri
- Vetrate e vetrine
- Scale
- Arredi e sanitari
- Misure nette (m)

SCALA 1:50 SU FOGLIO A3

0 — 2 m

VISIO Studio · Michelessi Corporation Srl
Bozza del 9 novembre 2026

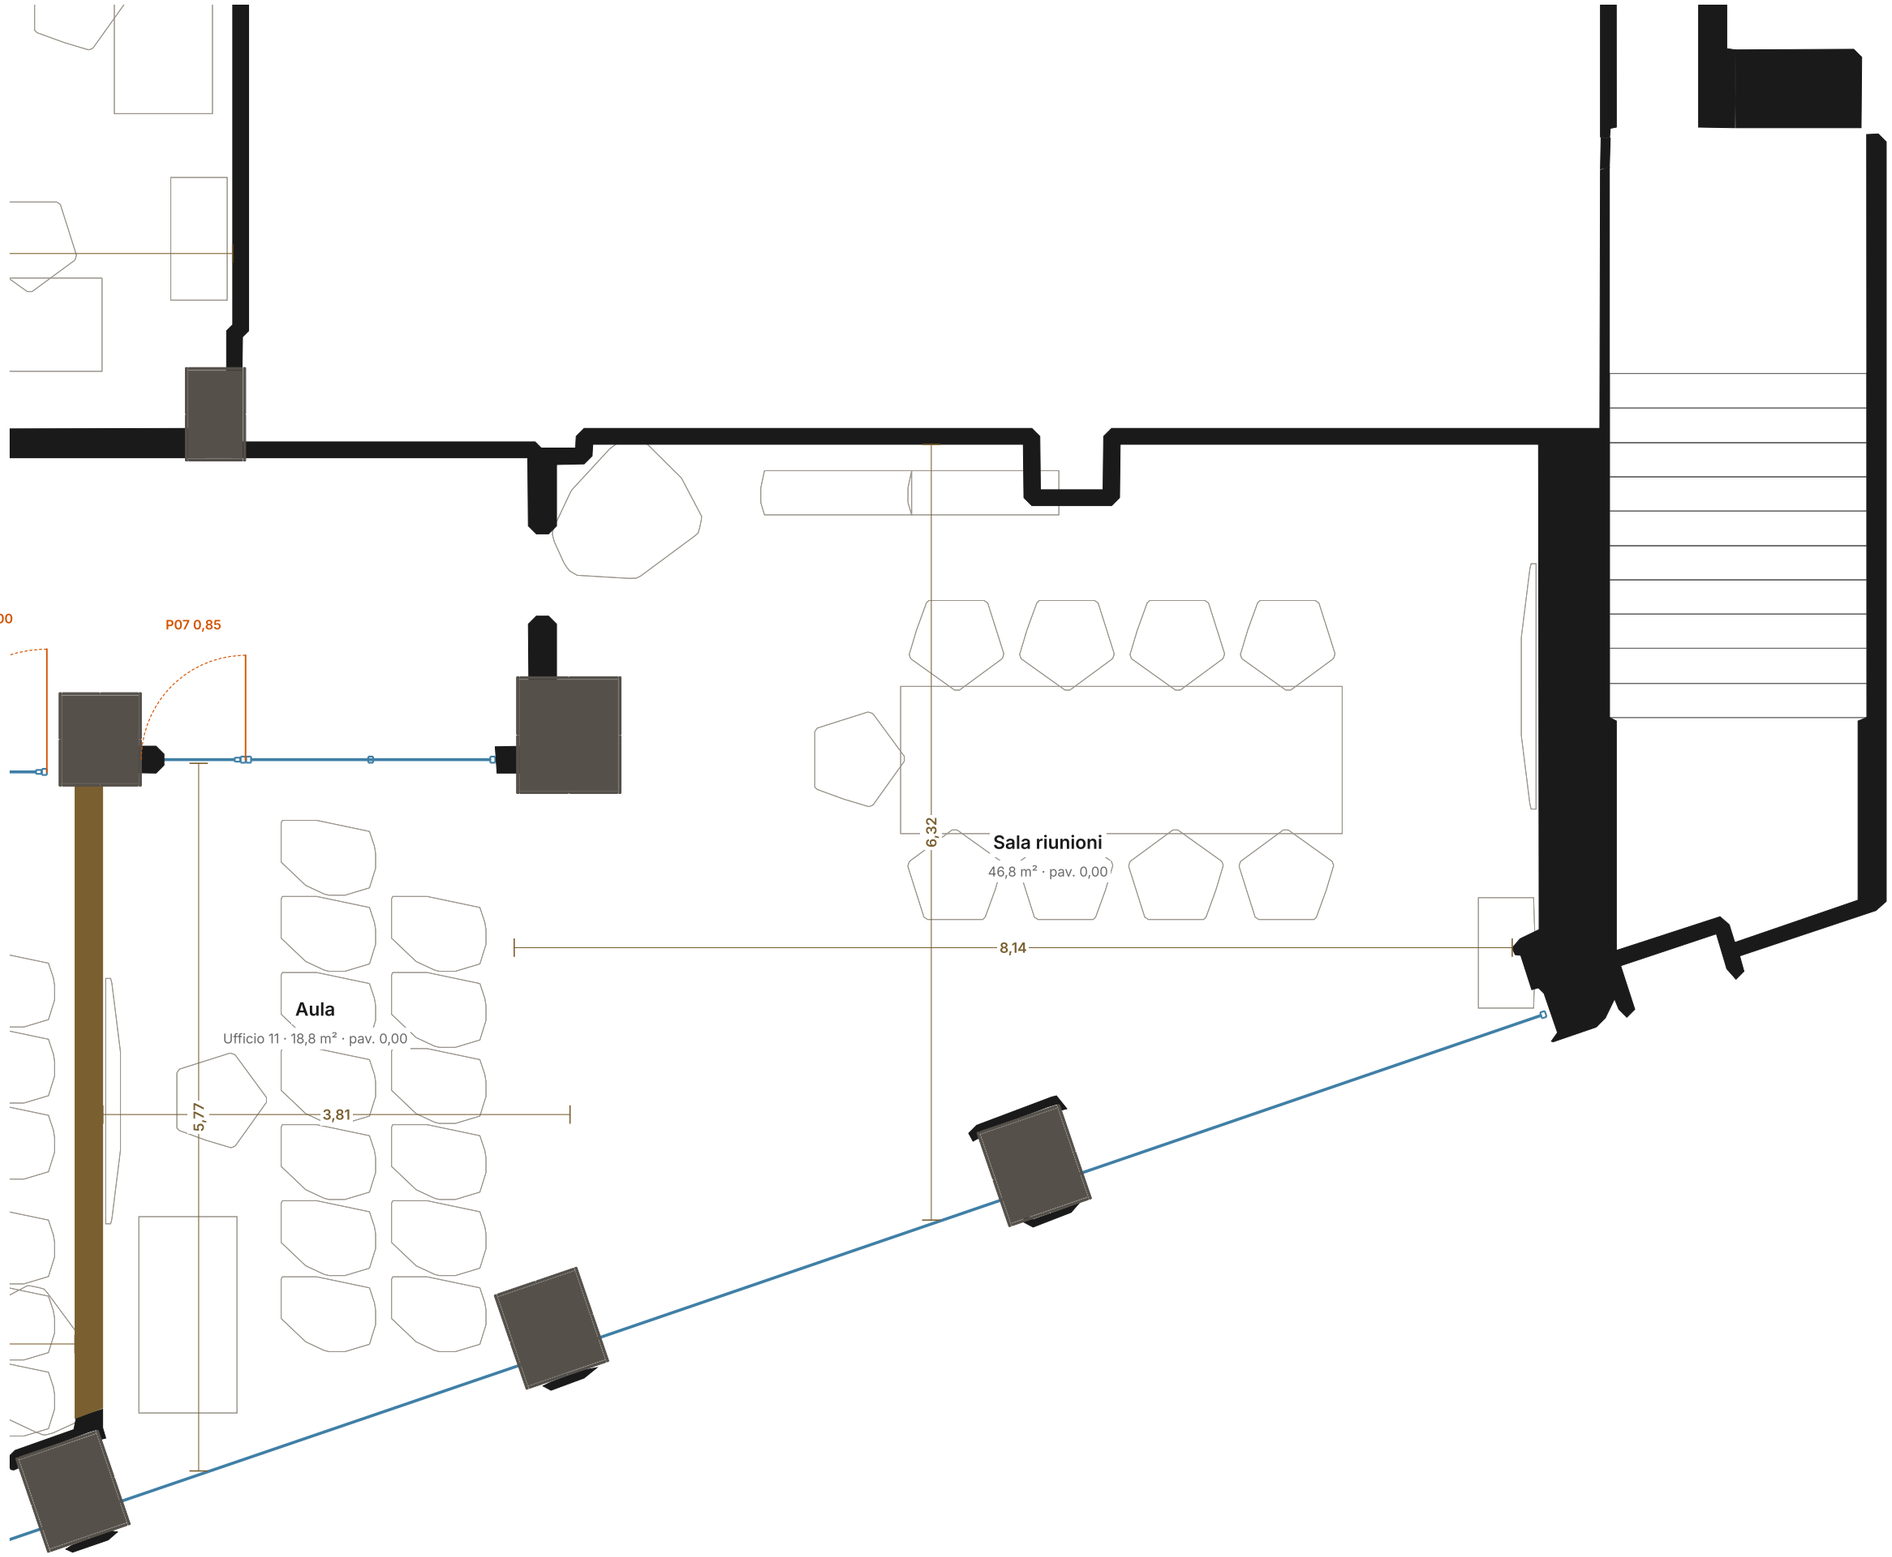

FUTURA
FORMAZIONE • LAVORO

TAVOLA D03

Sala riunioni

E scala di servizio

LEGENDA


- Murature esistenti
- Murature nuove
- Pilastri
- Vetrate e vetrine
- Scale
- Arredi e sanitari
- Misure nette (m)

SCALA 1:50 SU FOGLIO A3

0 — 2 m

VISIO

VISIO Studio · Michelessi Corporation Srl
Bozza del 9 novembre 2026

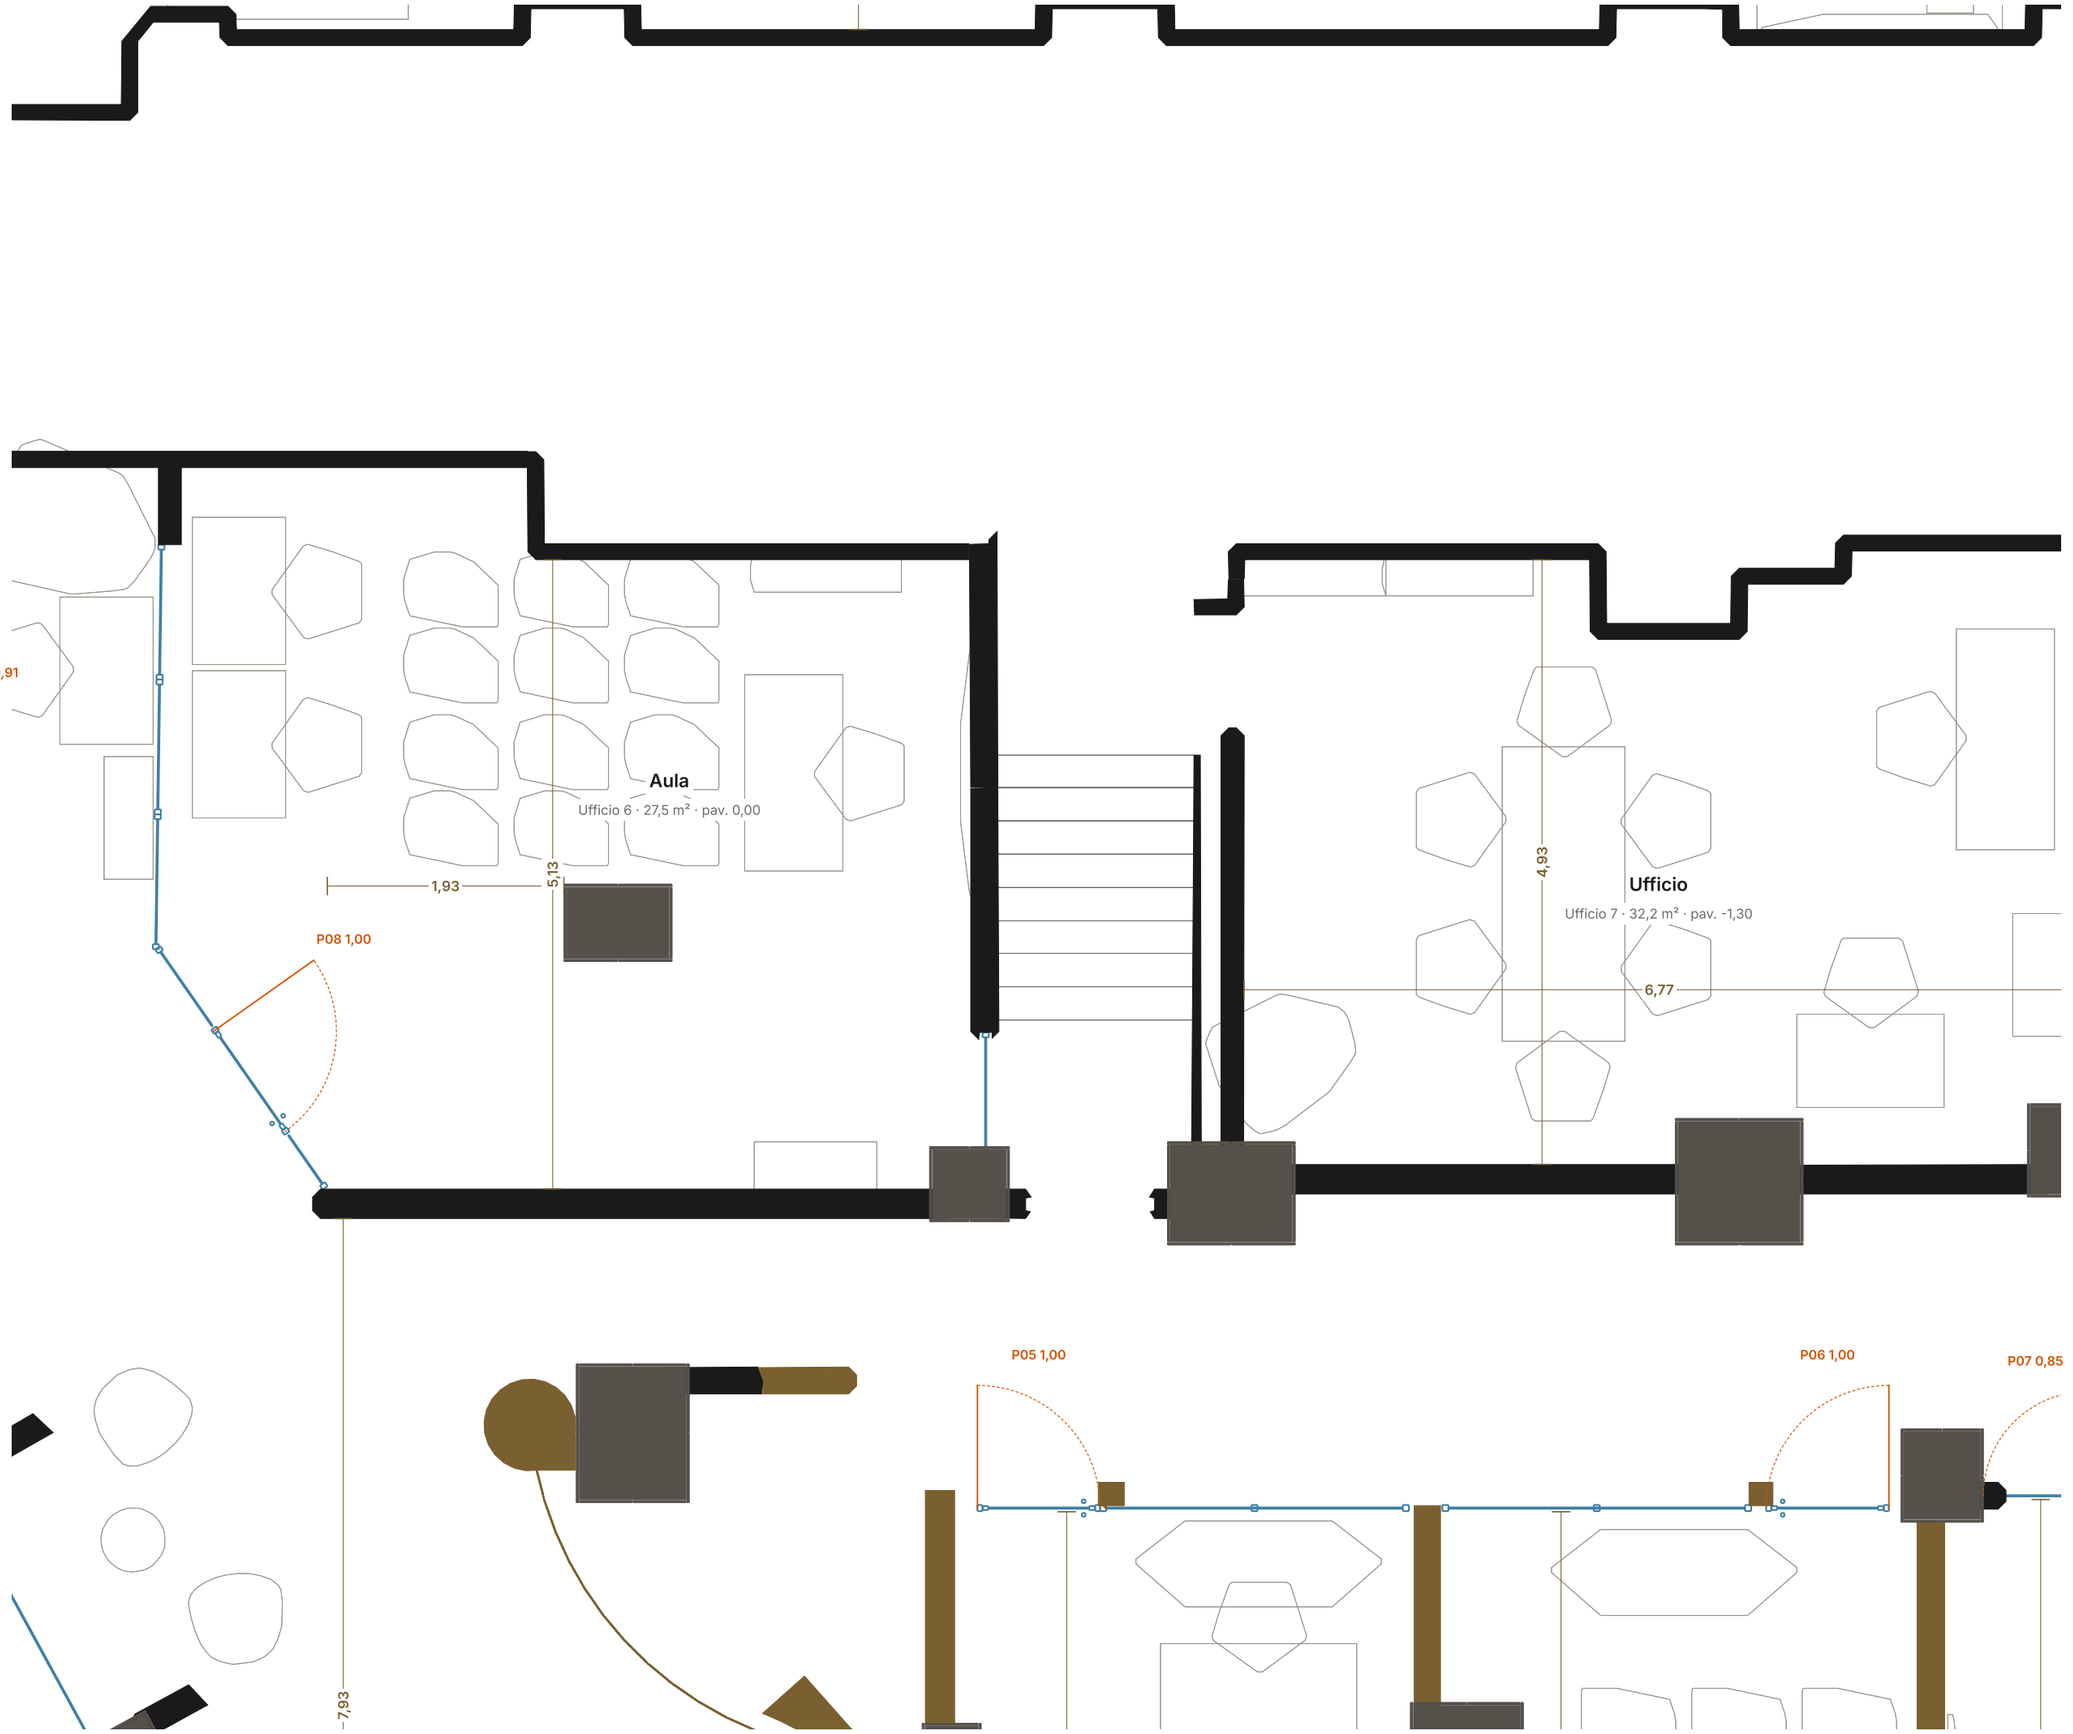

FUTURA
FORMAZIONE • LAVORO

TAVOLA D04

Aula 6 e Ufficio 7

Salto di quota 0,00 / -1,30

LEGENDA


- Murature esistenti
- Murature nuove
- Pilastri
- Vetrate e vetrine
- Scale
- Arredi e sanitari
- Misure nette (m)

SCALA 1:50 SU FOGLIO A3

0 2 m

VISIO

VISIO Studio · Michelessi Corporation Srl
Bozza del 9 novembre 2026

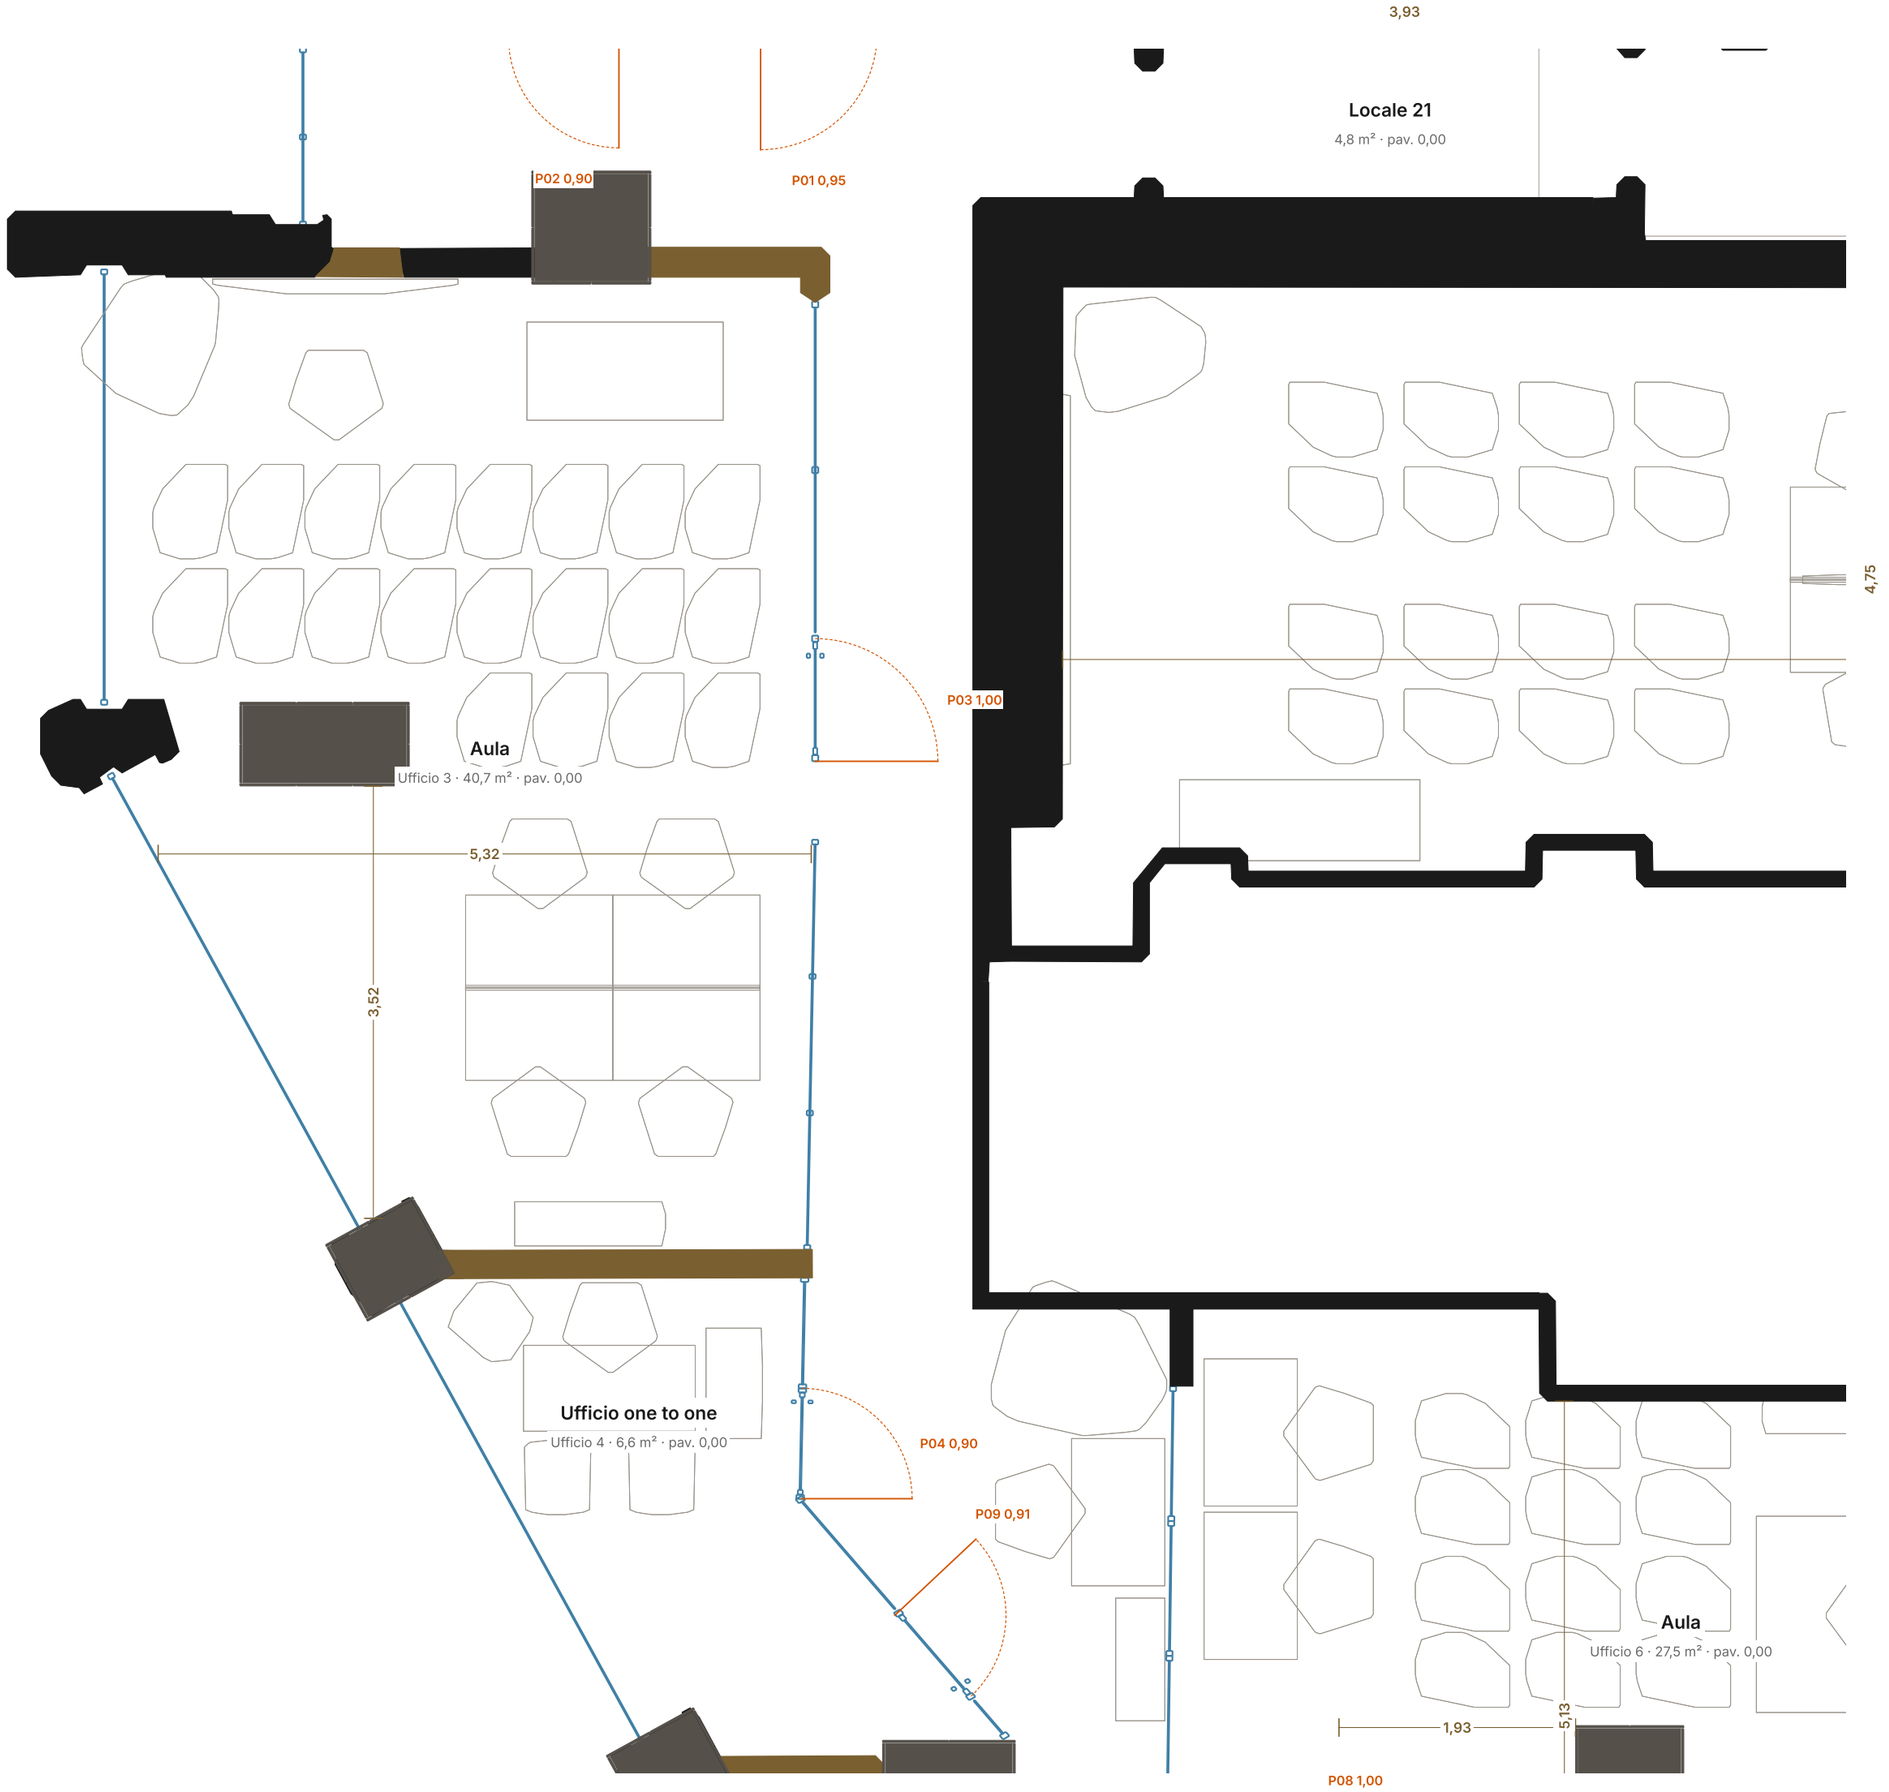

FUTURA
FORMAZIONE • LAVORO

TAVOLA D05

Aula 3
e one to one

Uffici 3 e 4

LEGENDA

- Murature esistenti
- Murature nuove
- Pilastri
- Vetrate e vetrine
- Scale
- Arredi e sanitari
- Misure nette (m)

SCALA 1:50 SU FOGLIO A3

0 — 2 m

VISIO Studio · Michelessi Corporation Srl
Bozza del 9 novembre 2026

FUTURA
FORMAZIONE • LAVORO

TAVOLA D06

Aula 1
e one to one

Uffici 1 e 2



LEGENDA

- Murature esistenti
- Murature nuove
- Pilastri
- Vetrate e vetrine
- Scale
- Arredi e sanitari
- Misure nette (m)

SCALA 1:50 SU FOGLIO A3

0 — 2 m

VISIO Studio · Michelessi Corporation Srl
Bozza del 9 novembre 2026



FUTURA
FORMAZIONE • LAVORO

TAVOLA D07

Bagni e servizi

Quote 0,00 e -1,30

LEGENDA

- Murature esistenti
- Murature nuove
- Pilastri
- Vetrate e vetrine
- Scale
- Arredi e sanitari
- Misure nette (m)

SCALA 1:50 SU FOGLIO A3

0 — 2 m

VISIO Studio · Michelessi Corporation Srl
Bozza del 9 novembre 2026

FUTURA
FORMAZIONE • LAVORO

TAVOLA D08

Laboratorio

Lezione, PC, lavoro e stampa 3D · quota -1,30

LEGENDA

- Murature esistenti
- Murature nuove
- Pilastri
- Vetrate e vetrine
- Scale
- Arredi e sanitari
- Misure nette (m)

SCALA 1:75 SU FOGLIO A3

0 — 3 m

VISIO Studio · Michelessi Corporation Srl
Bozza del 9 novembre 2026

Aula
Ufficio 1 · 24,8 m² · pav. 0,00
3,92
5

WC
5,9 m² · pav. 0,00
2,66
2,22

Locale 29
6,2 m² · pav. 0,00

WC
3,2 m² · pav. -1,30

Locale 25
1,5 m² · pav. -1,30

Locale 18
4,8 m² · pav. -1,30
2,06
2,12

Locale 28
5,7 m² · pav. -1,30
1,40
3,79

Locale 17
8,2 m² · pav. 0,00
1,59
3,93

Locale 21
4,8 m² · pav. 0,00

Corridoio
pav. -1,30
3,84
13,74

P01 0,95

0,90

Laboratorio
lezione, PC e stampa 3D · pav. -1,30
15
17,04

P03 1,00

icio one to one
o 4 · 6,6 m² · pav. 0,00


P04 0,90

P09 0,91

P08 1,00

Aula
Ufficio 6 · 27,5 m² · pav. 0,00
1,93
5,13

Ufficio
Ufficio 7 · 32,2 m² · pav. -1,30
4,93
6,77

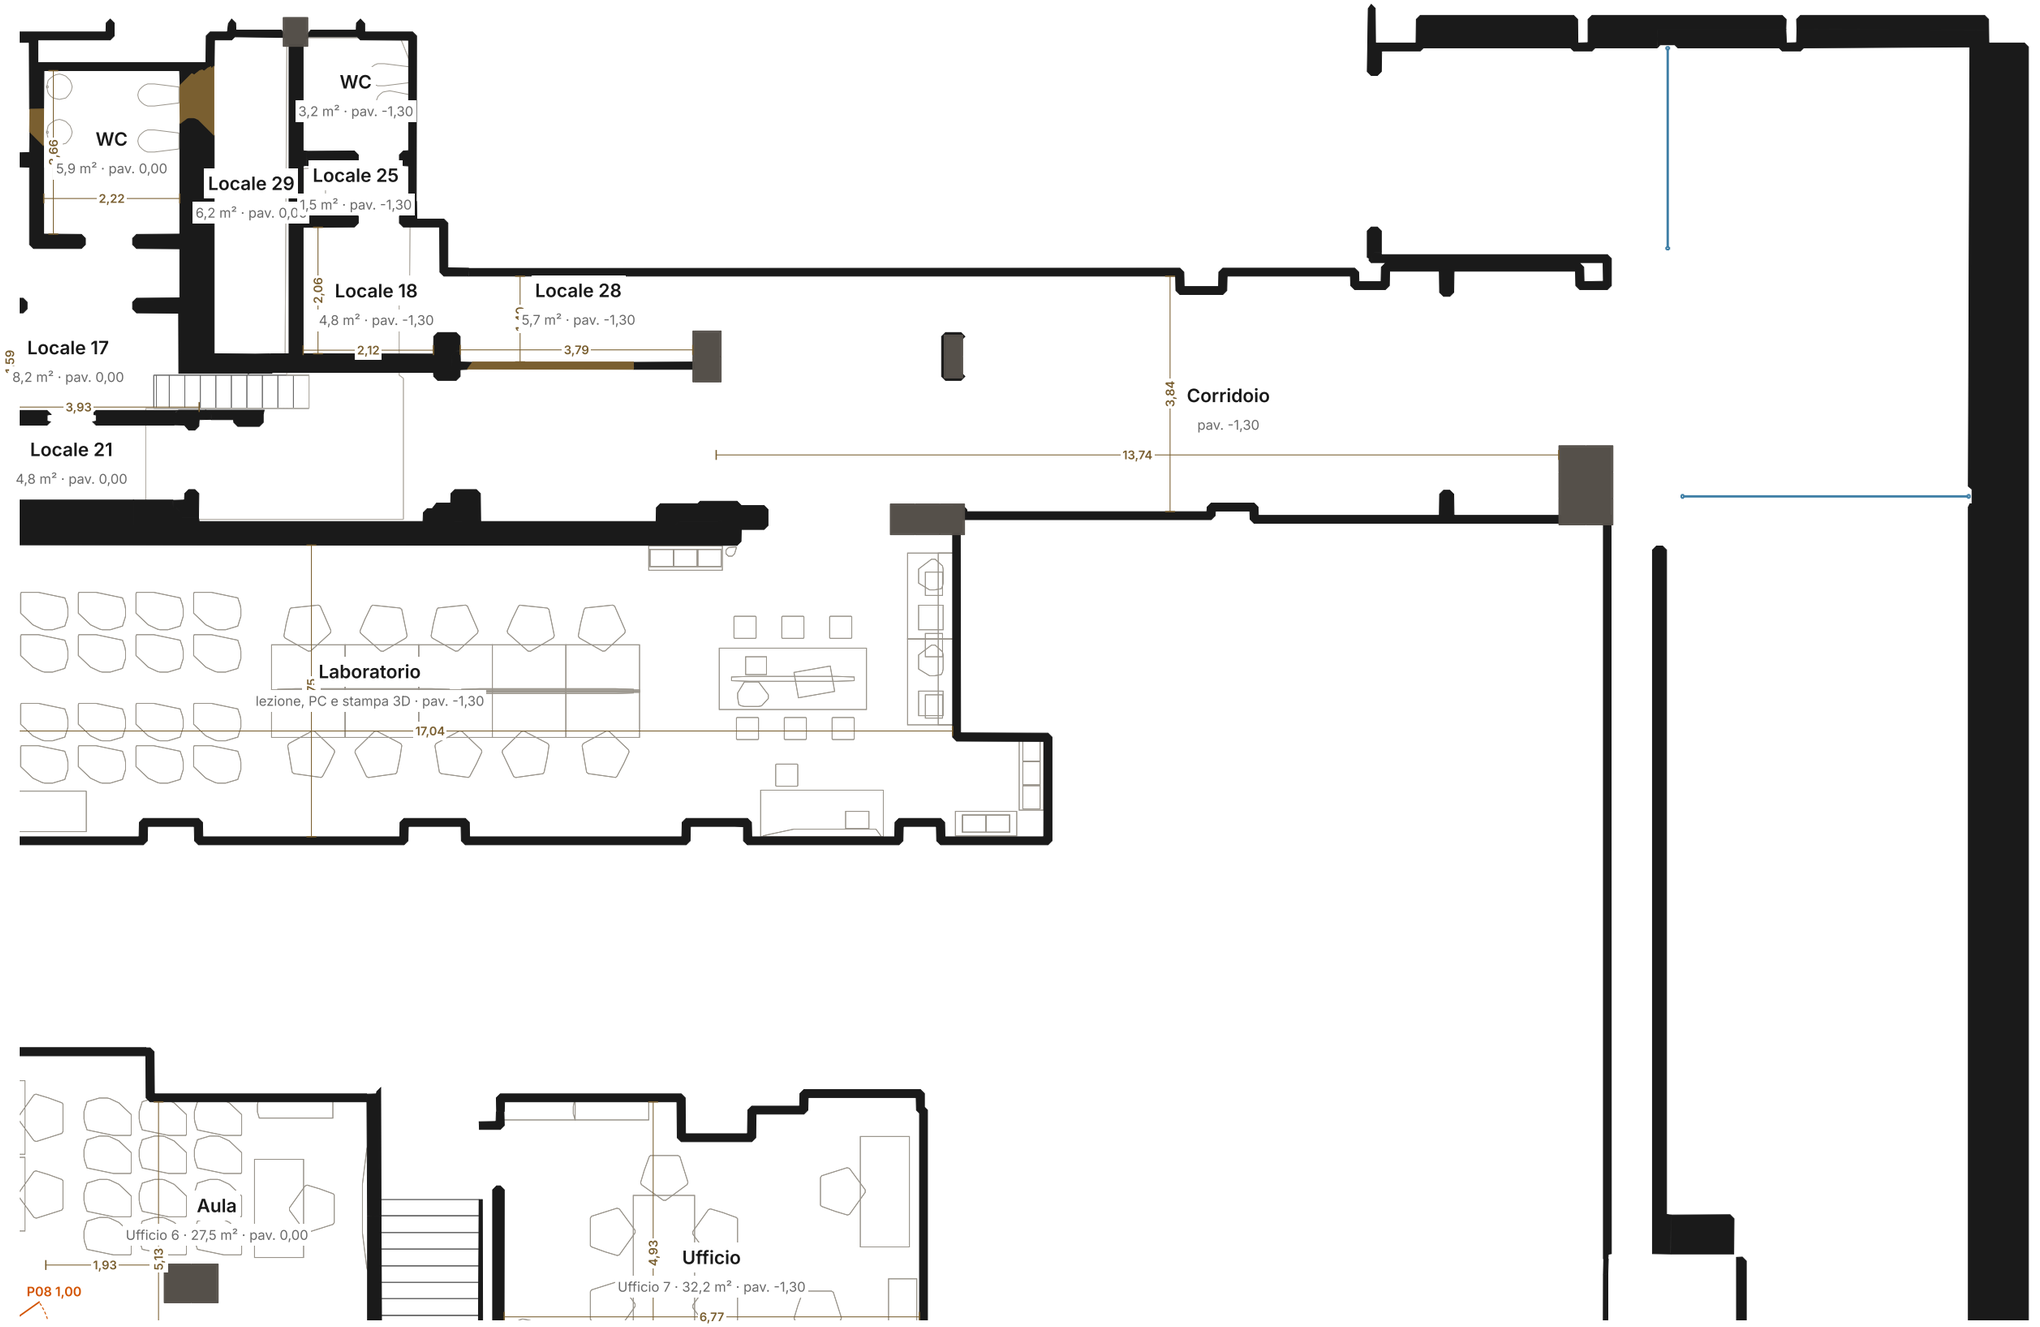

FUTURA
FORMAZIONE • LAVORO

TAVOLA D09

Corridoio -1,30

Rampa e corridoio


LEGENDA

- Murature esistenti
- Murature nuove
- Pilastri
- Vetrate e vetrine
- Scale
- Arredi e sanitari
- Misure nette (m)

SCALA 1:100 SU FOGLIO A3

0 — 5 m

VISIO Studio · Michelessi Corporation Srl
Bozza del 9 novembre 2026

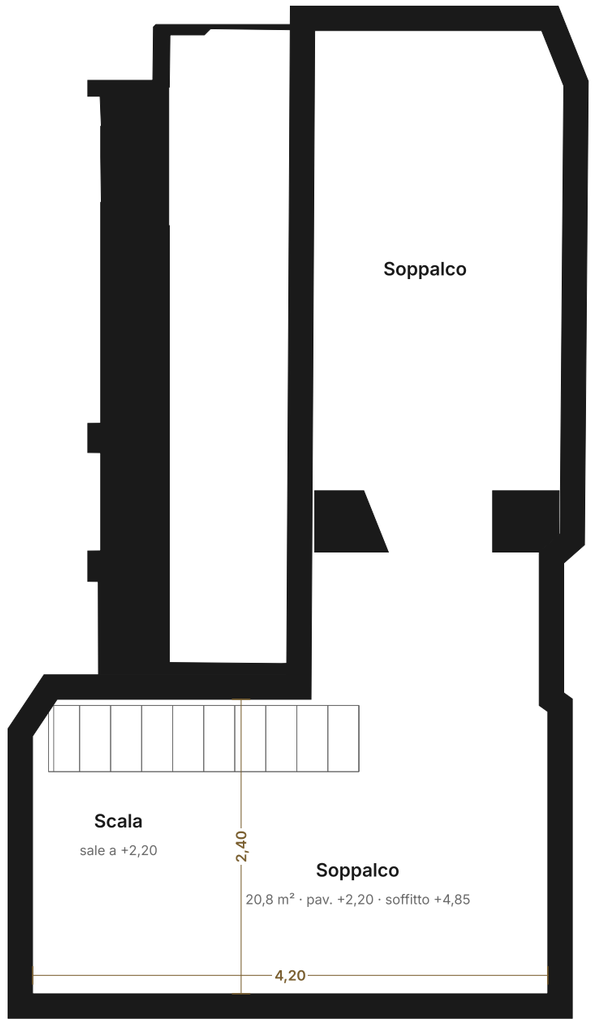

FUTURA
FORMAZIONE • LAVORO

TAVOLA D10

Soppalco

Taglio a +3,50

LEGENDA

- Murature esistenti
- Murature nuove
- Pilastri
- Vetrate e vetrine
- Scale
- Arredi e sanitari
- Misure nette (m)


SCALA 1:50 SU FOGLIO A3

0 — 2 m

VISIO Studio · Michelessi Corporation Srl
Bozza del 9 novembre 2026


Sezione A–A

Scala al soppalco, rampa e corridoio · 1:50

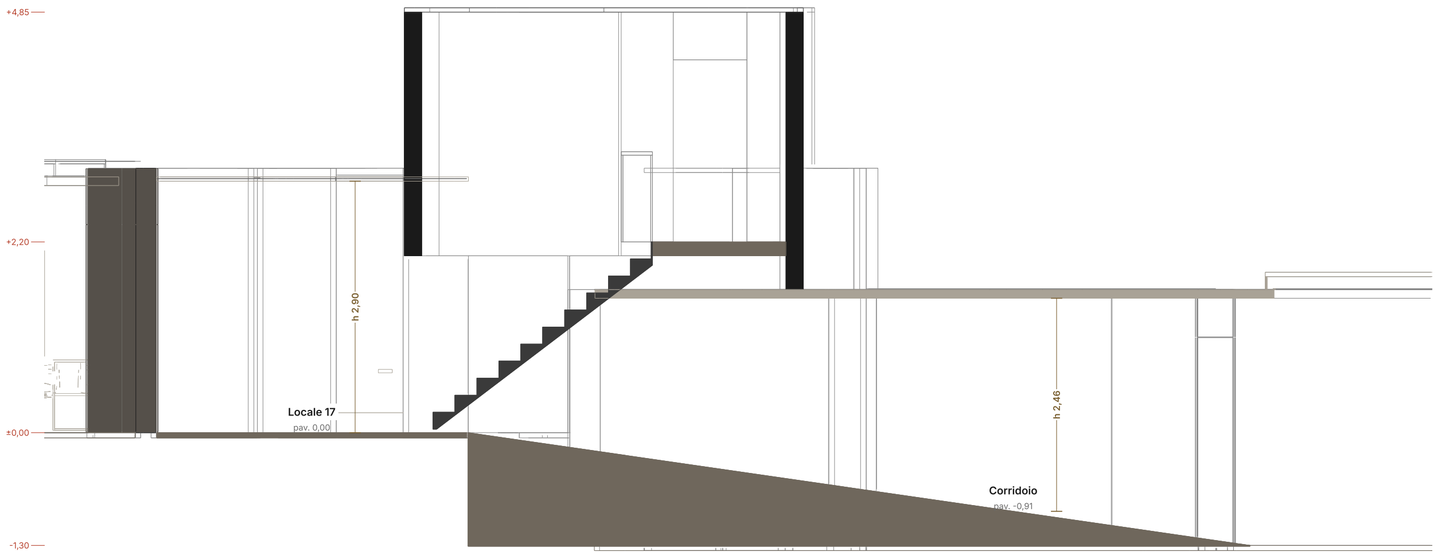

Sezione C–C

Salto di quota con la scala, Aula 6 e Ufficio 7 · 1:50

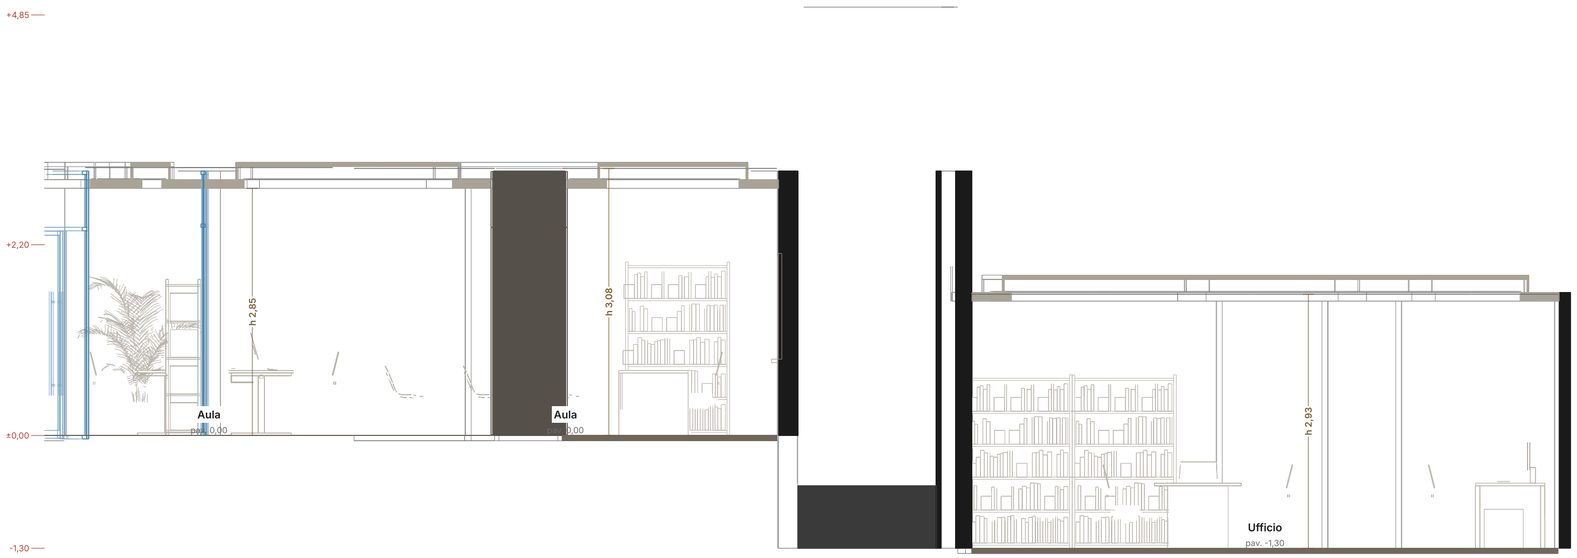

FUTURA
FORMAZIONE • LAVORO

TAVOLA S01

Sezioni A e C

Dal modello 3D aggiornato
Viste oltre il taglio
senza linee nascoste

LEGENDA

- Murature tagliate
- Murature nuove
- Pilastri
- Pavimenti e solaio
- Controsoffitti
- Vetro tagliato
- Vista oltre il taglio
- Arredi in vista
- Altezze nette (m)
- Quote di riferimento


SCALA 1:50 SU FOGLIO A2

0 2 m

VISIO Studio · Michelessi Corporation Srl
Bozza del 9 novembre 2026


Sezione B–B

Aula 6, laboratorio, corridoio, soppalco e bagni · 1:50

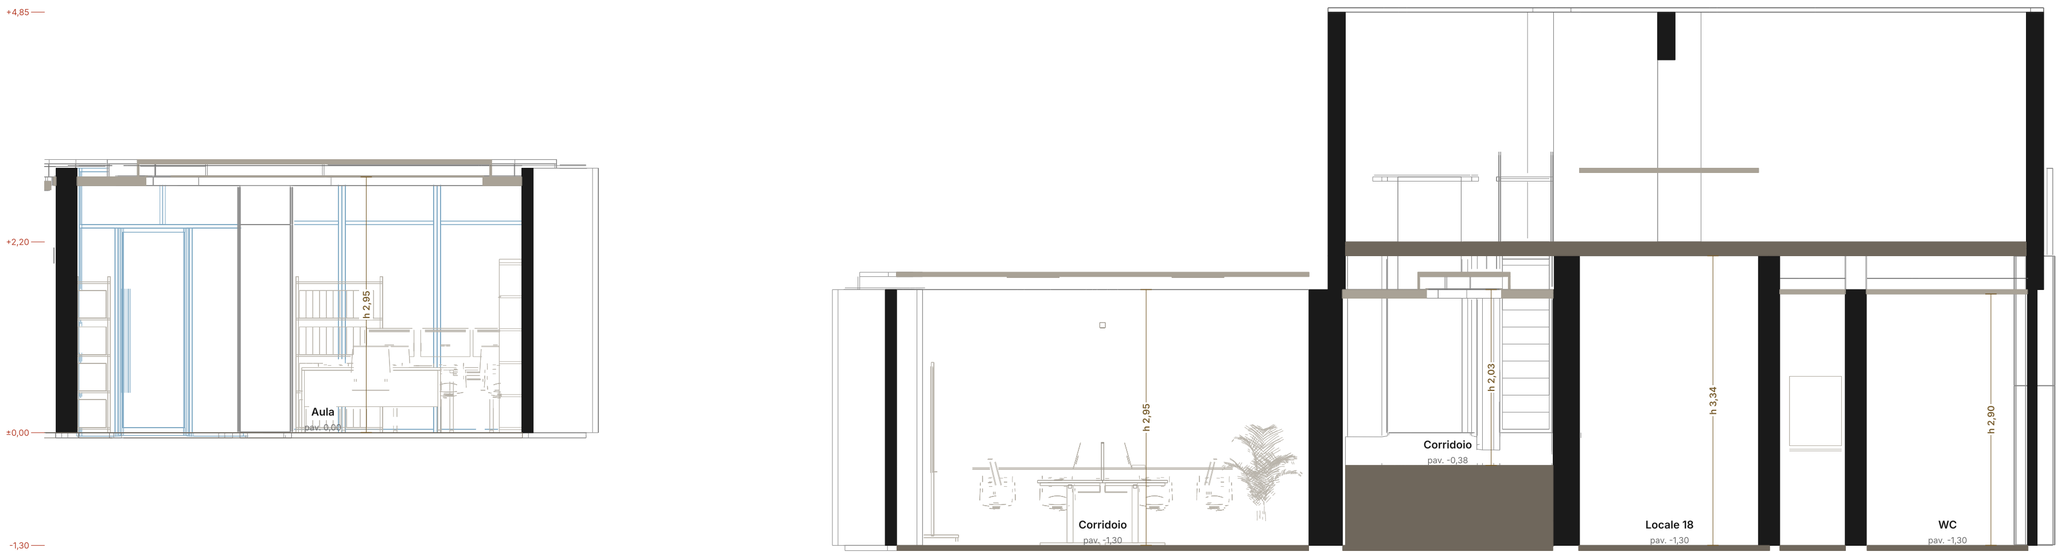

Sezione D–D

Vetrina, Aula 10, reception e Ufficio 7 · 1:50

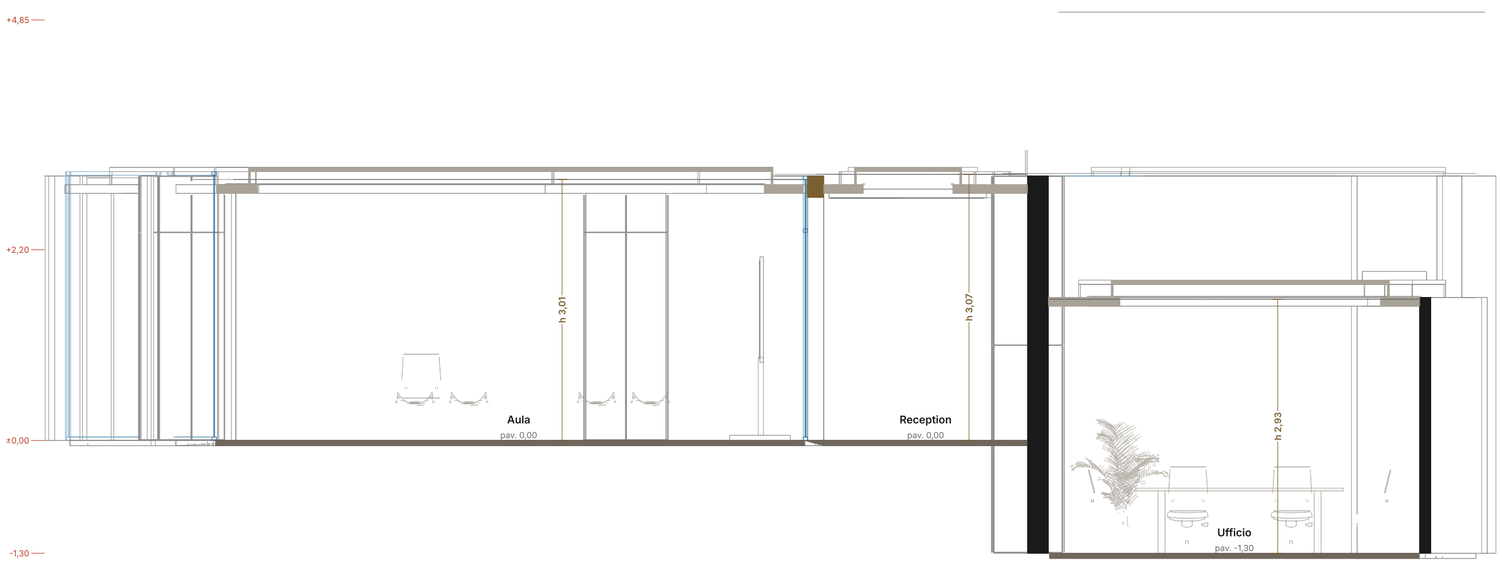

FUTURA
FORMAZIONE • LAVORO

TAVOLA S02

Sezioni B e D

Dal modello 3D aggiornato
Viste oltre il taglio
senza linee nascoste

LEGENDA

- Murature tagliate
- Murature nuove
- Pilastri
- Pavimenti e solaio
- Controsoffitti
- Vetro tagliato
- Vista oltre il taglio
- Arredi in vista
- Altezze nette (m)
- Quote di riferimento

SCALA 1:50 SU FOGLIO A2

0 — 2 m


VISIO Studio · Michelessi Corporation Srl
Bozza del 9 novembre 2026

Sezione F–F

Aula 3, corridoio, one to one e Aula 1 · 1:50



Chiave delle sezioni · 1:250

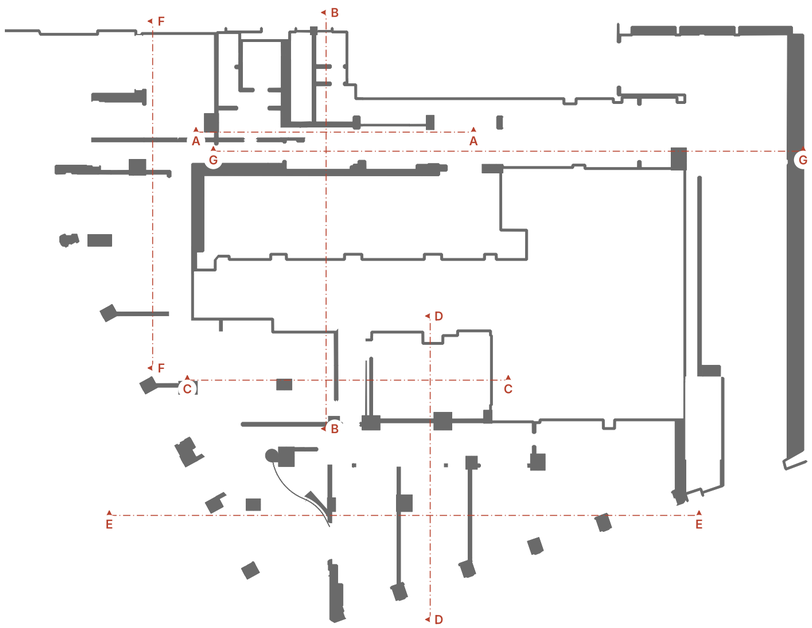

FUTURA
FORMAZIONE • LAVORO

TAVOLA S03

Sezioni
F

Dal modello 3D aggiornato
Viste oltre il taglio
senza linee nascoste

LEGENDA

- Murature tagliate
- Murature nuove
- Pilastri
- Pavimenti e solaio
- Controsoffitti
- Vetro tagliato
- Vista oltre il taglio
- Arredi in vista
- Altezze nette (m)
- Quote di riferimento


SCALA 1:50 SU FOGLIO A2

0 — 2 m

VISIO Studio · Michelessi Corporation Srl
Bozza del 9 novembre 2026


Sezione E–E

Reception, aule e sala riunioni · 1:75

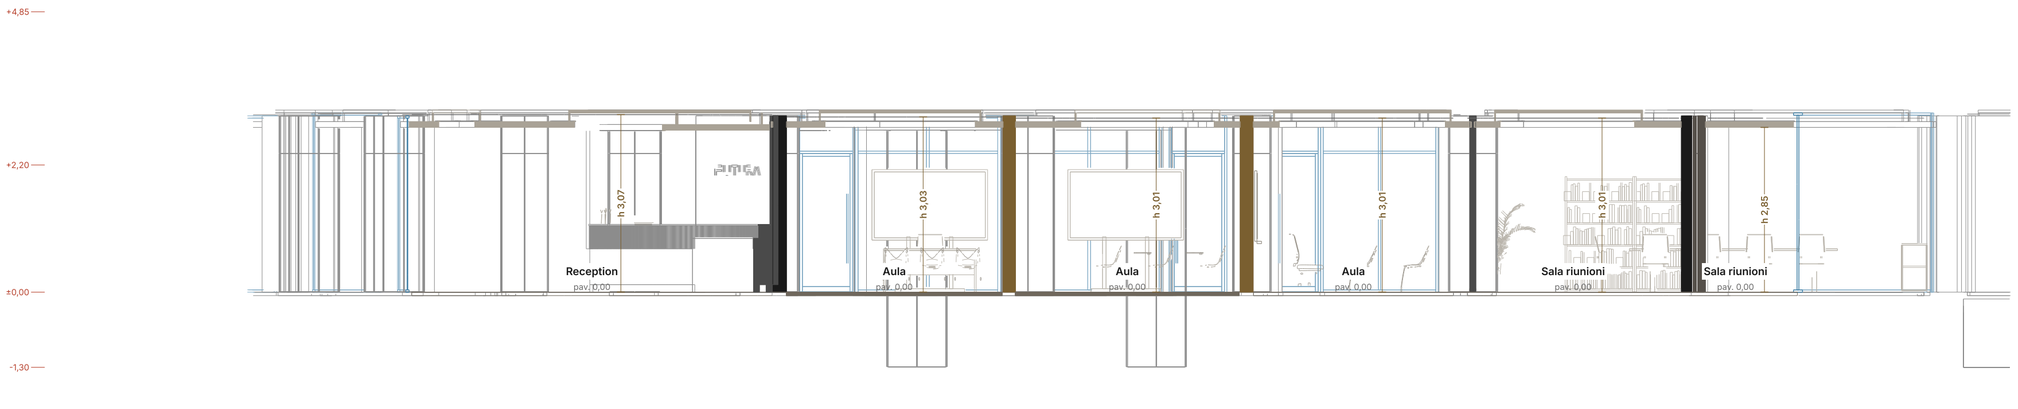

Sezione G–G

Corridoio a -1,30 con la rampa · 1:75

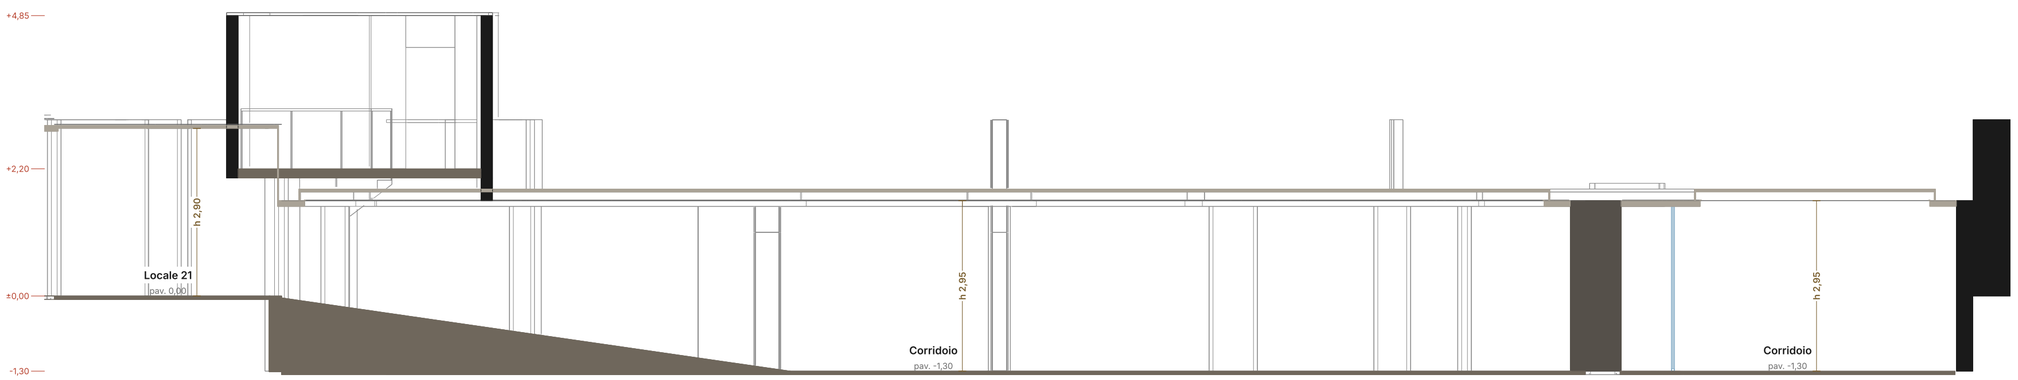

FUTURA
FORMAZIONE • LAVORO

TAVOLA S04

Sezioni E e G

Dal modello 3D aggiornato
Viste oltre il taglio
senza linee nascoste


LEGENDA

- Murature tagliate
- Murature nuove
- Pilastri
- Pavimenti e solaio
- Controsoffitti
- Vetro tagliato
- Vista oltre il taglio
- Arredi in vista
- Altezze nette (m)
- Quote di riferimento

SCALA 1:75 SU FOGLIO A2

0 — 3 m

VISIO Studio · Michelessi Corporation Srl
Bozza del 9 novembre 2026

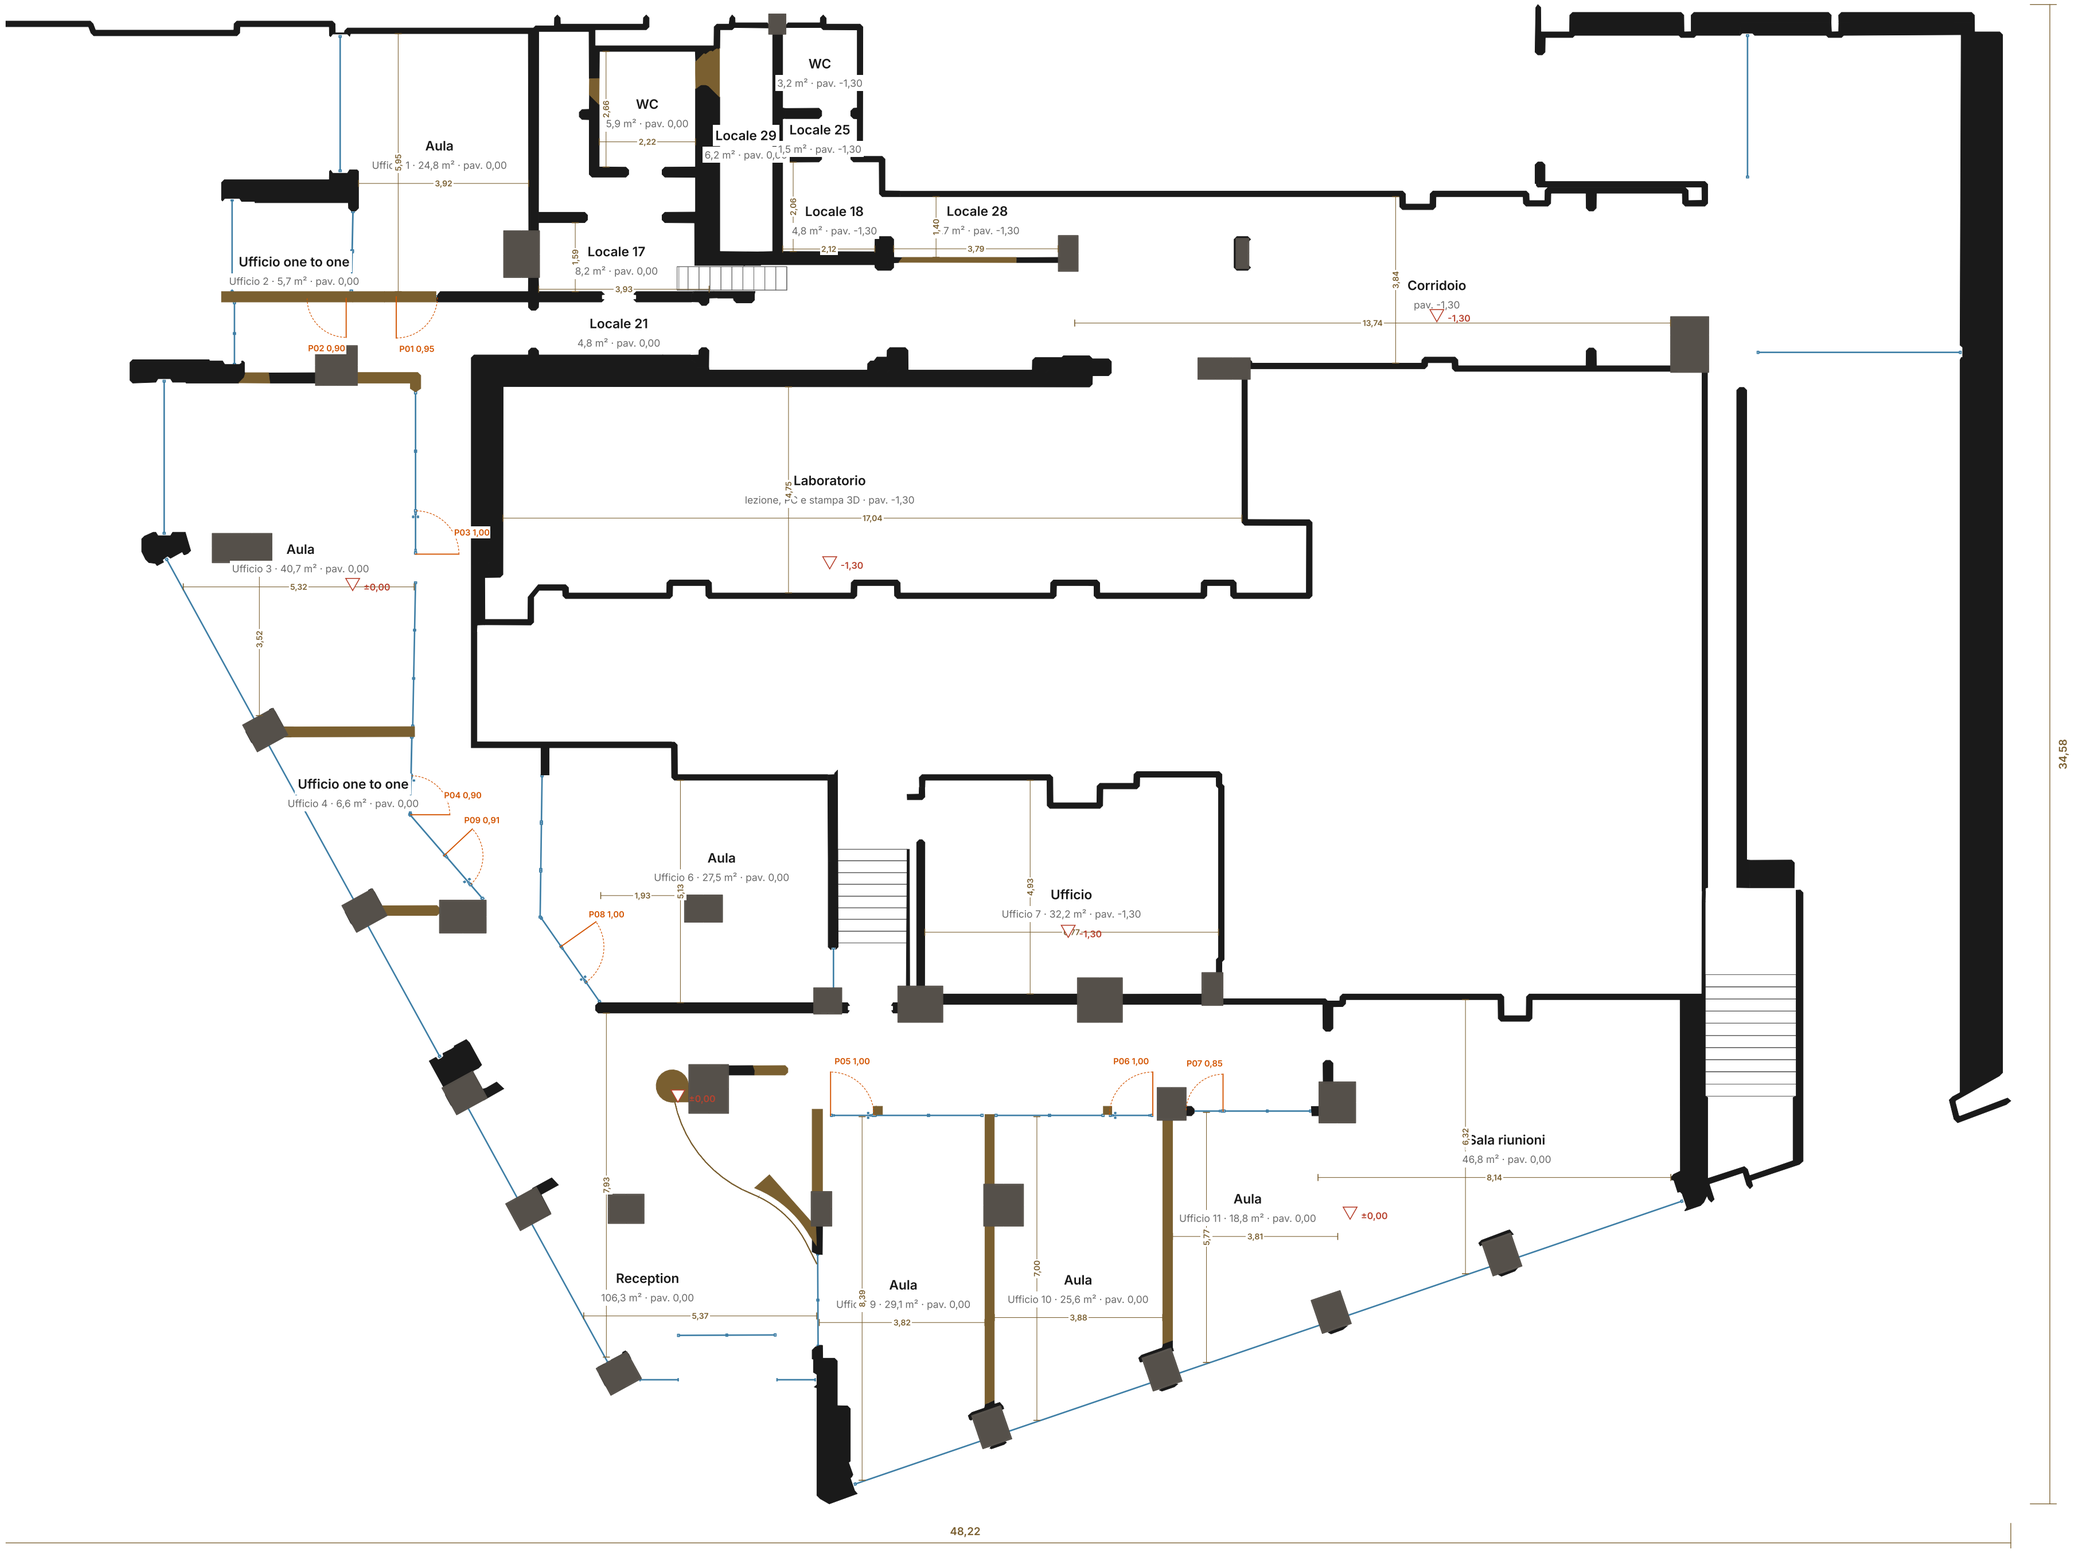

FUTURA
FORMAZIONE • LAVORO

Pianta quotata

Misure nette dei locali e ingombro generale (m), porte in vetro con luce, quote dei pavimenti. Da verificare in sito.

LEGENDA

- Murature esistenti
- Murature nuove
- Pilastri
- Pareti vetrate e vetrine
- Porte in vetro
- Misure nette (m)
- Quote del pavimento

SCALA 1:100 SU FOGLIO A2

0 — 5 m

VISIO Studio · Michelessi Corporation Srl
Bozza del 9 novembre 2026



FUTURA
FORMAZIONE • LAVORO

Controsoffitti e luci

Altezze dal pavimento
del locale (m).
328 faretti D90,
12 plafoniere, 3 lampade,
strisce LED in gola.

LEGENDA

- Campo in cartongesso h 2,80
- Veletta perimetrale h 2,55
- Controsoffitto piano h 2,60
- Anello sospeso reception h 2,50
- Striscia LED in gola
- Faretto D90 / plafoniera / lampada

SCALA 1:100 SU FOGLIO A2

0 — 5 m

VISIO Studio · Michelessi Corporation Srl
Bozza del 9 novembre 2026