
FUTURA
FORMAZIONE • LAVORO

TAVOLA V01

Pareti vetrate

Pianta con codici, lunghezze e porte. Misure in metri dal modello, da verificare in sito. Vetrine escluse.

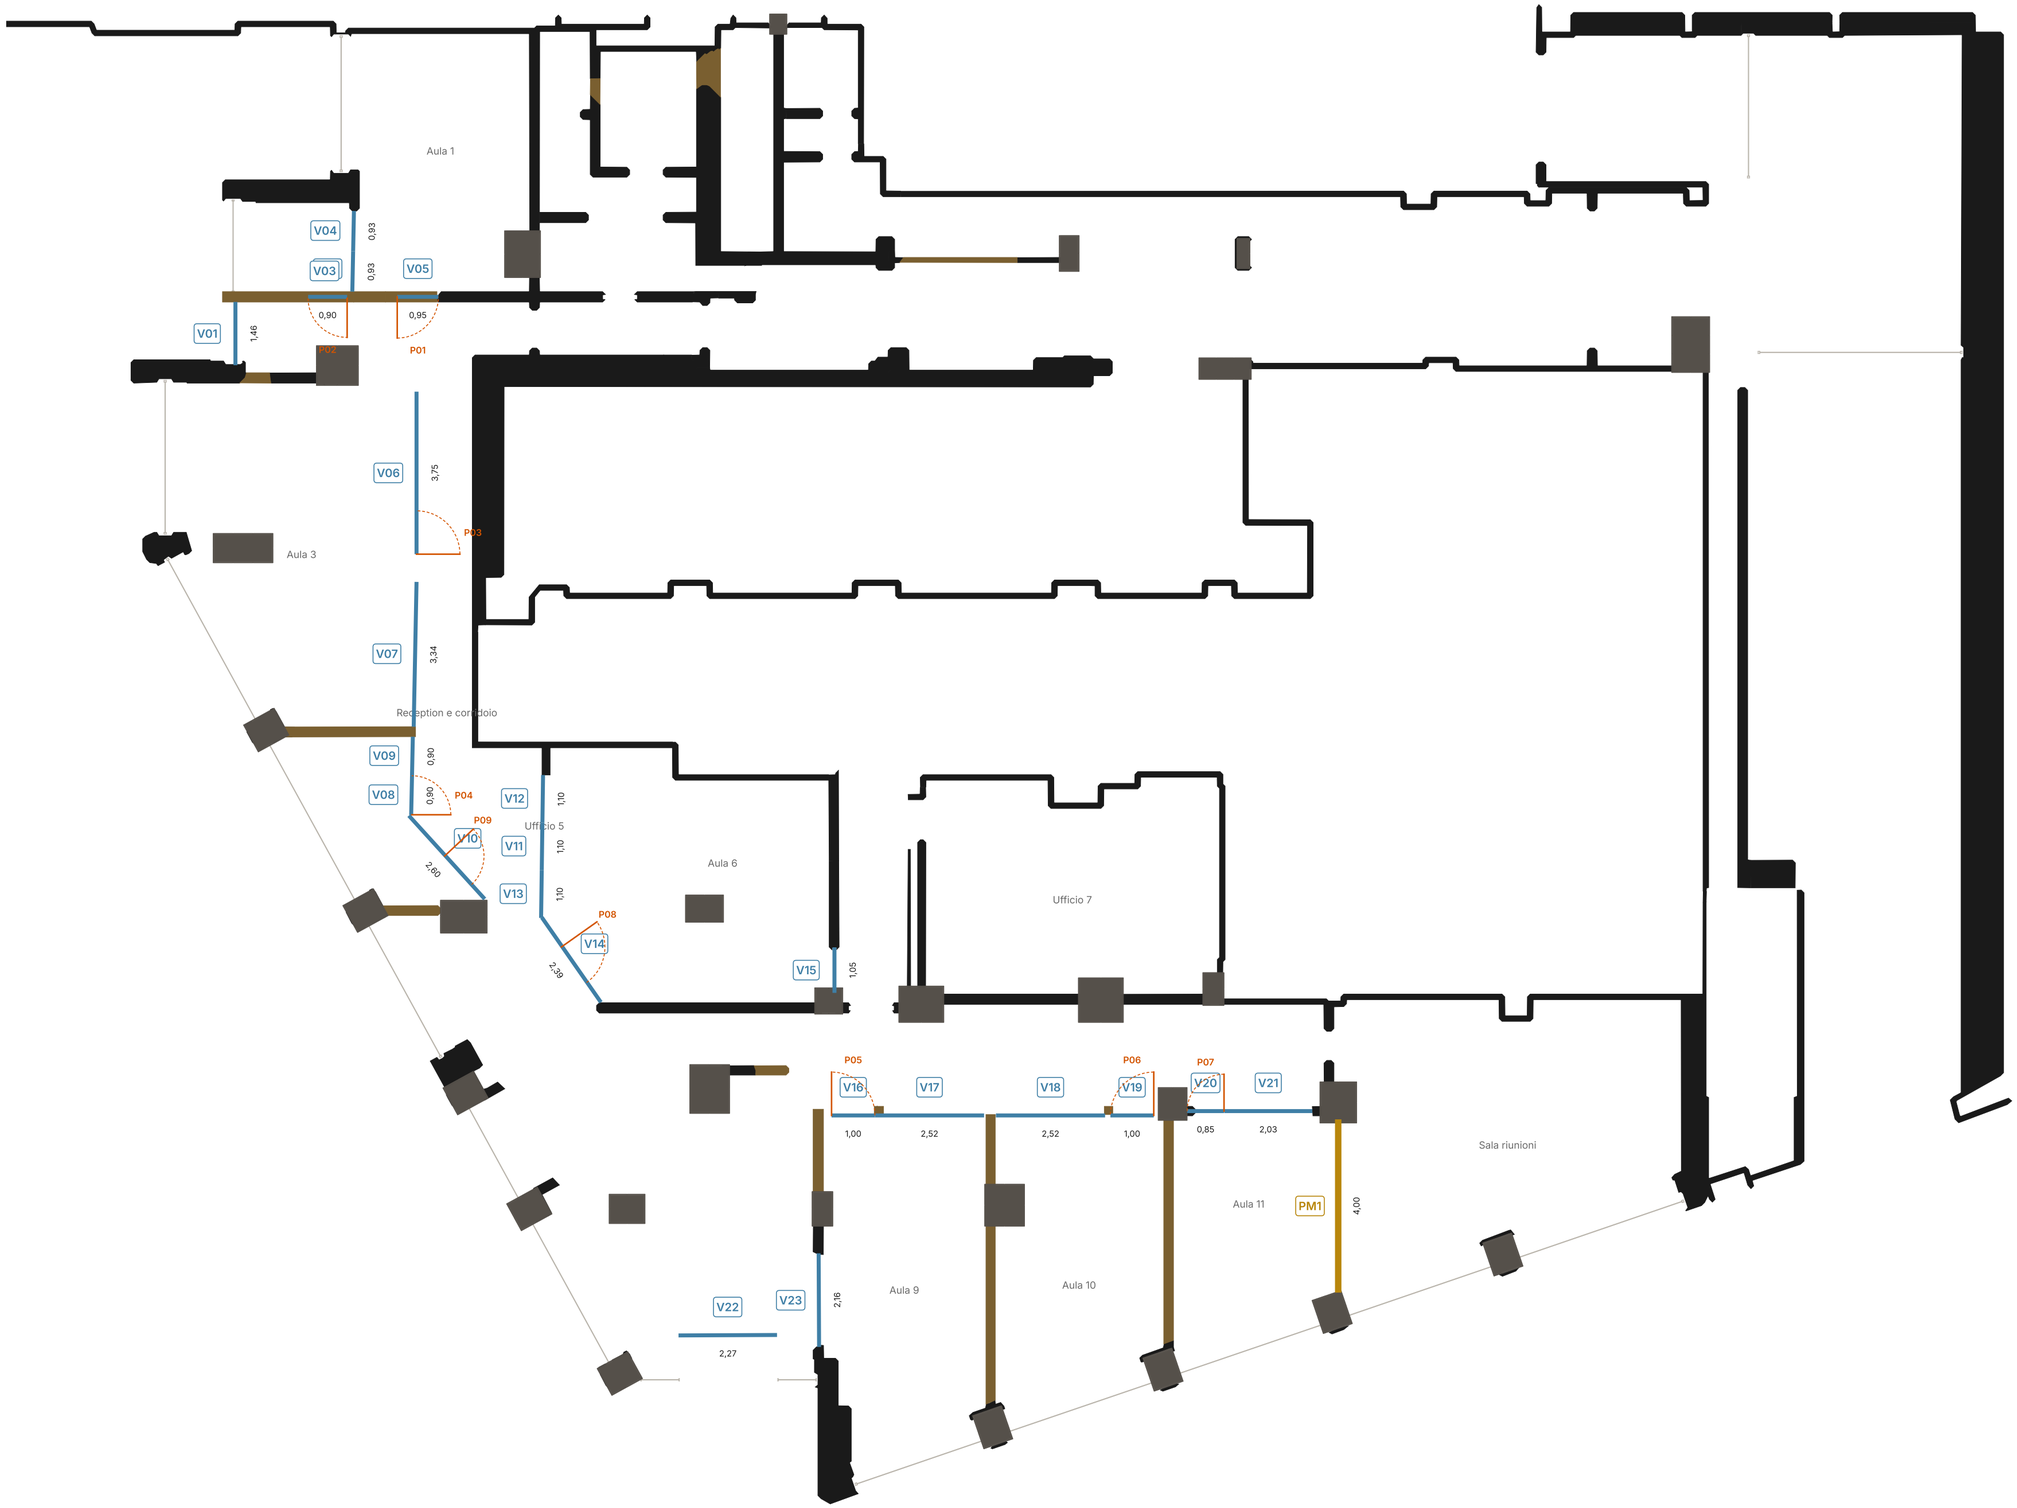

LEGENDA

- Parete vetrata interna (codice V)
- Porta in vetro e apertura (codice P)
- Parete mobile (PM1)
- Vetrine esterne, escluse
- Murature esistenti
- Murature nuove


SCALA 1:100 SU FOGLIO A2

0 — 5 m

VISIO Studio · Michelessi Corporation Srl
Bozza del 9 novembre 2026


V01 · Corridoio ovest / Facciata

lato ovest del corridoio verso la facciata: da verificare in sito

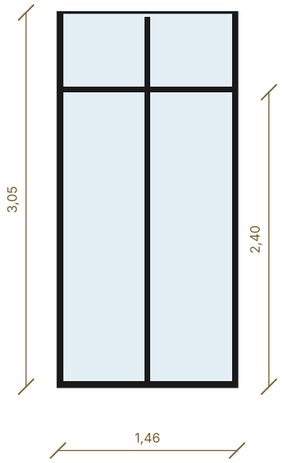


V02 · Reception e corridoio / Ufficio 2

porta in vetro nel muro nuovo verso il corridoio

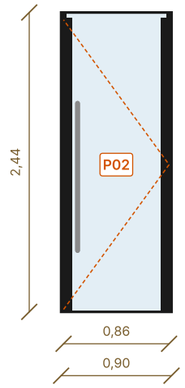

V03 · Aula 1 / Ufficio 2

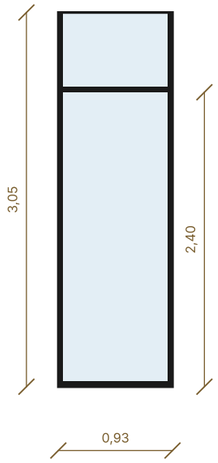

V04 · Aula 1 / Ufficio 2

V05 · Aula 1 / Reception e corridoio

tutto il tratto 004 diventa porta

V06 · Aula 3 / Reception e corridoio

si apre verso il corridoio

FUTURA
FORMAZIONE • LAVORO

TAVOLA V02

Prospetti vetrate

Viste dal lato del codice in pianta. Profili neri 40 mm, traverso a +2,40, porte con maniglione.

LEGENDA


- Profili e telai
- Vetro
- Porta: lato cerniere
- Parete mobile
- Quote in metri

SCALA 1:50 SU FOGLIO A3


0 — 2 m

VISIO Studio · Michelessi Corporation Srl
Bozza del 9 novembre 2026


V07 · Aula 3 / Reception e corridoio

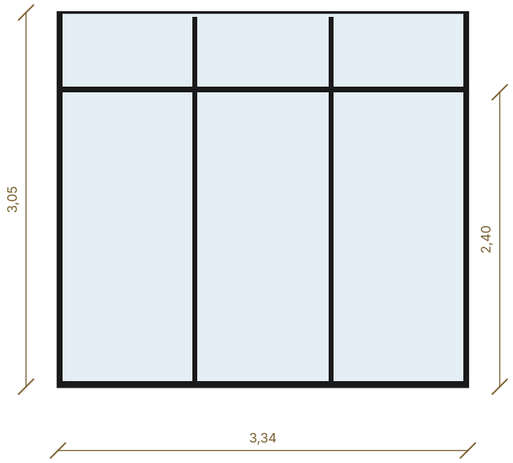

V08 · Reception e corridoio / Ufficio 4

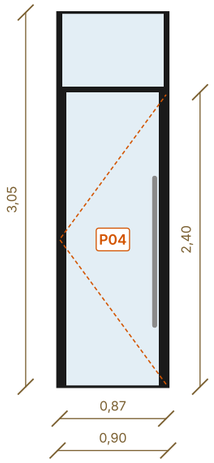


V09 · Reception e corridoio / Ufficio 4

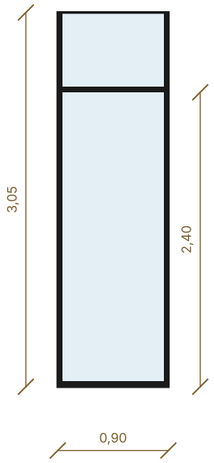


V10 · Reception e corridoio / Ufficio 5


vetrata diagonale; posa inclinata (132 gradi in pianta)

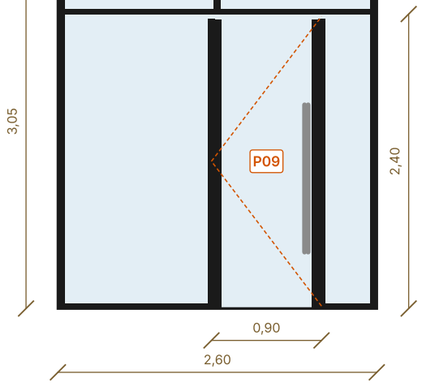

V11 · Aula 6 / Ufficio 5

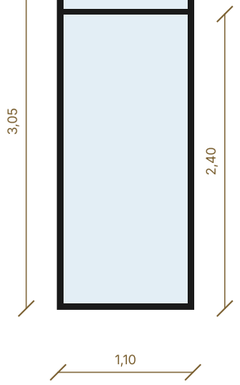

V12 · Aula 6 / Ufficio 5

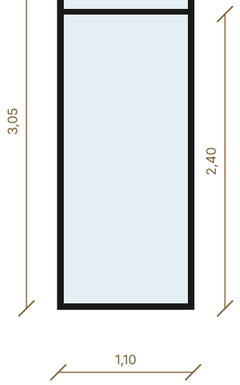

FUTURA
FORMAZIONE • LAVORO

TAVOLA V03

Prospetti vetrate

Viste dal lato del codice in pianta. Profili neri 40 mm, traverso a +2,40, porte con maniglione.

LEGENDA


- Profili e telai
- Vetro
- Porta: lato cerniere
- Parete mobile
- Quote in metri

SCALA 1:50 SU FOGLIO A3

0 — 2 m


VISIO Studio · Michelessi Corporation Srl
Bozza del 9 novembre 2026

V13 · Aula 6 / Ufficio 5

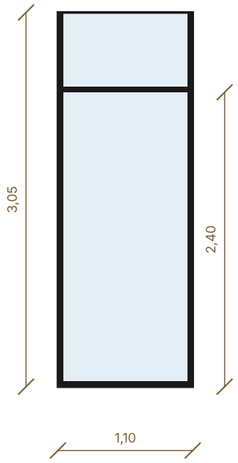


V14 · Aula 6 / Reception e corridoio

vetrata diagonale verso la reception; posa inclinata (125 gradi in pianta)

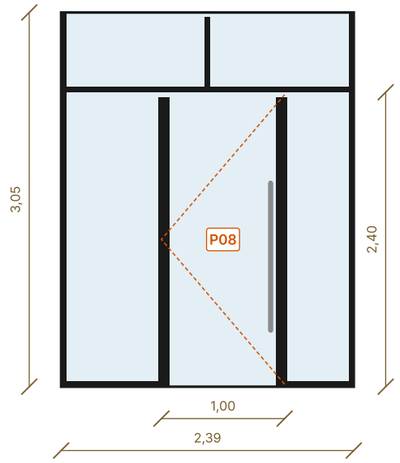


V15 · Aula 6 / Disimpegno scala

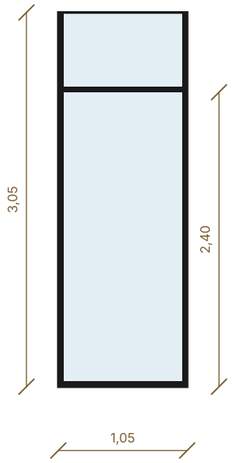


V16 · Aula 9 / Reception e corridoio


nel vano esistente tra muro e vetrata

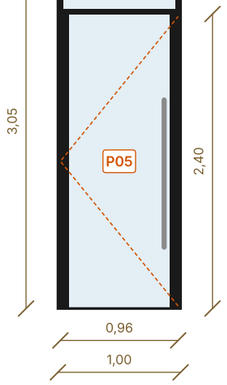

V17 · Aula 9 / Reception e corridoio

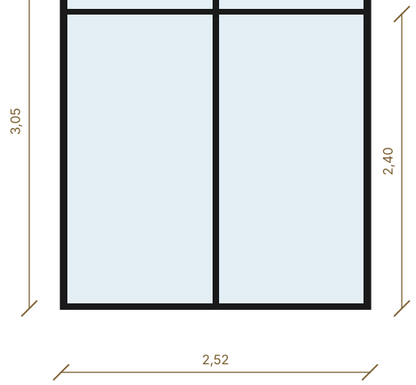

V18 · Aula 10 / Reception e corridoio

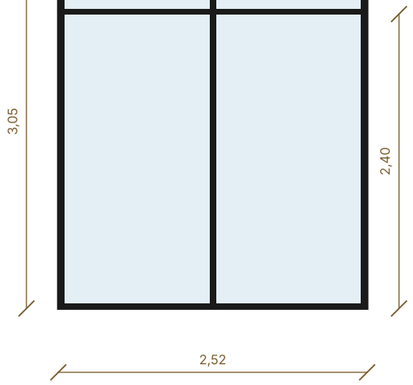

FUTURA
FORMAZIONE • LAVORO

TAVOLA V04

Prospetti vetrate

Viste dal lato del codice in pianta. Profili neri 40 mm, traverso a +2,40, porte con maniglione.

LEGENDA

- Profili e telai
- Vetro
- Porta: lato cerniere
- Parete mobile
- Quote in metri


SCALA 1:50 SU FOGLIO A3

0 — 2 m

VISIO Studio · Michelessi Corporation Srl
Bozza del 9 novembre 2026


V19 · Aula 10 / Reception e corridoio

nel vano esistente

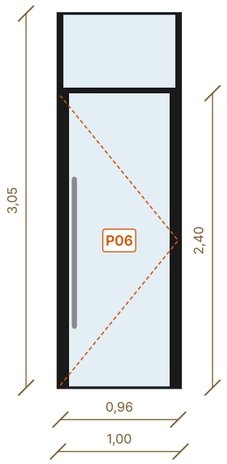


V20 · Aula 11 / Reception e corridoio

nel vano esistente, accanto al pilastro

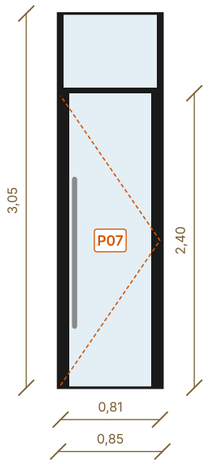


V21 · Aula 11 / Reception e corridoio

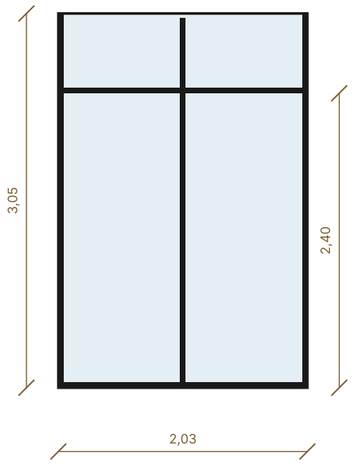


V22 · Ingresso / Reception


alta 2,93 m, nella zona d'ingresso: da verificare se e' bussola o vetrata interna

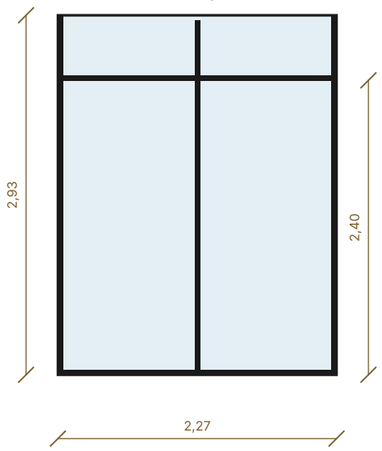

V23 · Aula 9 / Reception e corridoio

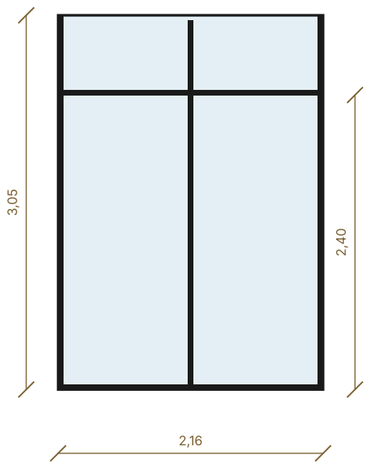

PM1 · Aula 11 / Sala riunioni

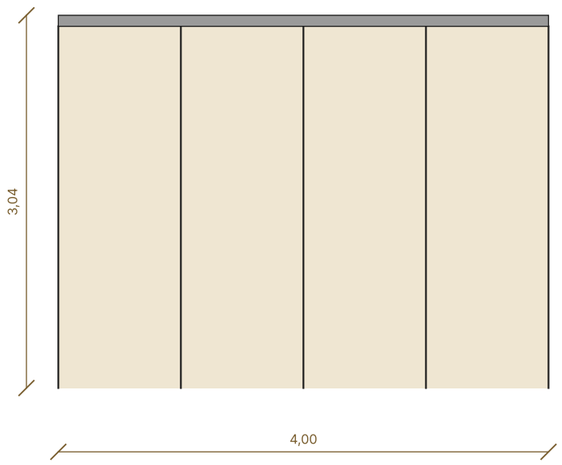

FUTURA
FORMAZIONE • LAVORO

TAVOLA V05

Prospetti vetrate

Viste dal lato del codice in pianta. Profili neri 40 mm, traverso a +2,40, porte con maniglione.

LEGENDA

- Profili e telai
- Vetro
- Porta: lato cerniere
- Parete mobile
- Quote in metri

SCALA 1:50 SU FOGLIO A3

0 — 2 m

VISIO Studio · Michelessi Corporation Srl

Bozza del 9 novembre 2026