
FUTURA
FORMAZIONE • LAVORO

TAVOLA V01

Pareti vetrate

Pianta con codici, lunghezze e porte. Misure in metri dal modello, da verificare in sito. Vetrine escluse.

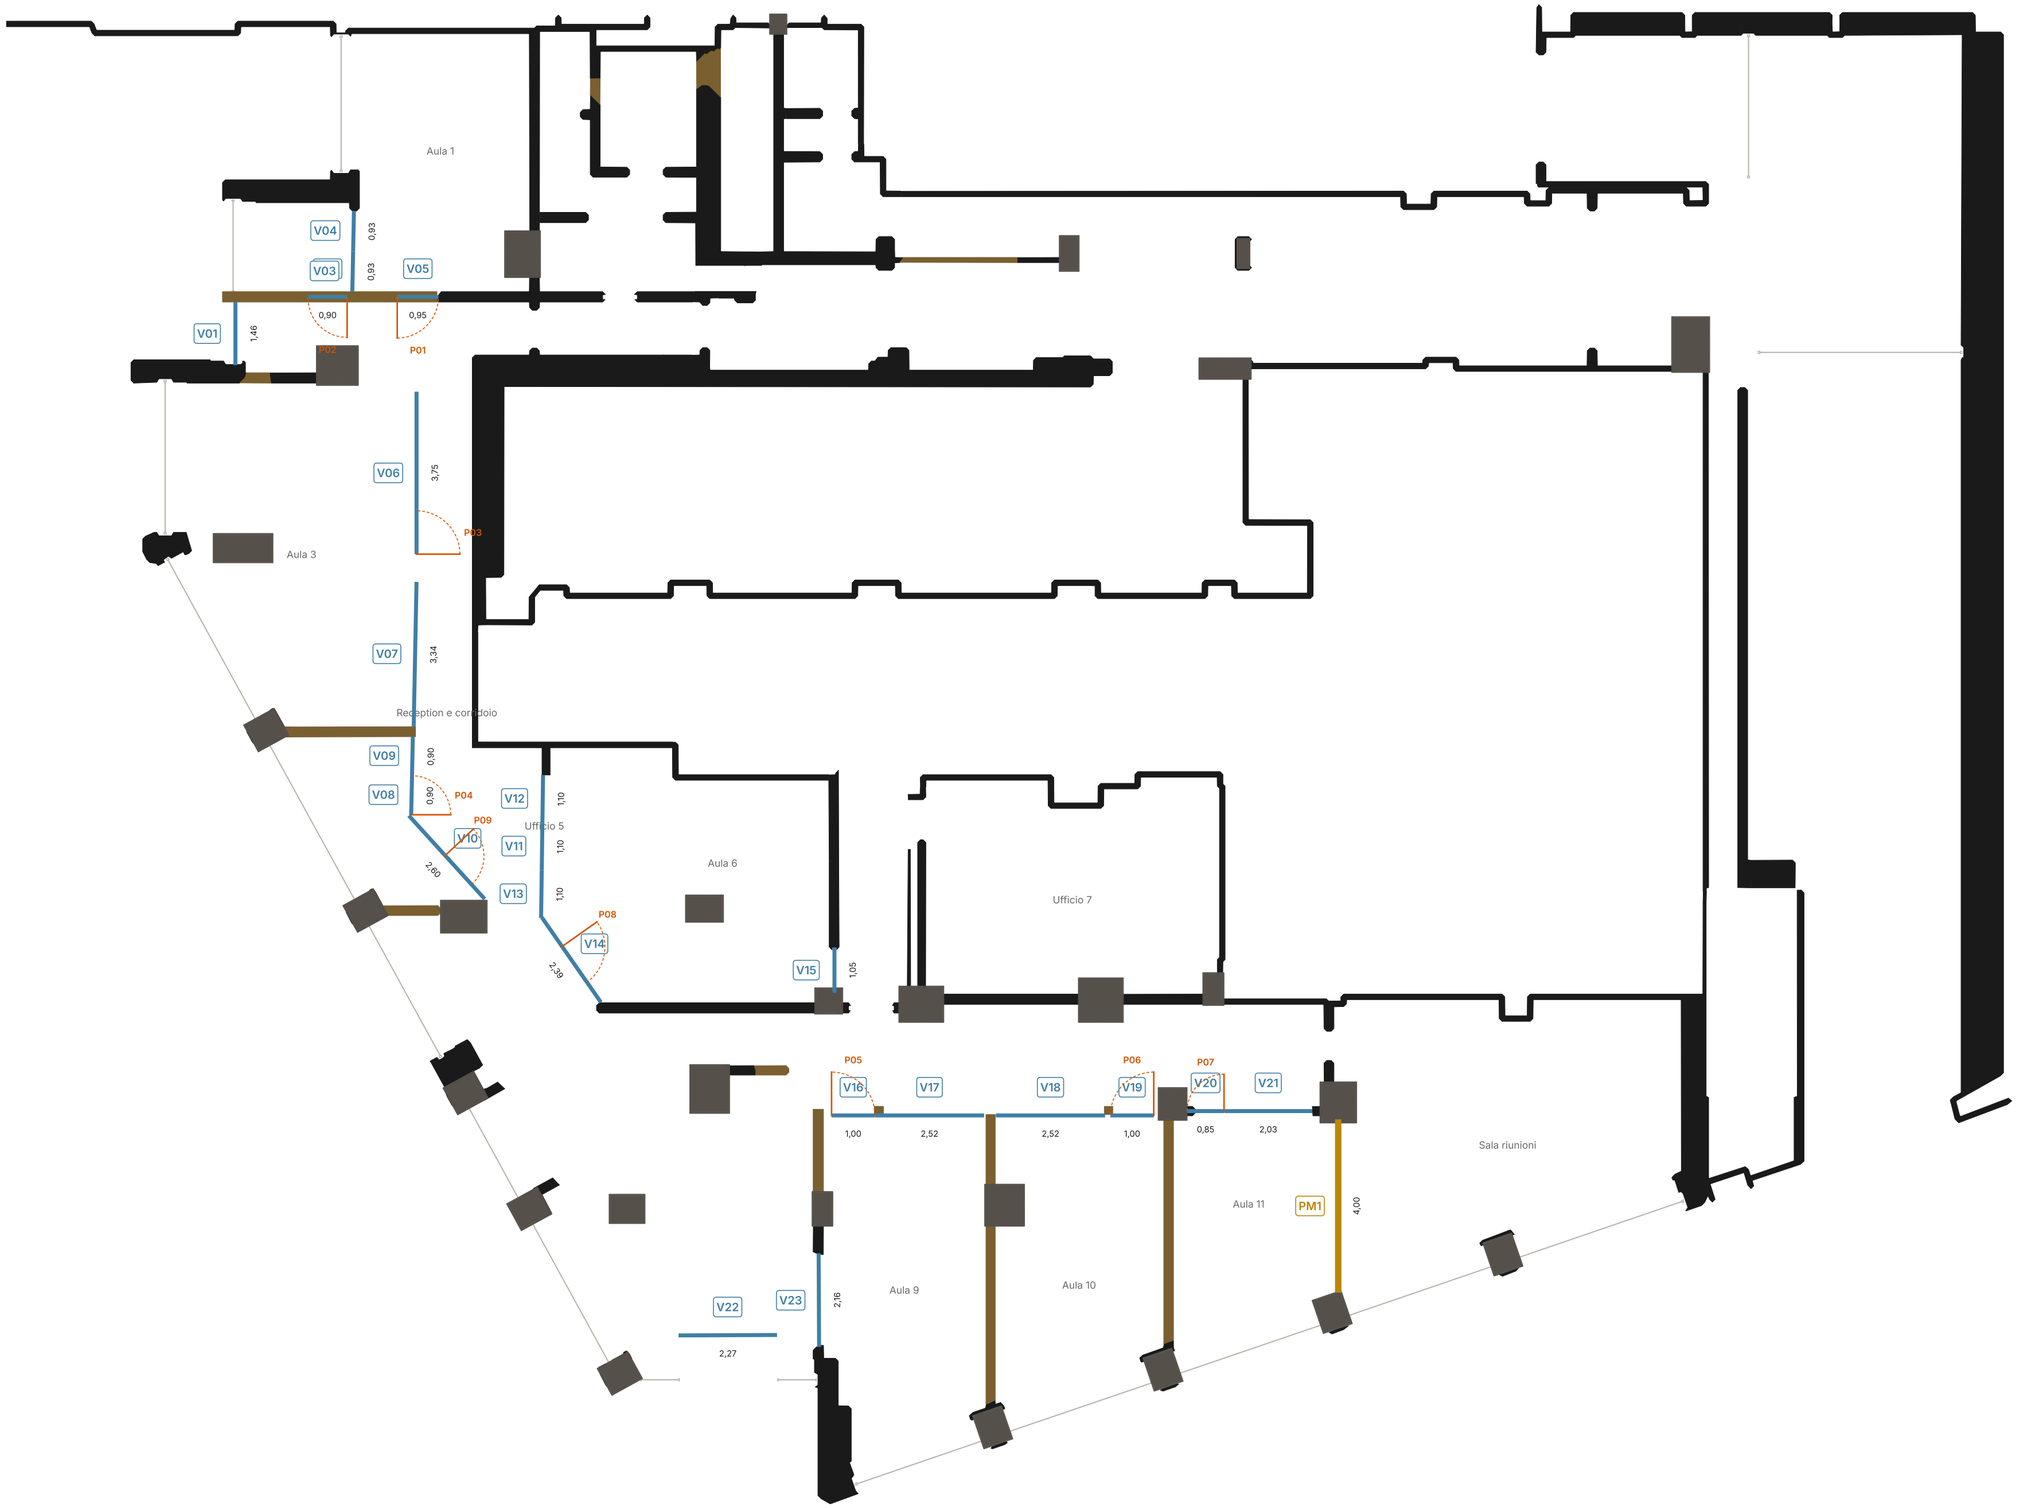

LEGENDA

- Parete vetrata interna (codice V)
- Porta in vetro e apertura (codice P)
- Parete mobile (PM1)
- Vetrine esterne, escluse
- Murature esistenti
- Murature nuove

SCALA 1:100 SU FOGLIO A2

0 — 5 m

VISIO Studio · Michelessi Corporation Srl
Bozza del 9 novembre 2026