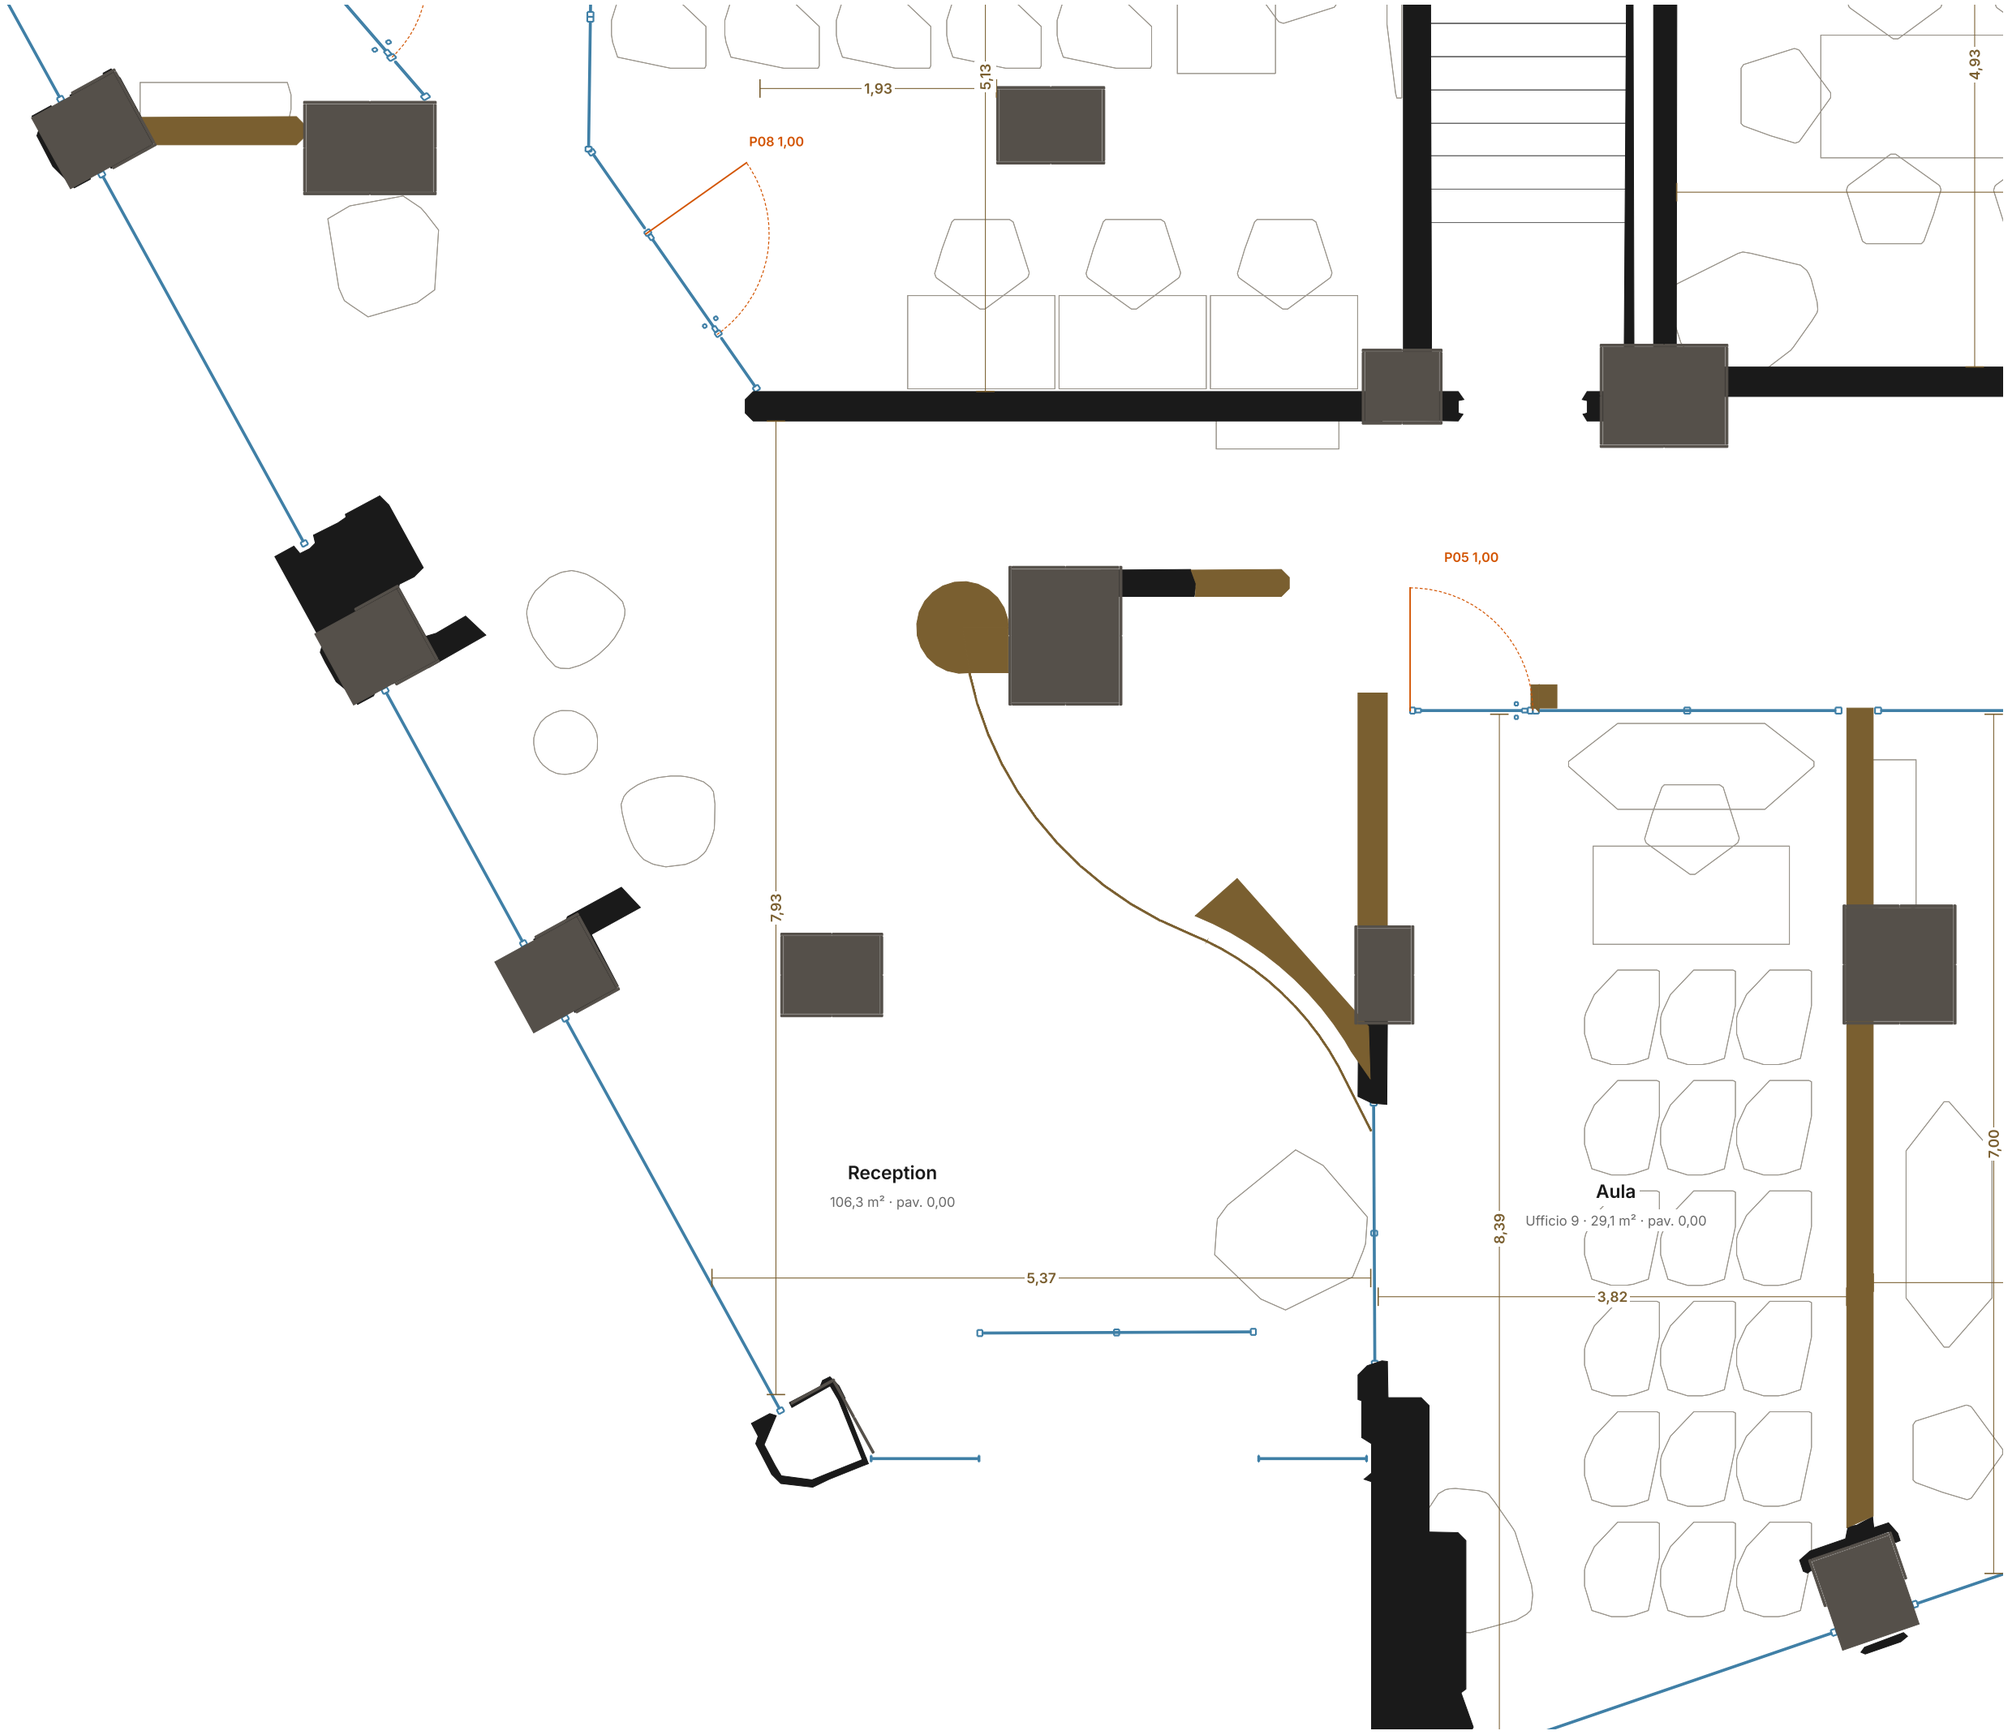


FUTURA
FORMAZIONE • LAVORO

TAVOLA D01

Reception

Ingresso e bancone

LEGENDA

- Murature esistenti
- Murature nuove
- Pilastri
- Vetrate e vetrine
- Scale
- Arredi e sanitari
- Misure nette (m)

SCALA 1:50 SU FOGLIO A3

0 — 2 m

VISIO Studio · Michelessi Corporation Srl
Bozza dell'11 novembre 2026