

Sezione E–E

Reception, Aule 11 e 12 · 1:75

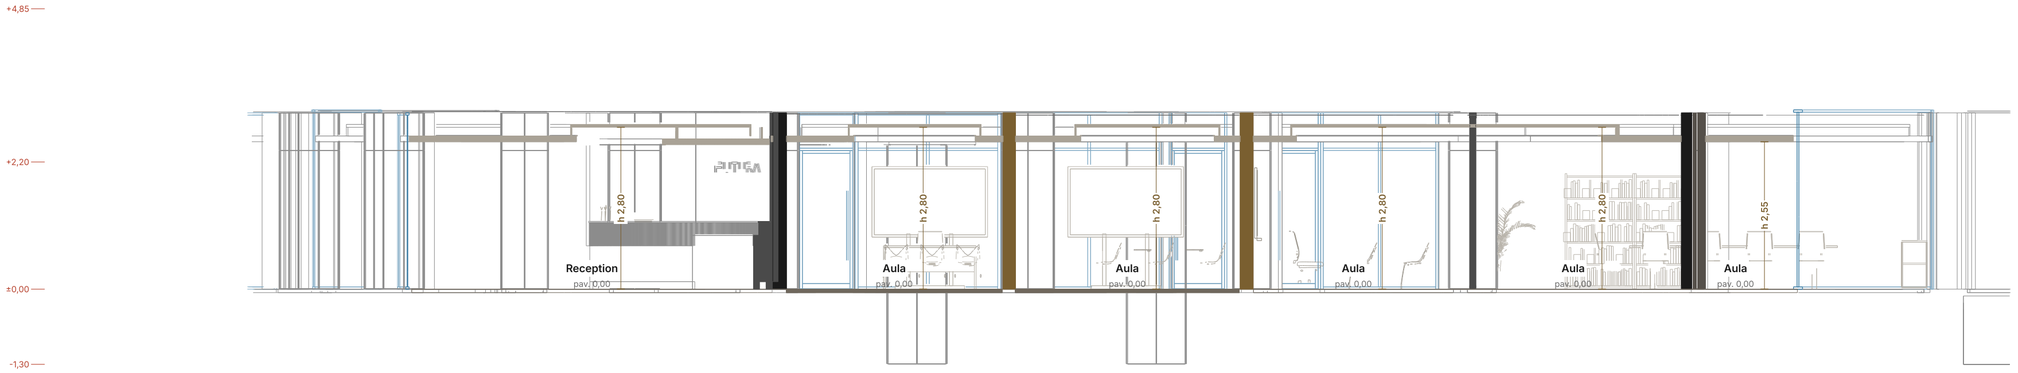

Sezione G–G

Corridoio a -1,30 con la rampa · 1:75

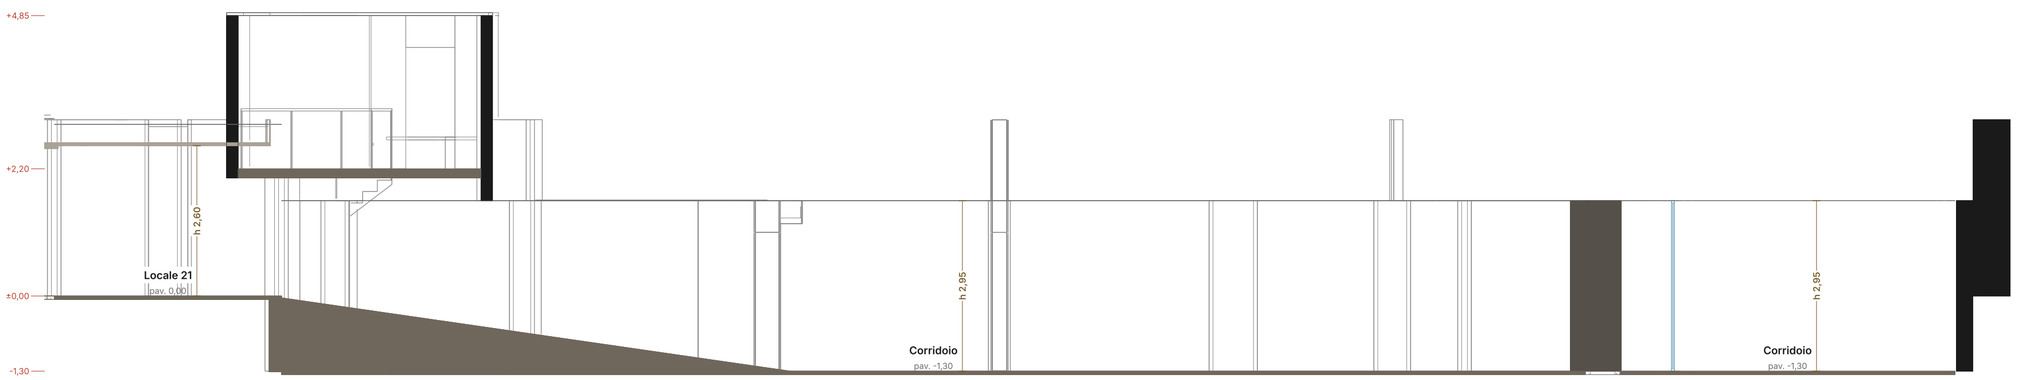

FUTURA
FORMAZIONE • LAVORO

TAVOLA S04

Sezioni E e G

Dal modello 3D aggiornato
Viste oltre il taglio
senza linee nascoste

LEGENDA

- Murature tagliate
- Murature nuove
- Pilastri
- Pavimenti e solaio
- Controsoffitti
- Vetro tagliato
- Vista oltre il taglio
- Arredi in vista
- Altezze nette (m)
- Quote di riferimento

SCALA 1:75 SU FOGLIO A2

0 — 3 m

VISIO Studio · Michelessi Corporation Srl
Bozza dell'11 novembre 2026