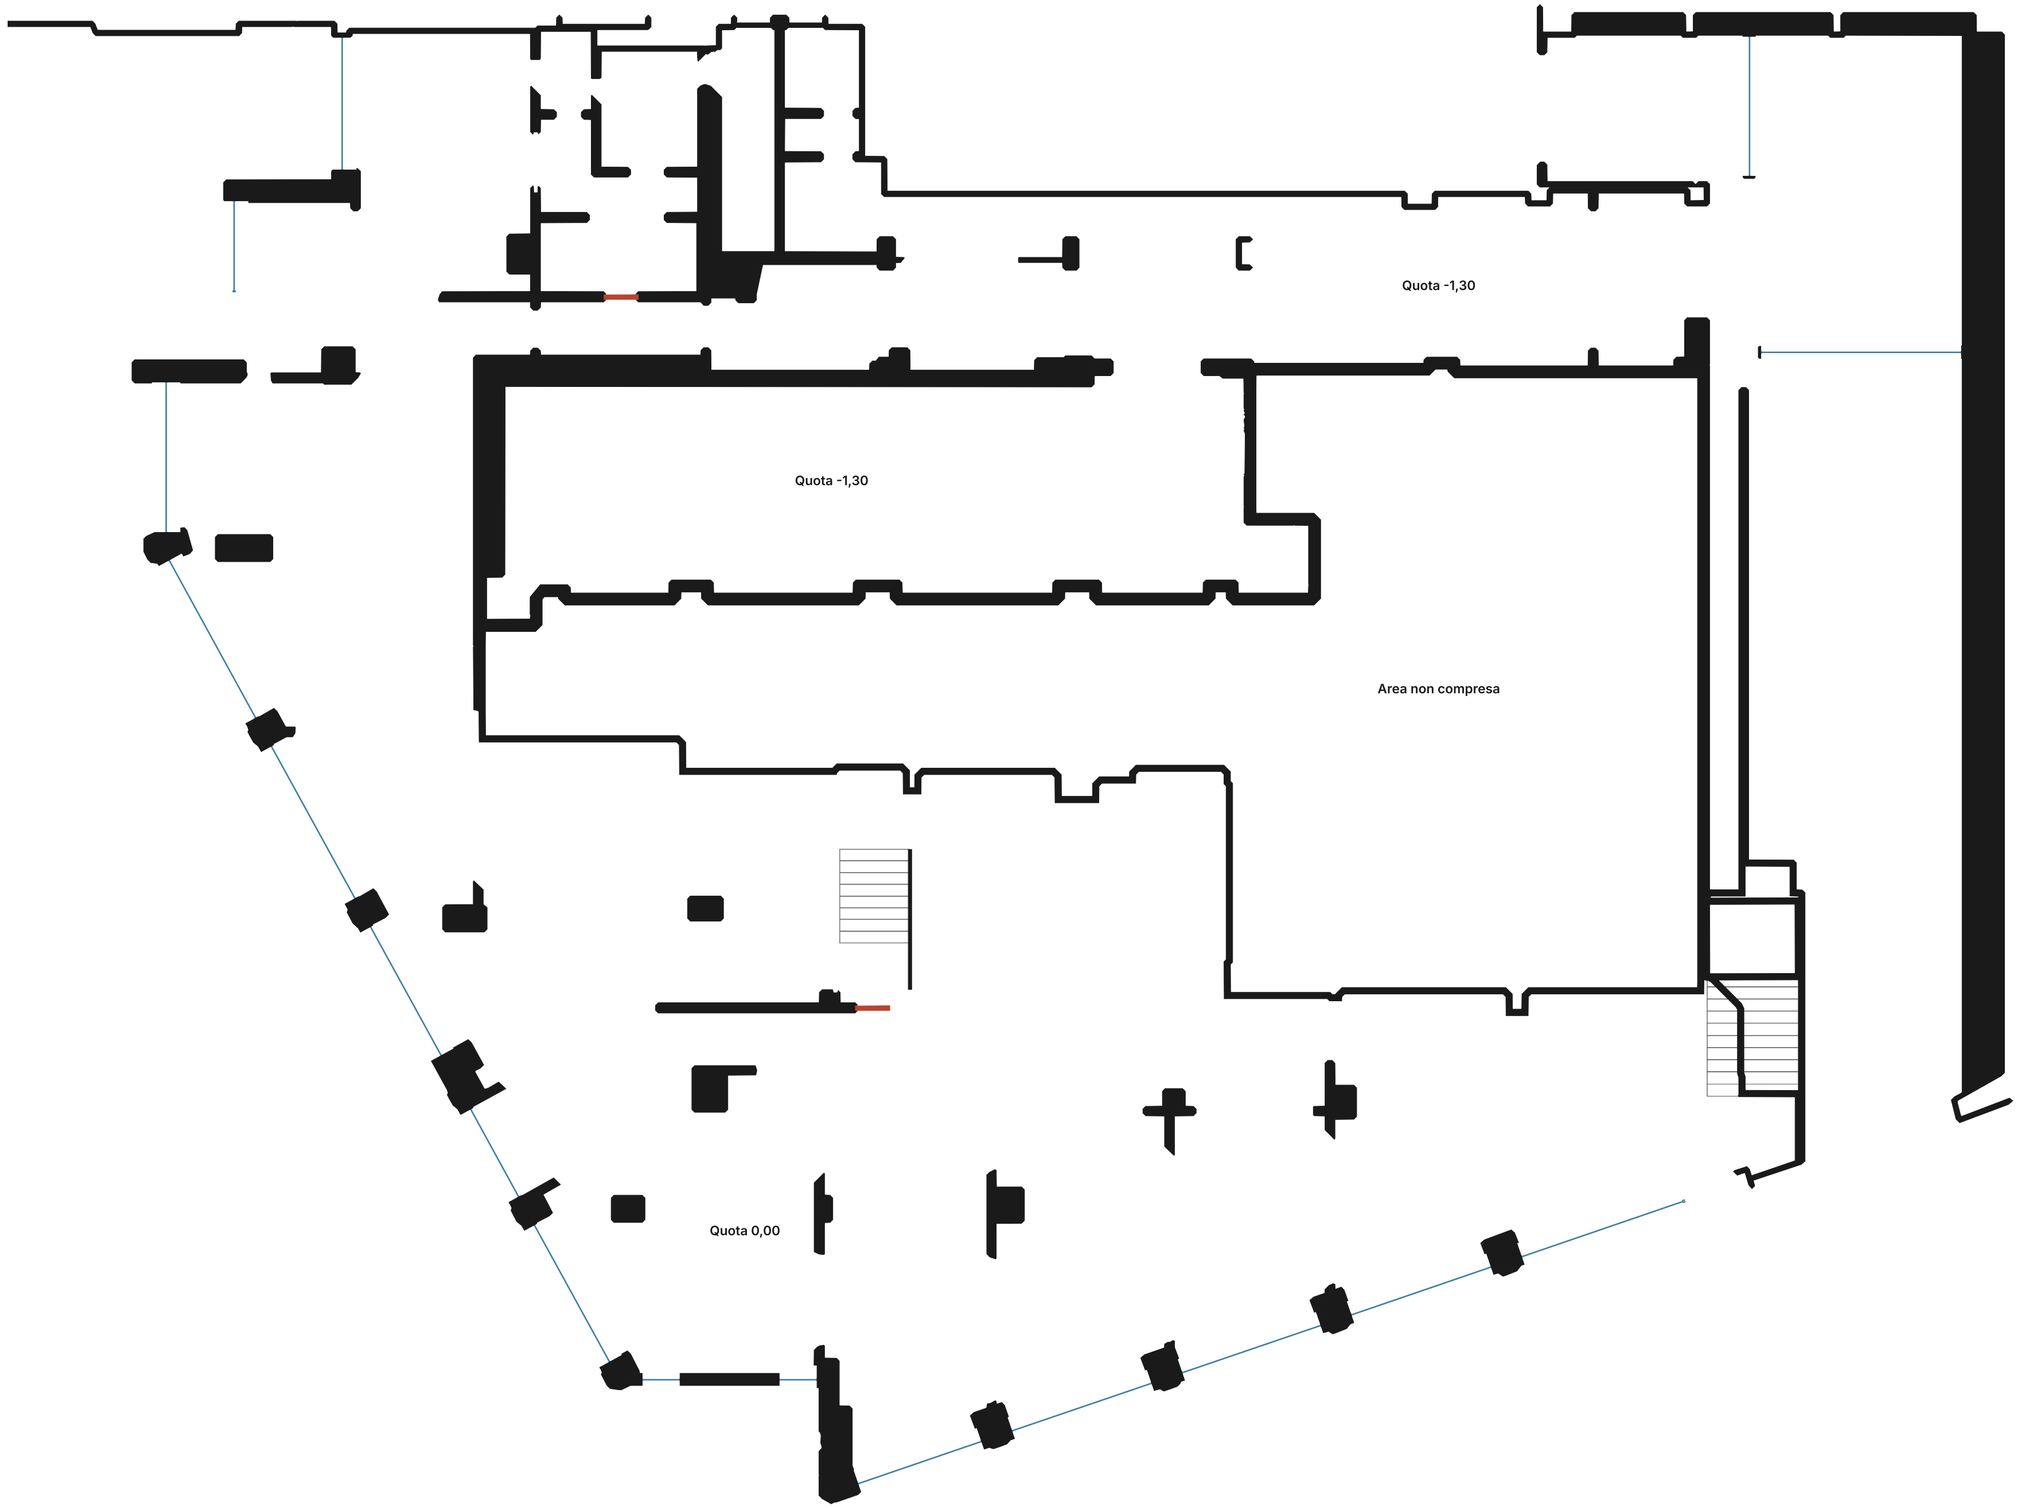


FUTURA
FORMAZIONE • LAVORO

Ante operam

Stato di fatto
dal rilievo 3D e dalla
planimetria EPT Rev01
Taglio a +1,00

LEGENDA

- Murature esistenti
- Da demolire
- Vetrine esistenti
- Scale

SCALA 1:100 SU FOGLIO A2

0 — 5 m

VISIO

VISIO Studio · Michelessi Corporation Srl
Bozza dell'11 novembre 2026