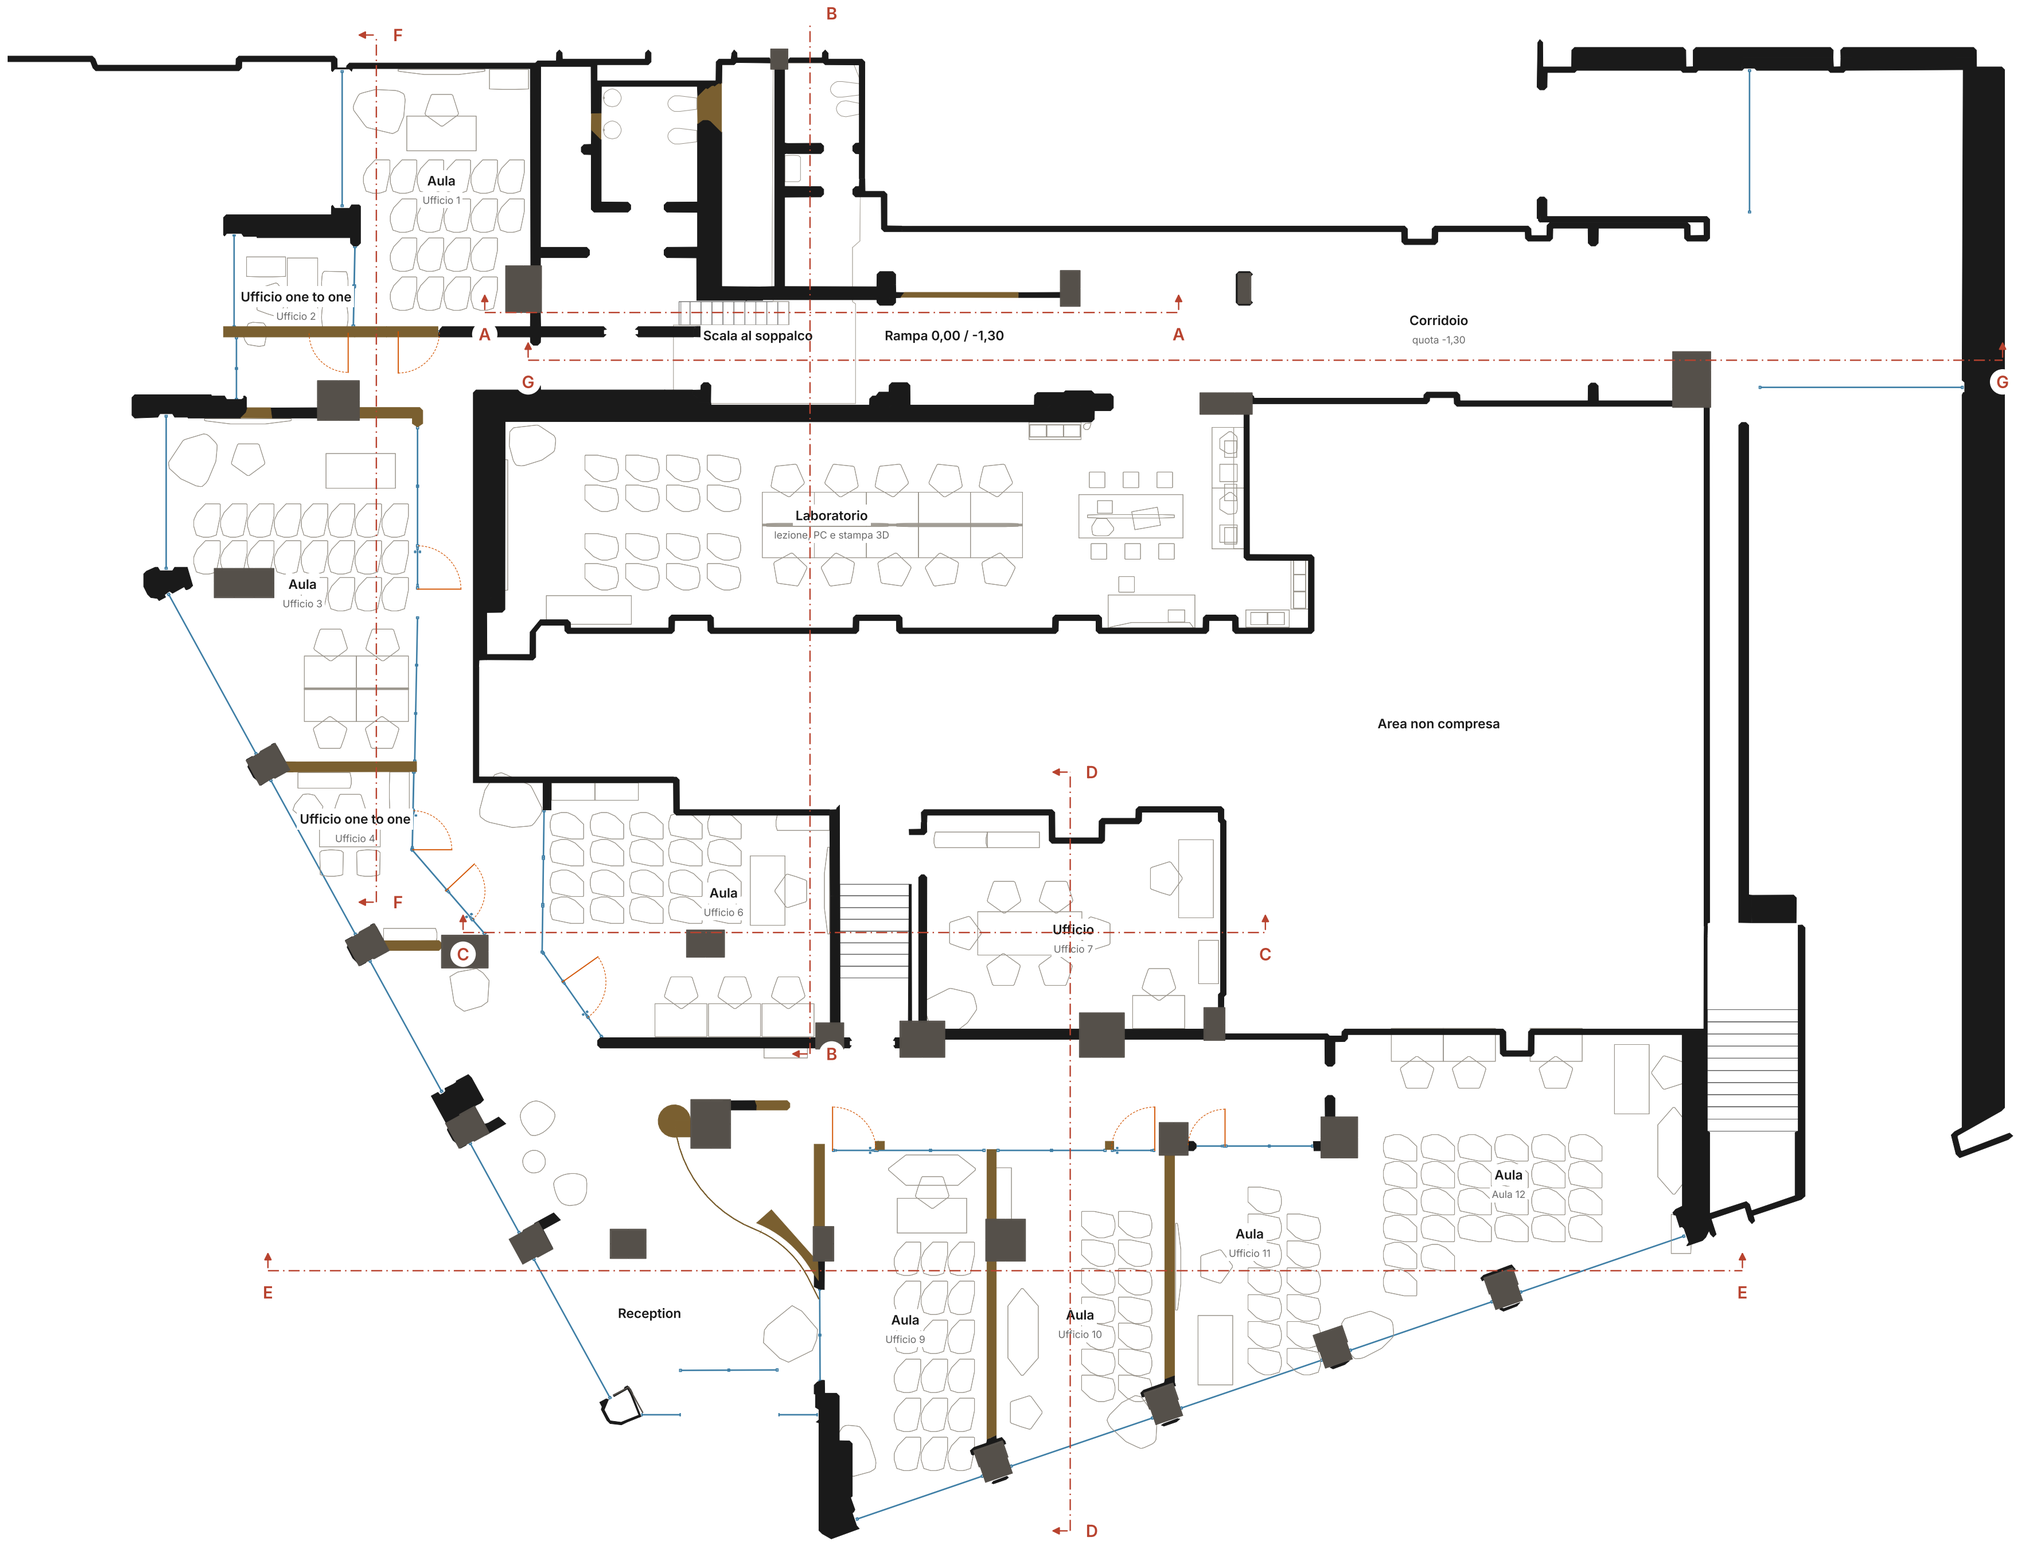


FUTURA
FORMAZIONE • LAVORO

Post operam

Progetto dal modello 3D aggiornato
Taglio a +1,00

LEGENDA

- Murature esistenti
- Murature nuove e bancone
- Pilastri rivestiti
- Pareti vetrate e vetrine
- Scale
- Arredi e sanitari
- Soppalco sopra il taglio
- Tracce delle sezioni

SCALA 1:100 SU FOGLIO A2

0 — 5 m

VISIO Studio · Michelessi Corporation Srl
Bozza dell'11 novembre 2026