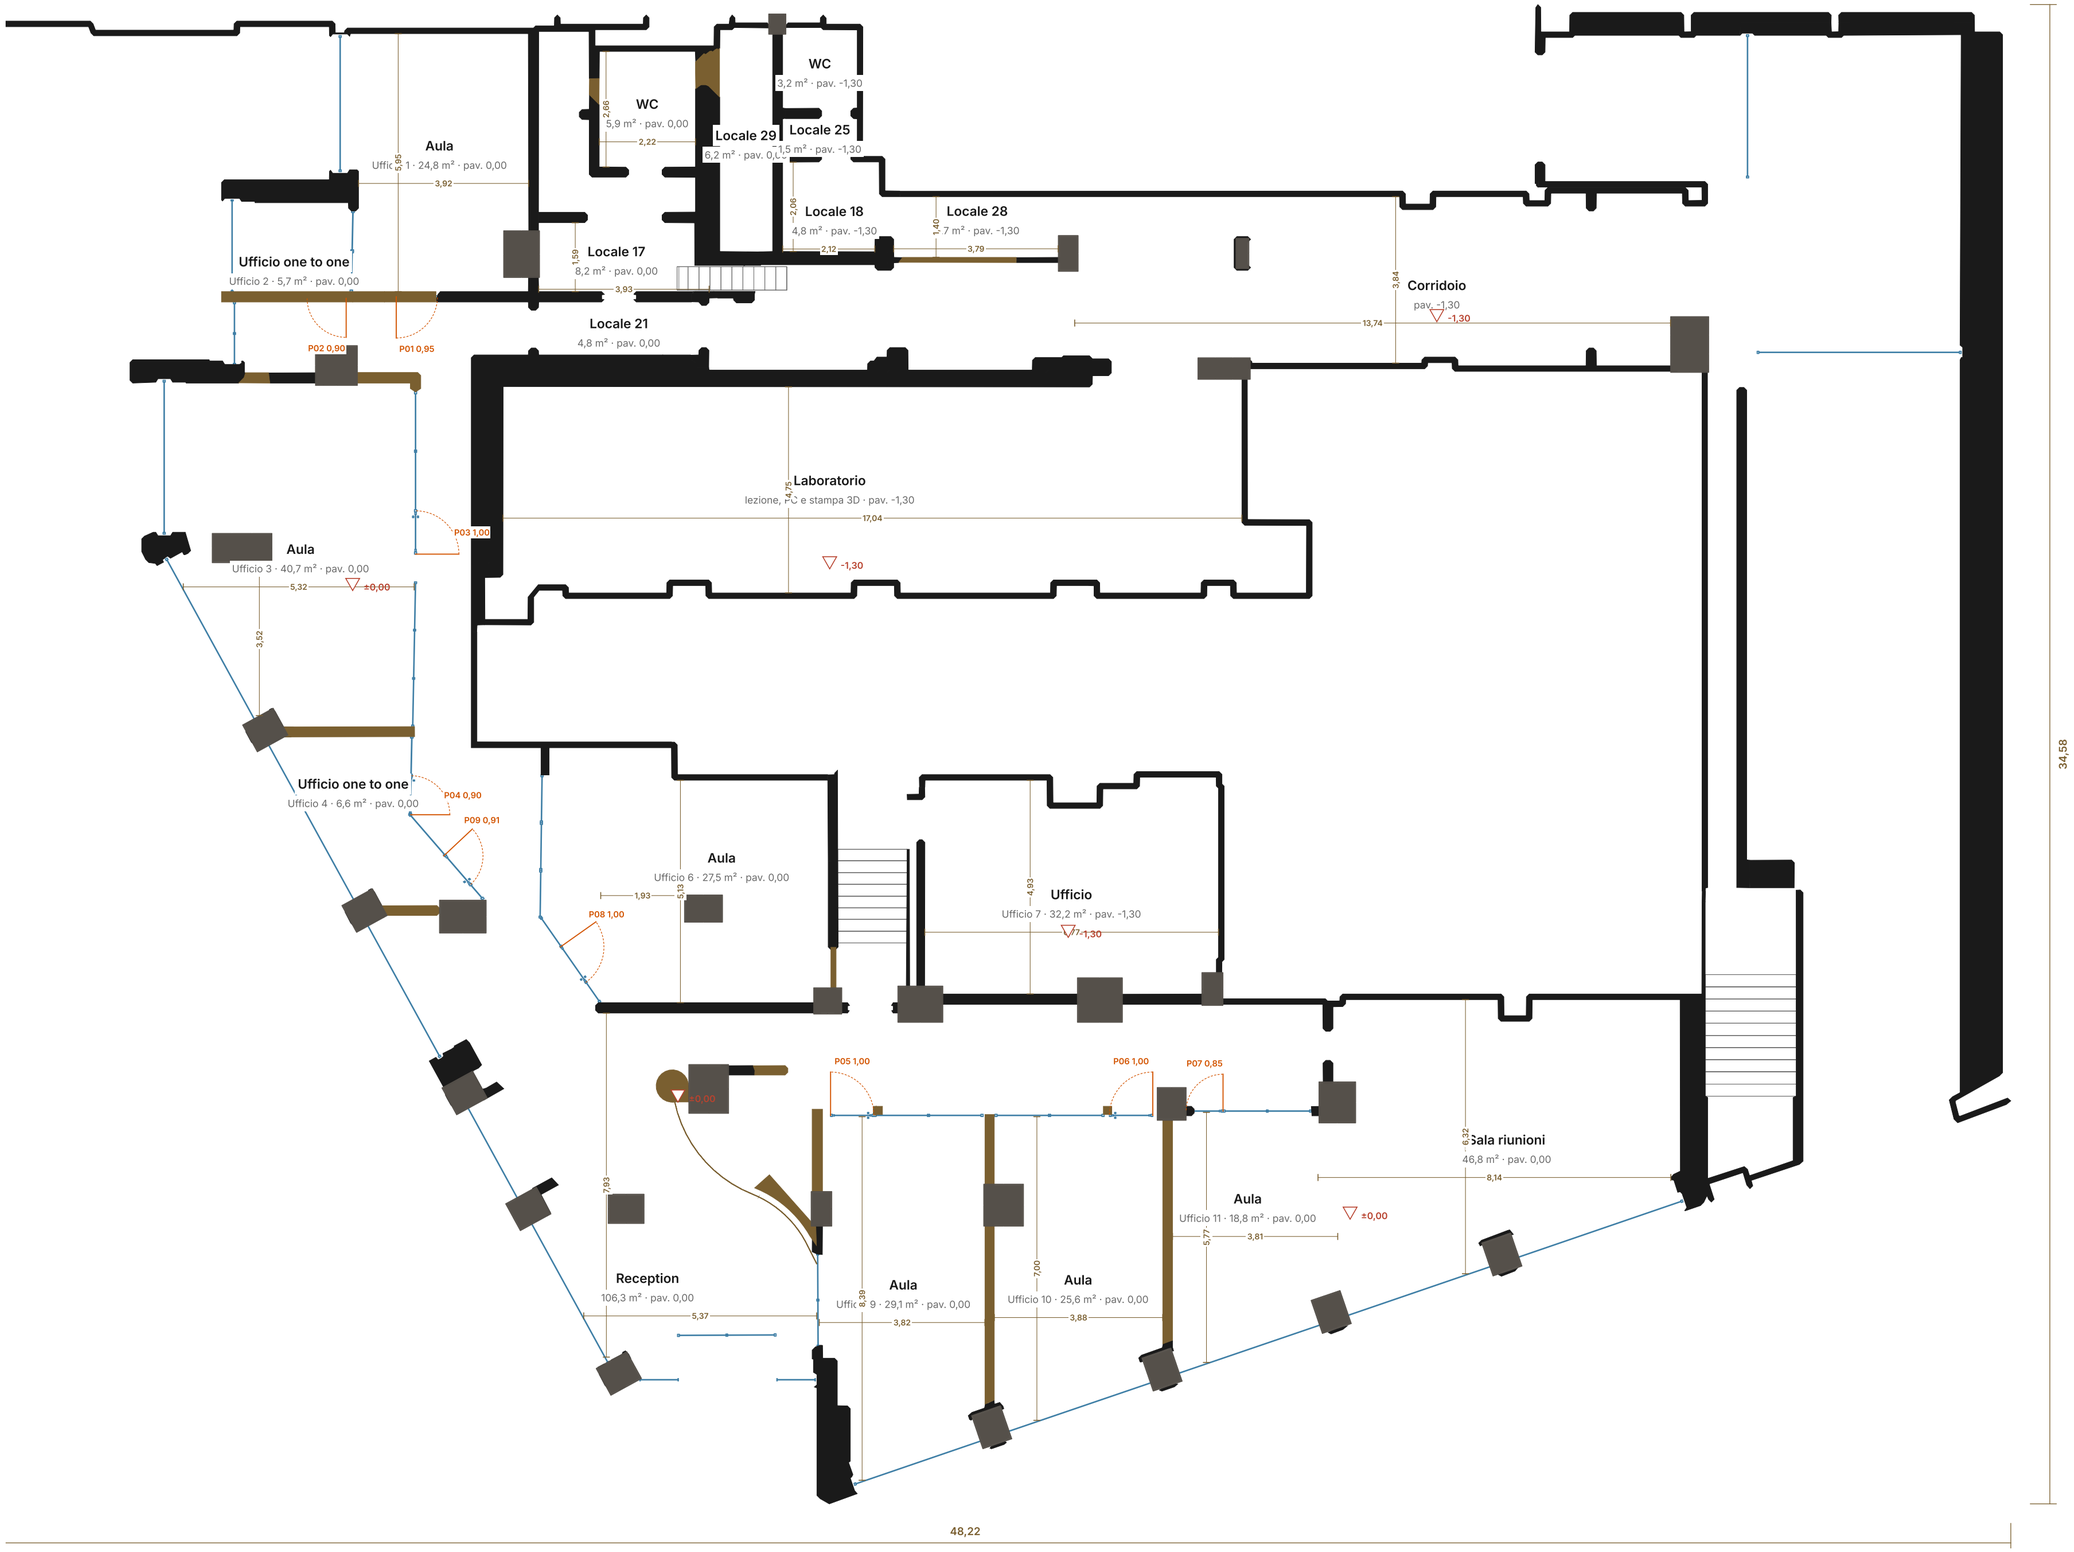



FUTURA
FORMAZIONE • LAVORO

# Pianta quotata

Misure nette dei locali e ingombro generale (m), porte in vetro con luce, quote dei pavimenti. Da verificare in sito.

LEGENDA

- Murature esistenti
- Murature nuove
- Pilastri
- Pareti vetrate e vetrine
- Porte in vetro
- Misure nette (m)
- Quote del pavimento

SCALA 1:100 SU FOGLIO A2

0 — 5 m

VISIO Studio · Michelessi Corporation Srl
Bozza del 9 novembre 2026