

Sezione F–F

Aula 3, corridoio, one to one e Aula 1 · 1:50

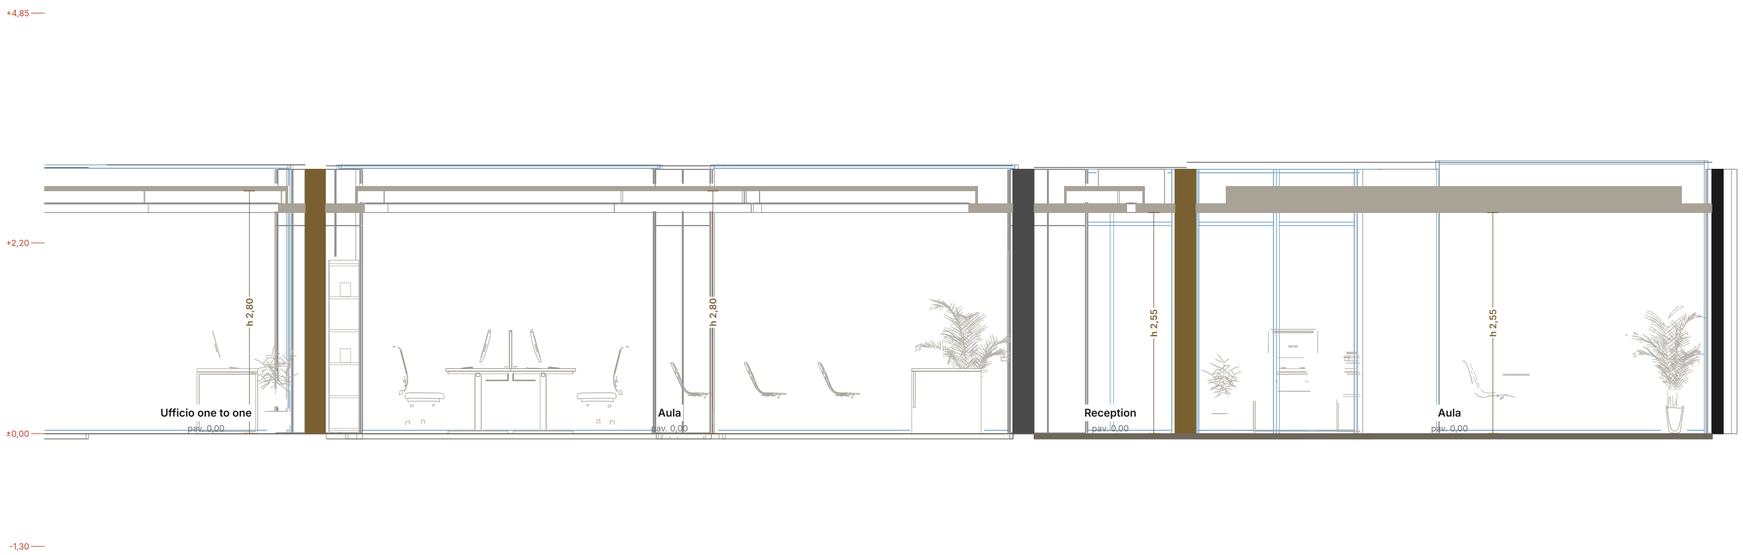

Chiave delle sezioni · 1:250

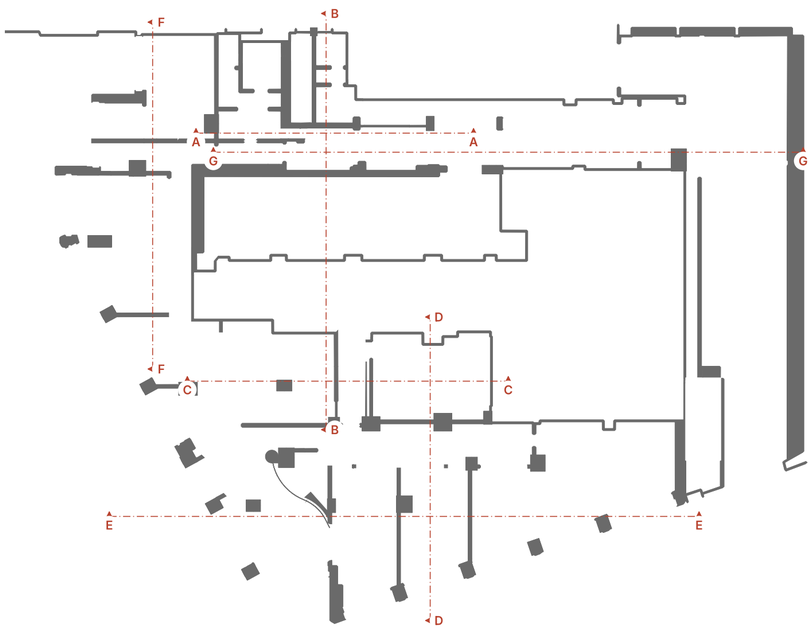

FUTURA
FORMAZIONE • LAVORO

TAVOLA S03

Sezioni
F

Dal modello 3D aggiornato
Viste oltre il taglio
senza linee nascoste

LEGENDA

- Murature tagliate
- Murature nuove
- Pilastri
- Pavimenti e solaio
- Controsoffitti
- Vetro tagliato
- Vista oltre il taglio
- Arredi in vista
- Altezze nette (m)
- Quote di riferimento

SCALA 1:50 SU FOGLIO A2

0 — 2 m

VISIO Studio · Michelessi Corporation Srl
Bozza del 9 novembre 2026