
Stato attuale

Piano terra e seminterrato come sono oggi




Piano terra · h netta 3,00 m

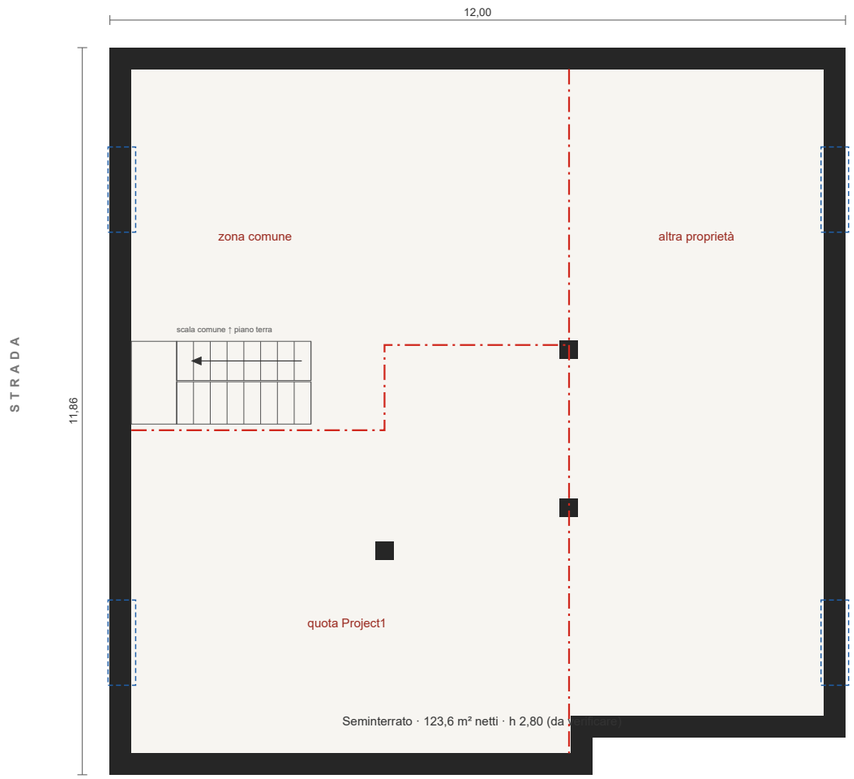


Seminterrato · oggi C/2

Progetto

Due unità: A al piano terra, B su piano terra e seminterrato con scala interna

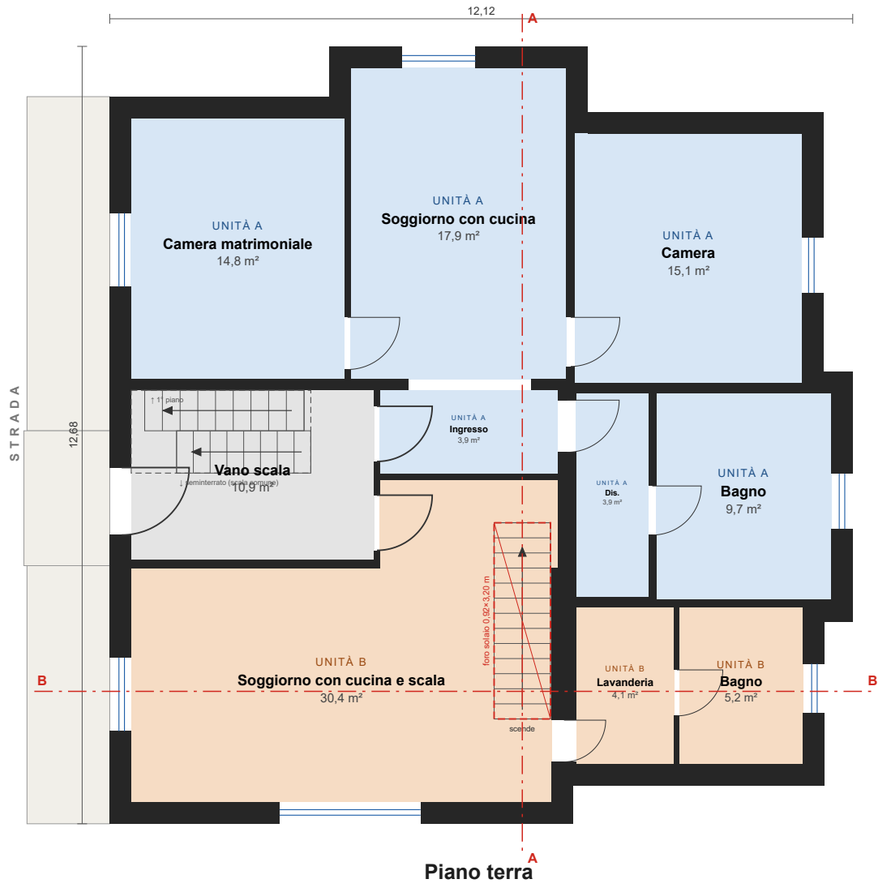

Piano terra

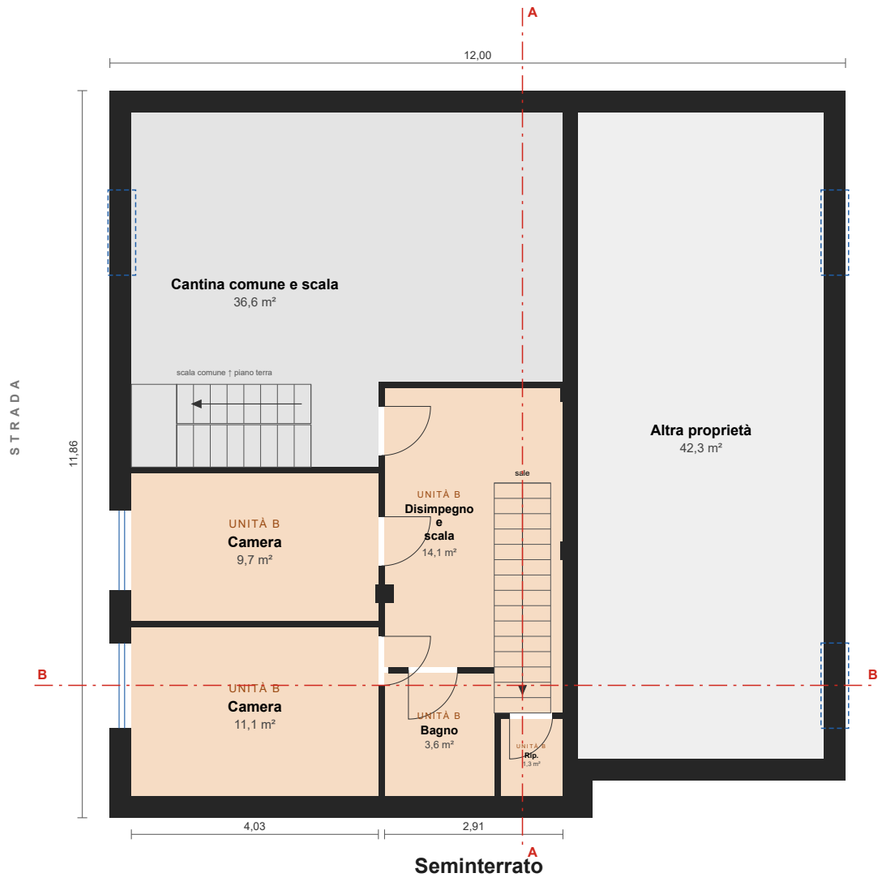


Seminterrato

Unità A · solo piano terra · 65,3 m² netti Unità B · duplex · 39,6 + 39,8 m² netti parti comuni


Tav. 02 Scala 1:100 (A3) Misure indicative: da verificare in sito

Demolizioni e costruzioni

Confronto tra stato attuale e progetto (gialli e rossi)

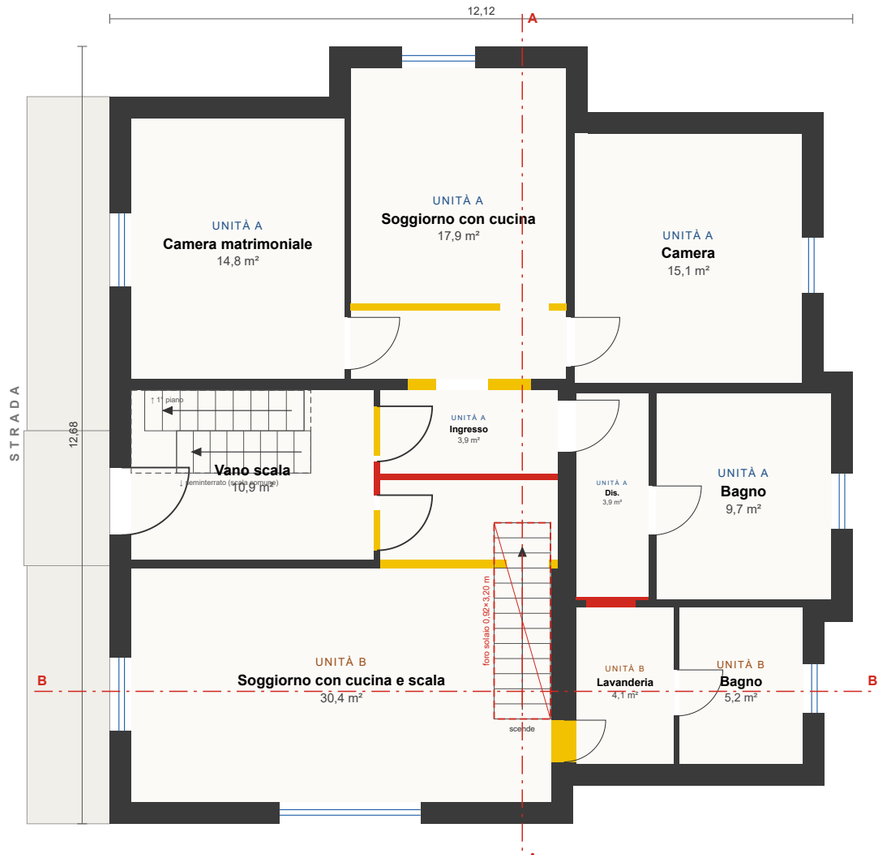

Piano terra

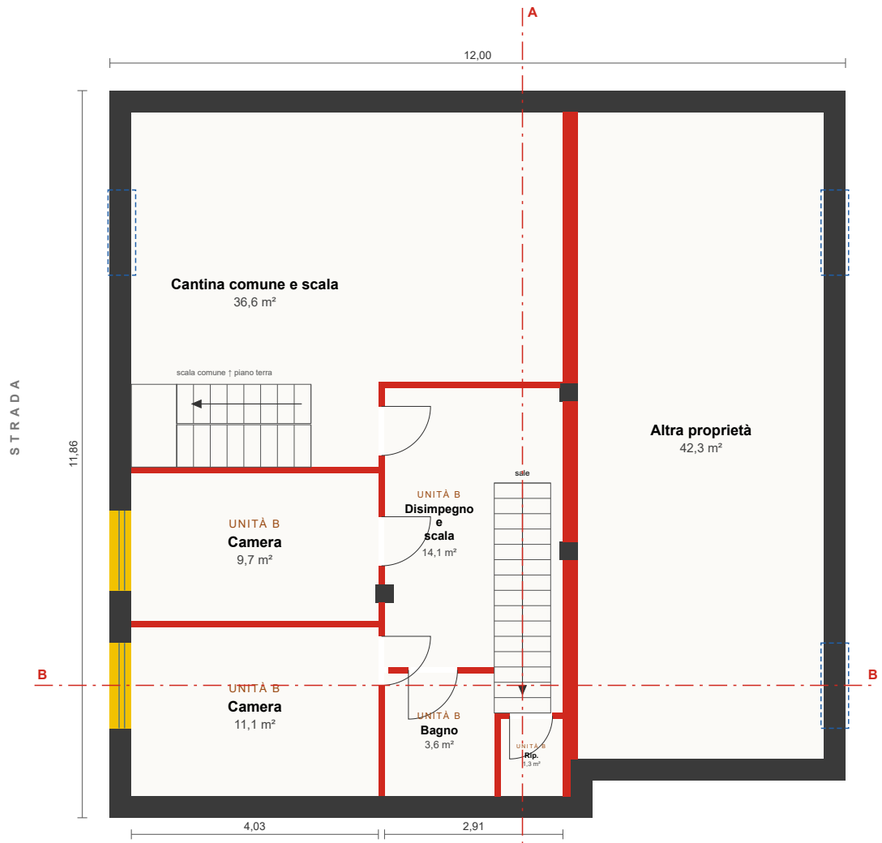

Seminterrato

muri esistenti · demolizioni · nuove costruzioni


Tav. 03 Scala 1:100 (A3) Misure indicative: da verificare in sito

Sezioni

Scala interna dell'unità B e finestre ribassate del seminterrato

Sezione A–A

taglio nord–sud sulla scala interna (nord a sinistra)

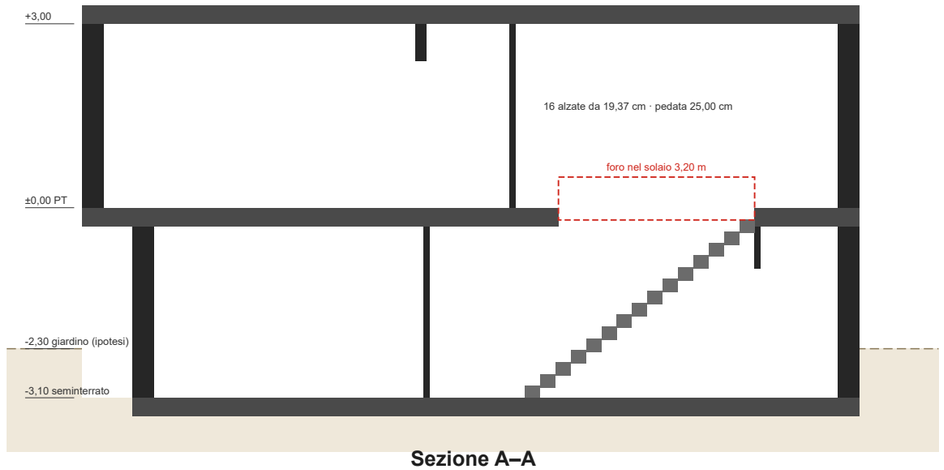

Sezione A–A

Sezione B–B

taglio ovest–est sulle camere del seminterrato (strada a sinistra)



Sezione B–B