
Stato attuale

Piano terra dal rilievo Polycam, seminterrato dalla planimetria, vano scala condominiale




Piano terra · h netta 3,00 m

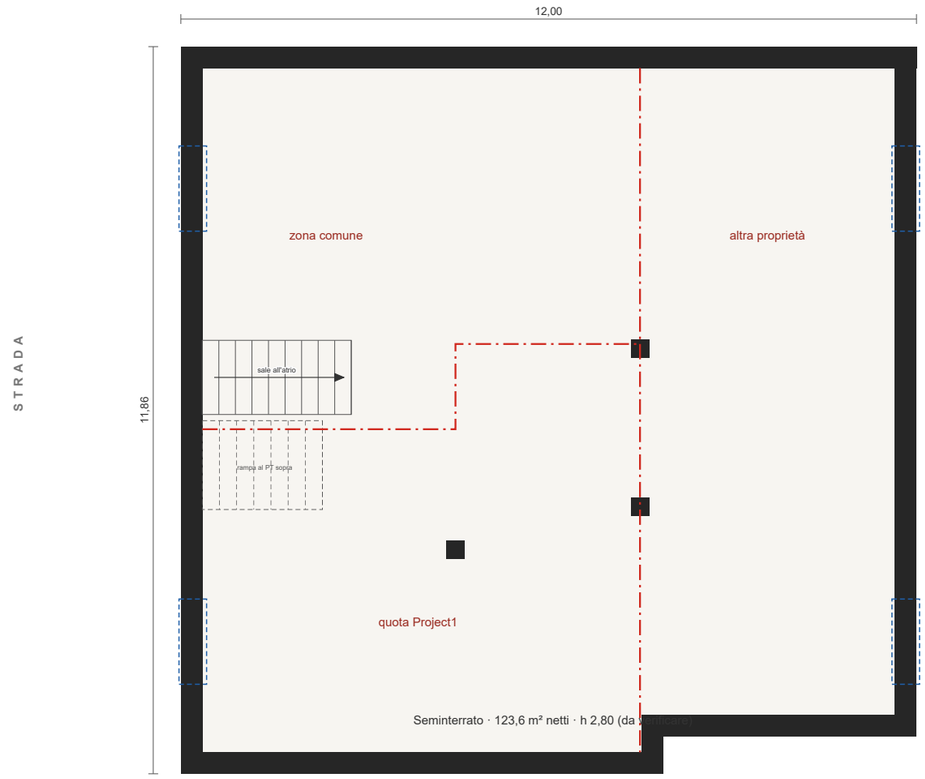


Seminterrato · oggi C/2

Progetto

Unità A: open space sul fronte, due camere e bagno sul retro · Unità B: duplex con scala interna

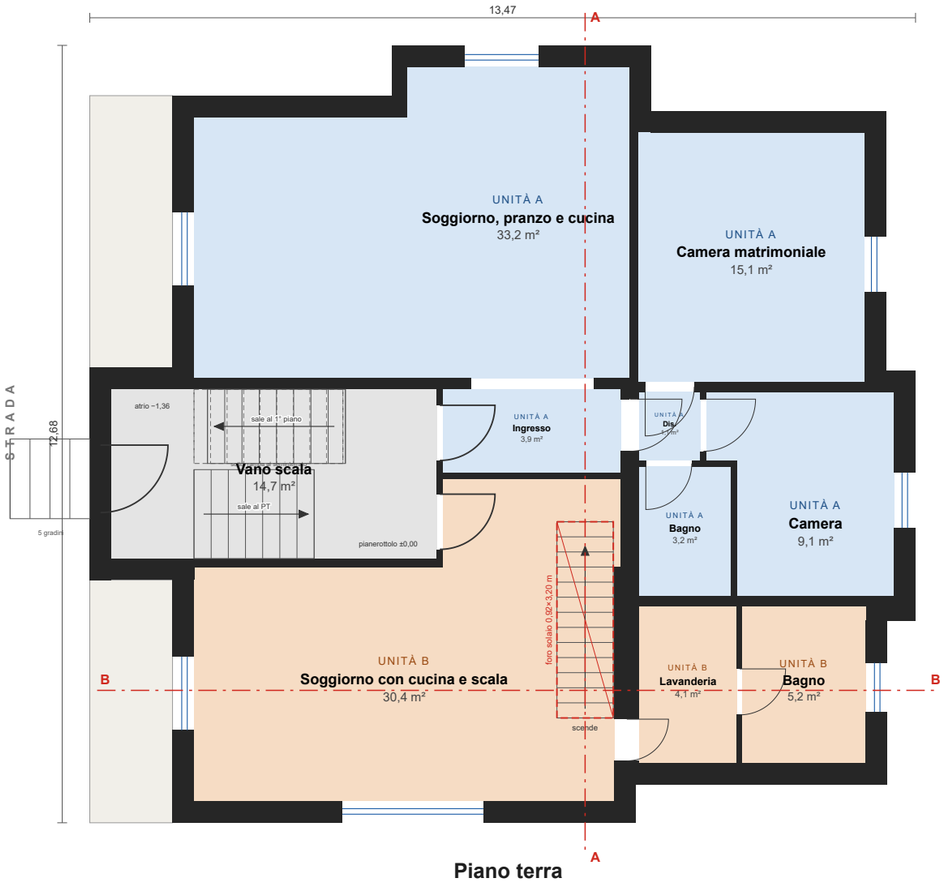

Piano terra

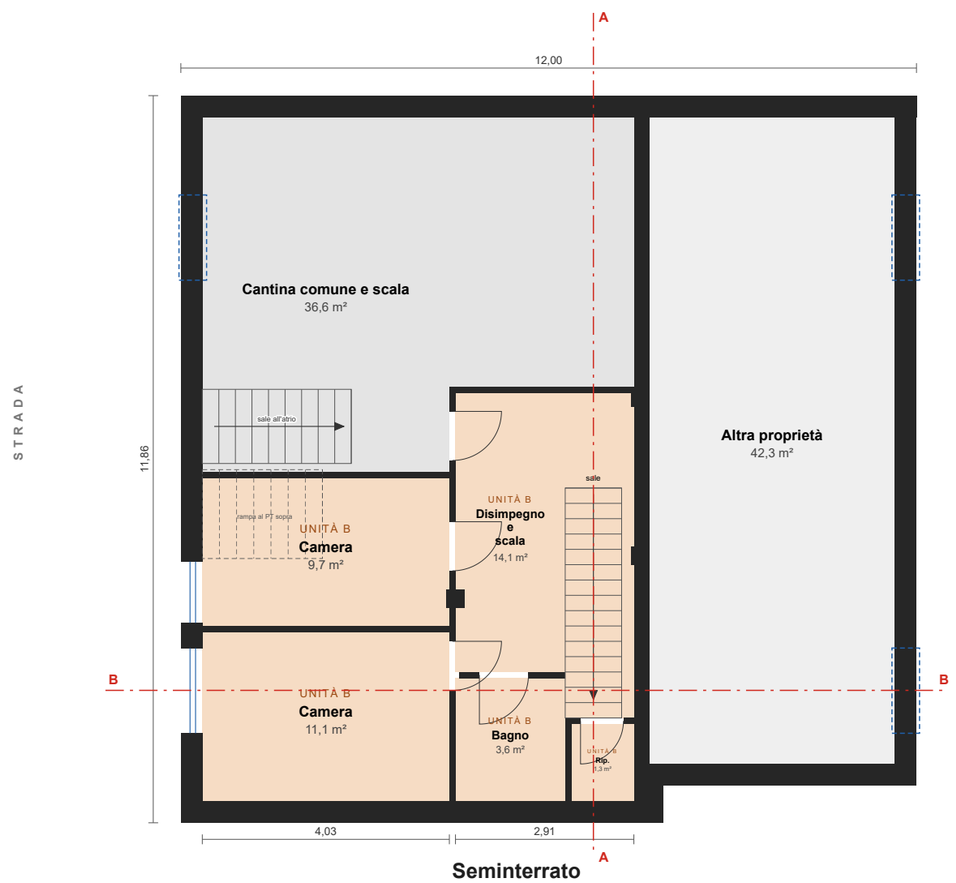


Seminterrato

Unità A · 65,6 m² netti Unità B · 39,6 + 39,8 m² netti parti comuni


Tav. 02 Scala 1:100 (A3) Da verificare in sito

Demolizioni e costruzioni

Confronto tra stato attuale e progetto

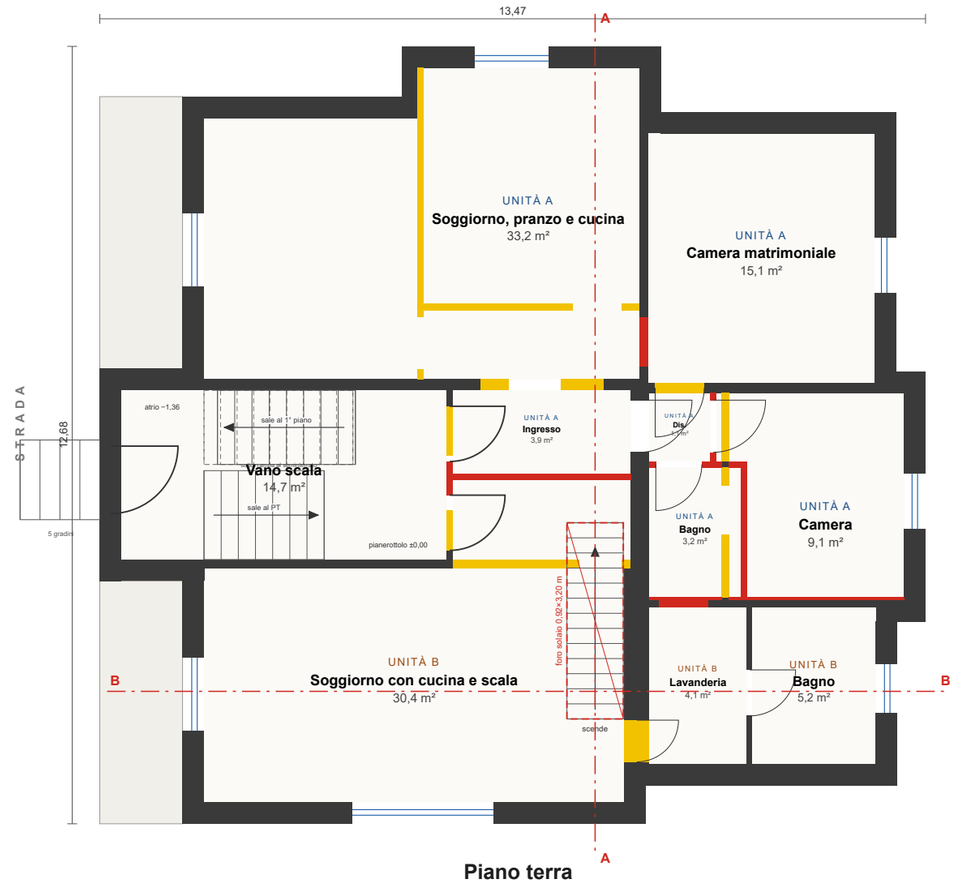

Piano terra

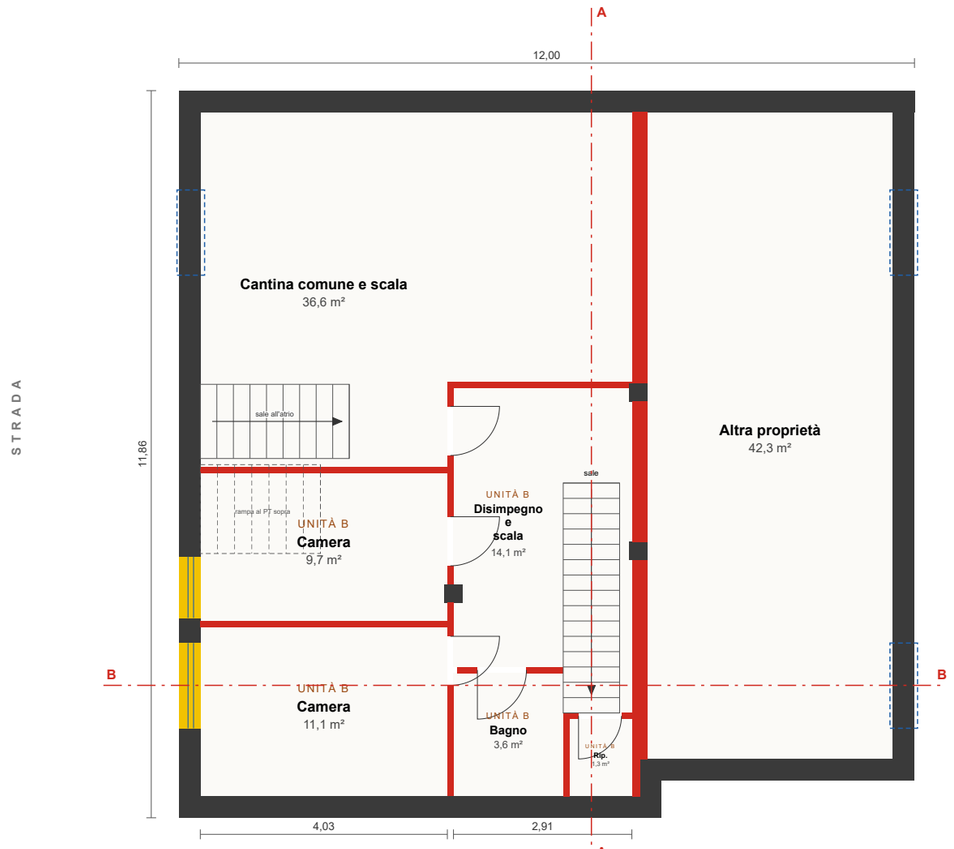

Seminterrato

esistente demolizioni nuove costruzioni


Tav. 03 Scala 1:100 (A3) Da verificare in sito

Sezioni

Scala interna dell'unità B e finestre ribassate del seminterrato

Sezione A–A

taglio nord–sud sulla scala interna (nord a sinistra)

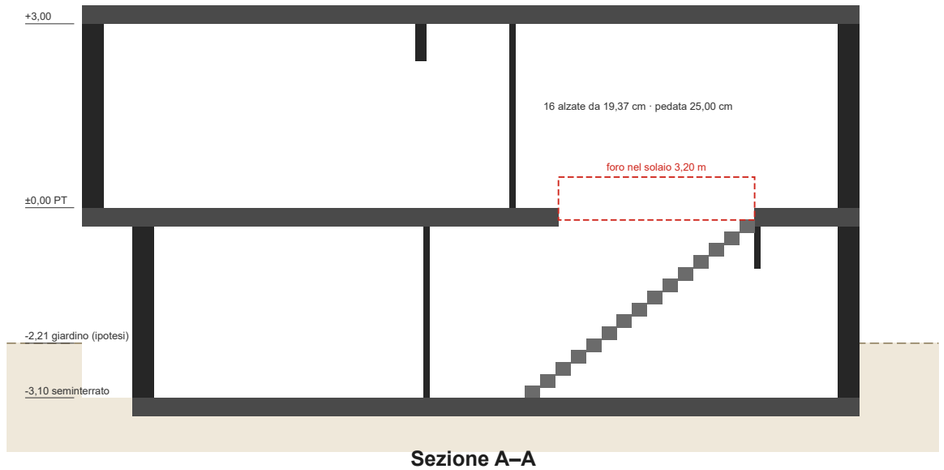

Sezione A–A

Sezione B–B


taglio ovest–est sulle camere del seminterrato (strada a sinistra)



Sezione B–B

Arredi e pavimenti

Arredo minimal con passaggi verificati; pavimento in gres effetto resina chiaro, neutro freddo, lastre 120 × 60 cm con fuga 2 mm

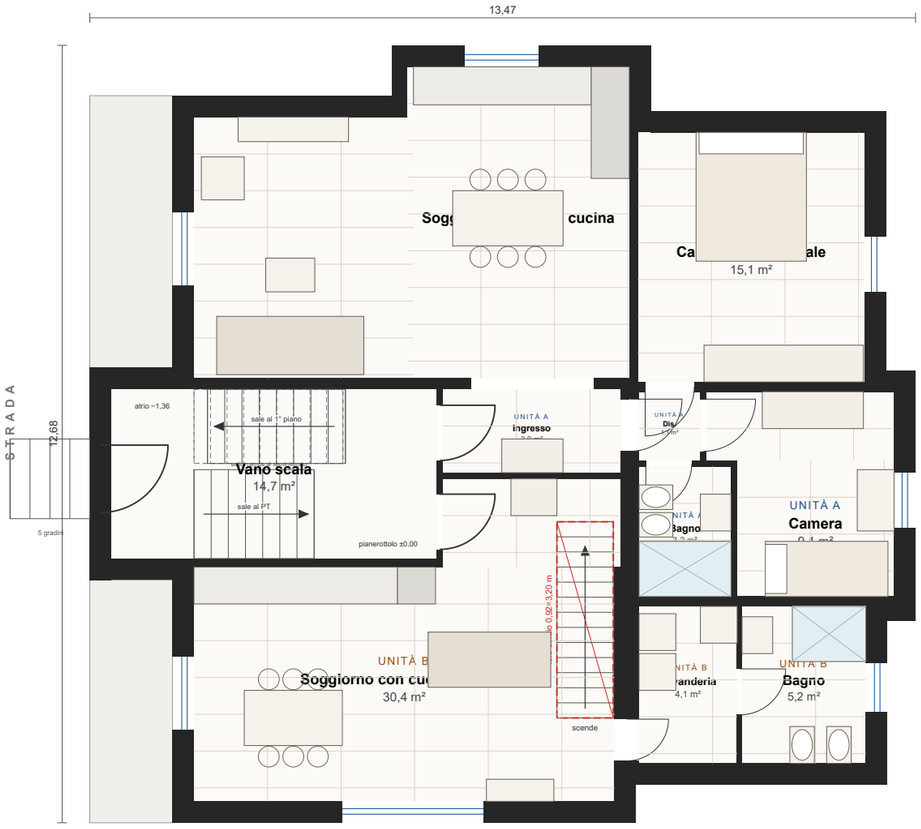

Piano terra



Seminterrato

lastre 120 × 60, fuga 2 mm arredi e sanitari Pavimento: A 65,6 m² · B 76,5 m²

Controsoffitti e illuminazione

Cartongesso a soffitto con gola LED perimetrale nelle zone giorno e notte, faretti a incasso, sospensioni su isola e tavolo



Piano terra




Seminterrato

h 2,80 (velette e gola) · h 2,70 · h 2,40 (passaggio impianti) · gola LED · Faretti A 20 · B 44 · LED 78,3 ml

Tav. 06 · Scala 1:100 (A3) · Da verificare in sito

Impianto elettrico

Rifacimento completo: un quadro per unità, punti luce, comandi, prese, linee dedicate, TV, dati, videocitofono, termostati

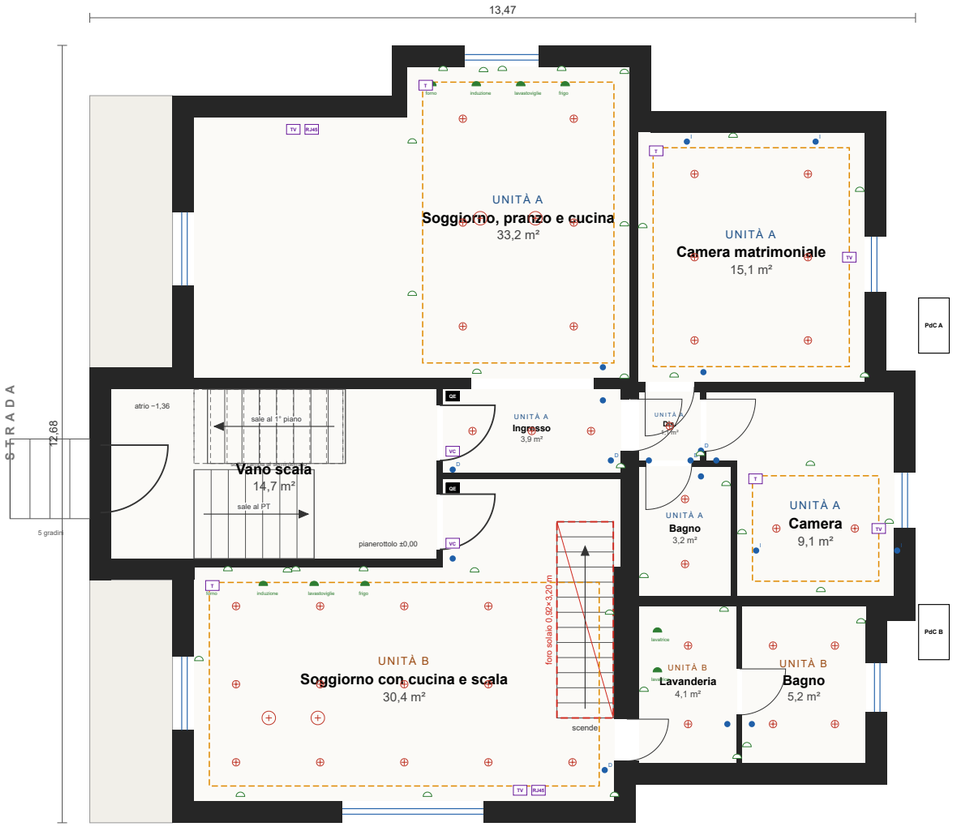

Piano terra




Seminterrato

punto luce · comando (D deviatore, I invertitore) · presa · linea dedicata · QE quadro elettrico · Dotazioni almeno livello 1 CEI 64-8/3

Impianto idrico-sanitario e termico

Pompa di calore aria-acqua per unità, accumulo ACS, pavimento radiante, collettori, nuove colonne di scarico; seminterrato con stazione di sollevamento

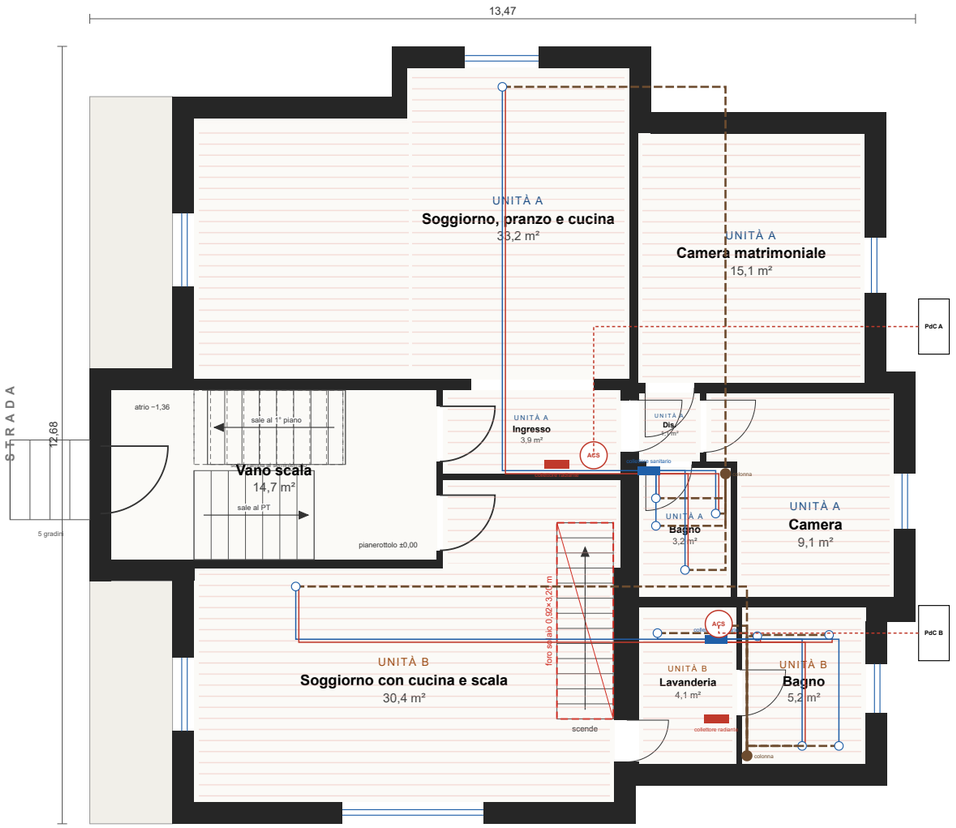

Piano terra




Seminterrato

acqua fredda · acqua calda e radiante · scarico · pavimento radiante · Punti acqua A 5 · B 10

Tav. 08 Scala 1:100 (A3) Da verificare in sito

Sistemazione esterna

Lotto ricalcato dalla vista satellitare dall'alto e registrato sull'edificio: il fronte su via Cagliari è ruotato di circa 25° rispetto alla casa · scala 1:200, precisione ±1 m

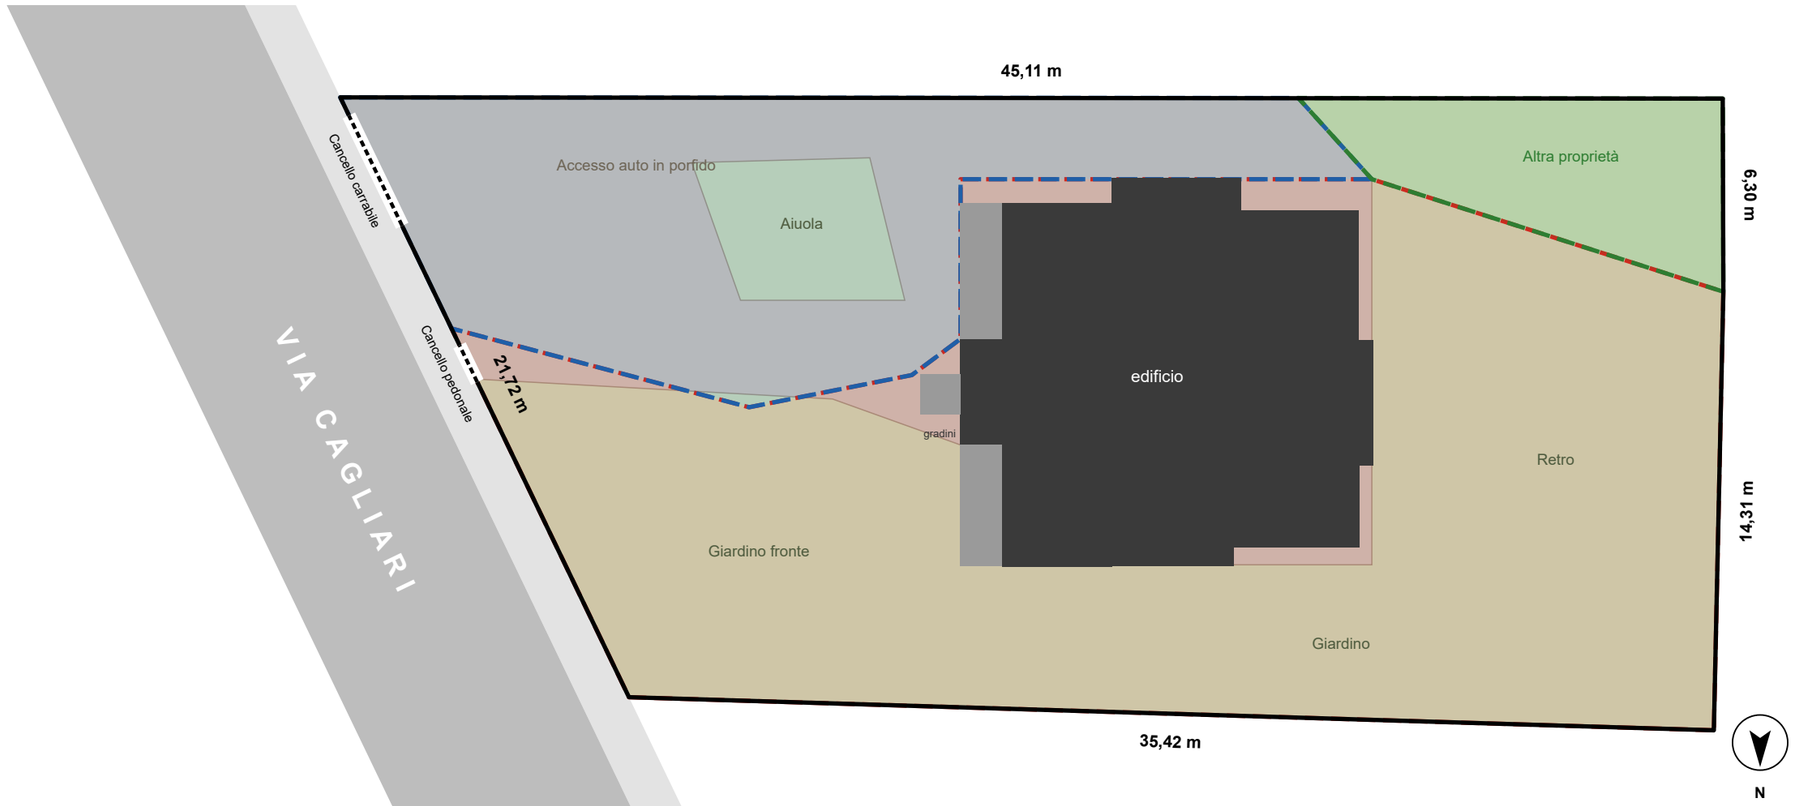


Corte e accessi

porfido · giardino · Project1 · comune: accesso auto e vialetto · altra proprietà · Lotto ≈ 807 m² · Project1 ≈ 557 m² edificio compreso · comune ≈ 196 m²

Planimetria arredata e punti di vista

Ogni numero è la posizione della camera di un render: stessa camera nel modello 3D e nel render, arredi nelle stesse posizioni

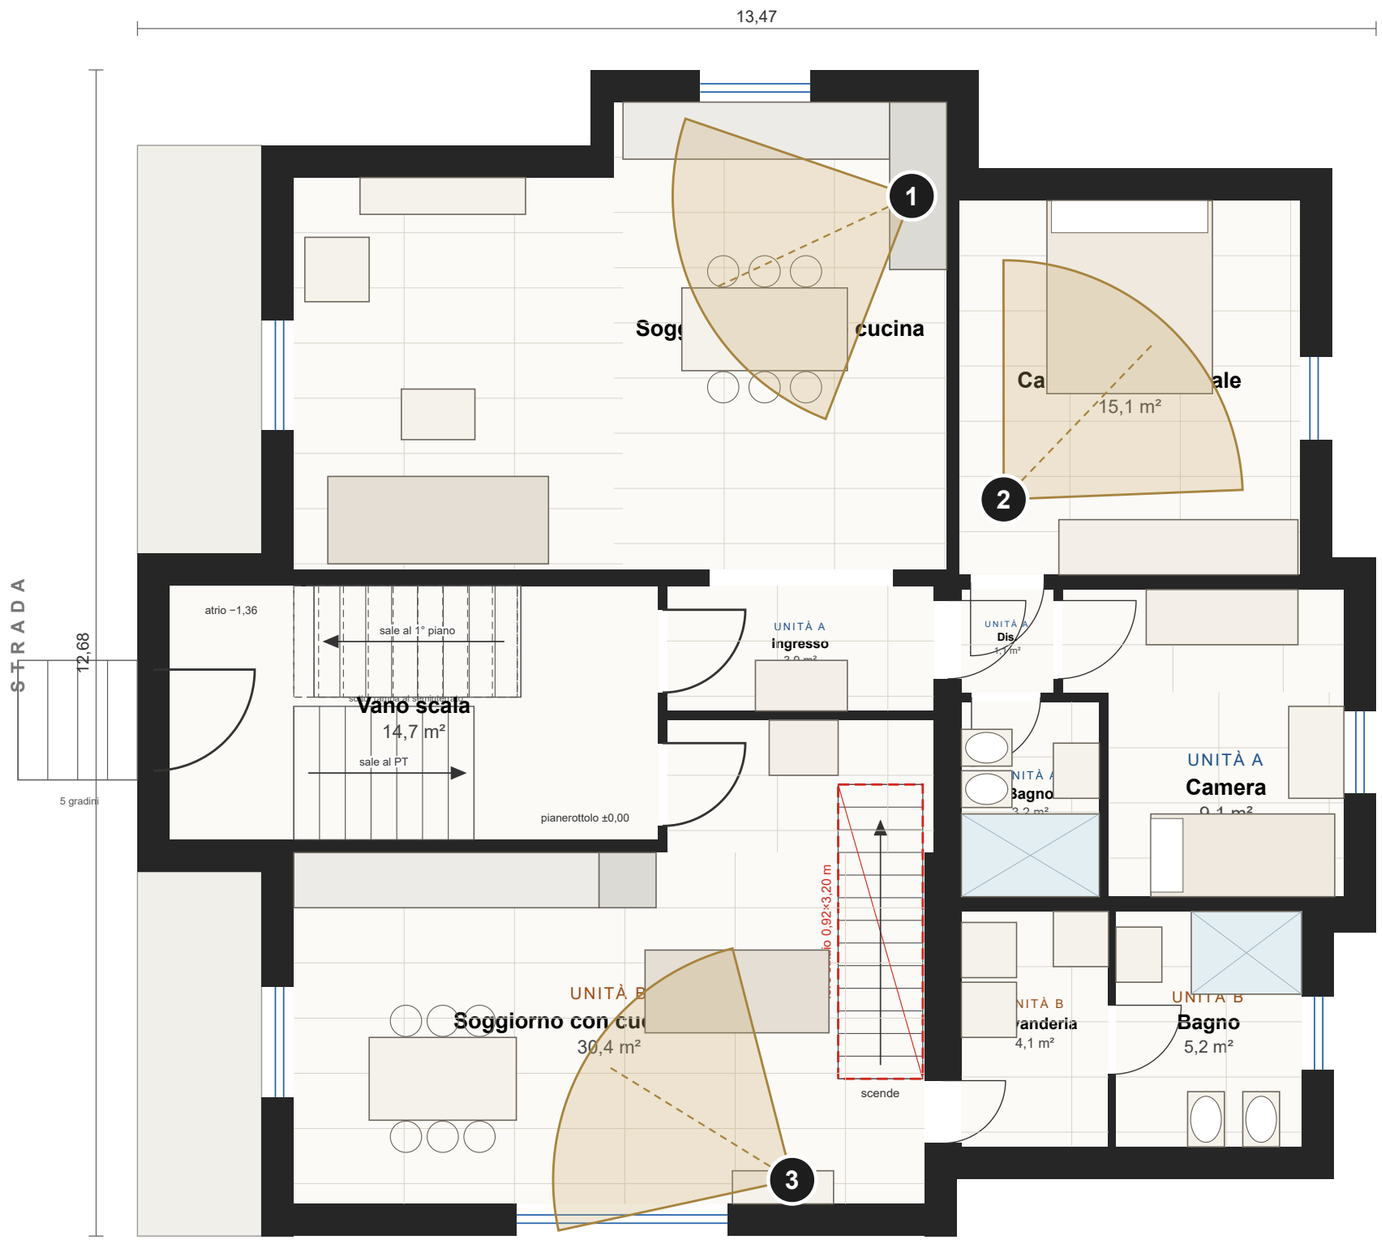

Piano terra arredato · scala 1:67

1 Open space A **2** Camera matrimoniale A **3** Soggiorno con cucina B campo visivo della camera (fov 62°, 16:10)